




S&L Harris/Day Architecture

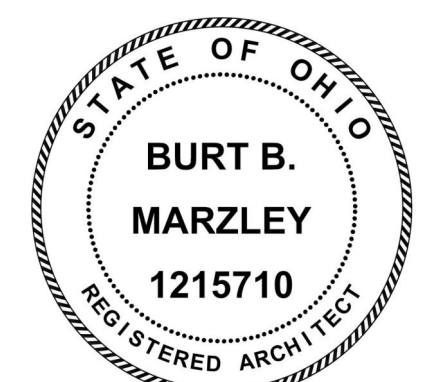

BURT B. MARZLEY, LICENSE # 1215710
EXPIRATION DATE 12/15/2025
not published; all rights reserved


TYPICAL WALL SECTION NOTES

1. ALL WORK SHALL CONFORM TO THE FEDERAL, STATE AND LOCAL CODES AND REQUIREMENTS.
2. COORDINATE DIMENSIONS WITH STRUCTURAL DRAWINGS - TYPICAL.
3. ALL CONTRACTORS TO COORDINATE WITH STRUCTURAL, ARCHITECTURAL, PLUMBING, MECHANICAL AND ELECTRICAL DRAWINGS.
4. ALL DIMENSIONS THAT ARE UNCLEAR OR UN-INDICATED SHALL BE VERIFIED WITH THE ARCHITECT. EACH CONTRACTOR SHALL VERIFY ALL DIMENSIONS AND CLEARANCES BEFORE PROCEEDING WITH THEIR WORK. COMMENCEMENT OF THE WORK CONSTITUTES ACCEPTANCE OF THE EXISTING AND/OR NEW CONDITIONS.
5. NON-COMBUSTIBLE BLOCKING SHALL BE REQUIRED IN STUD WALLS FOR EQUIPMENT, CASEWORK, TOILET ACCESSORIES, HANDRAILS, ETC. NON-COMBUSTIBLE BLOCKING TO BE FURNISHED AND INSTALLED BY THE TRADE, REQUIRING THE BLOCKING FOR ALL OWNER-SUPPLIED EQUIPMENT INDICATED ON THE DRAWINGS. NON-COMBUSTIBLE BLOCKING SHALL BE FURNISHED AND INSTALLED BY FRAMING CONTRACTOR.
6. FILL IN ALL MASONRY VOIDS WITH MORTAR OR CONCRETE WHERE MASONRY ANCHORS OCCUR.
7. ALL OUTSIDE DRYWALL CORNERS ARE TO RECEIVE A STRUCTURAL LAMINATE CORNER BEAD AS DEFINED IN THE SPECIFICATION SECTION 09 59 00. ONLY REQUIRED WITHIN 8'-0" OF FINISH FLOOR. NOT REQUIRED ON SOFFITS.

TYP. CMU MASONRY WALL W/ METAL SIDING WALL CONSTRUCTION (INTERIOR TO EXTERIOR)


INSIDE AIR FILM	R-0.68
8-12" CMU	R-1.28
2.5" SPRAY FOAM	R-16
0.5" AIR SPACE	R-0.5
METAL SIDING	R-0
OUTSIDE AIR FILM	R-0.17

TOTAL WALL R-VALUE 18.63

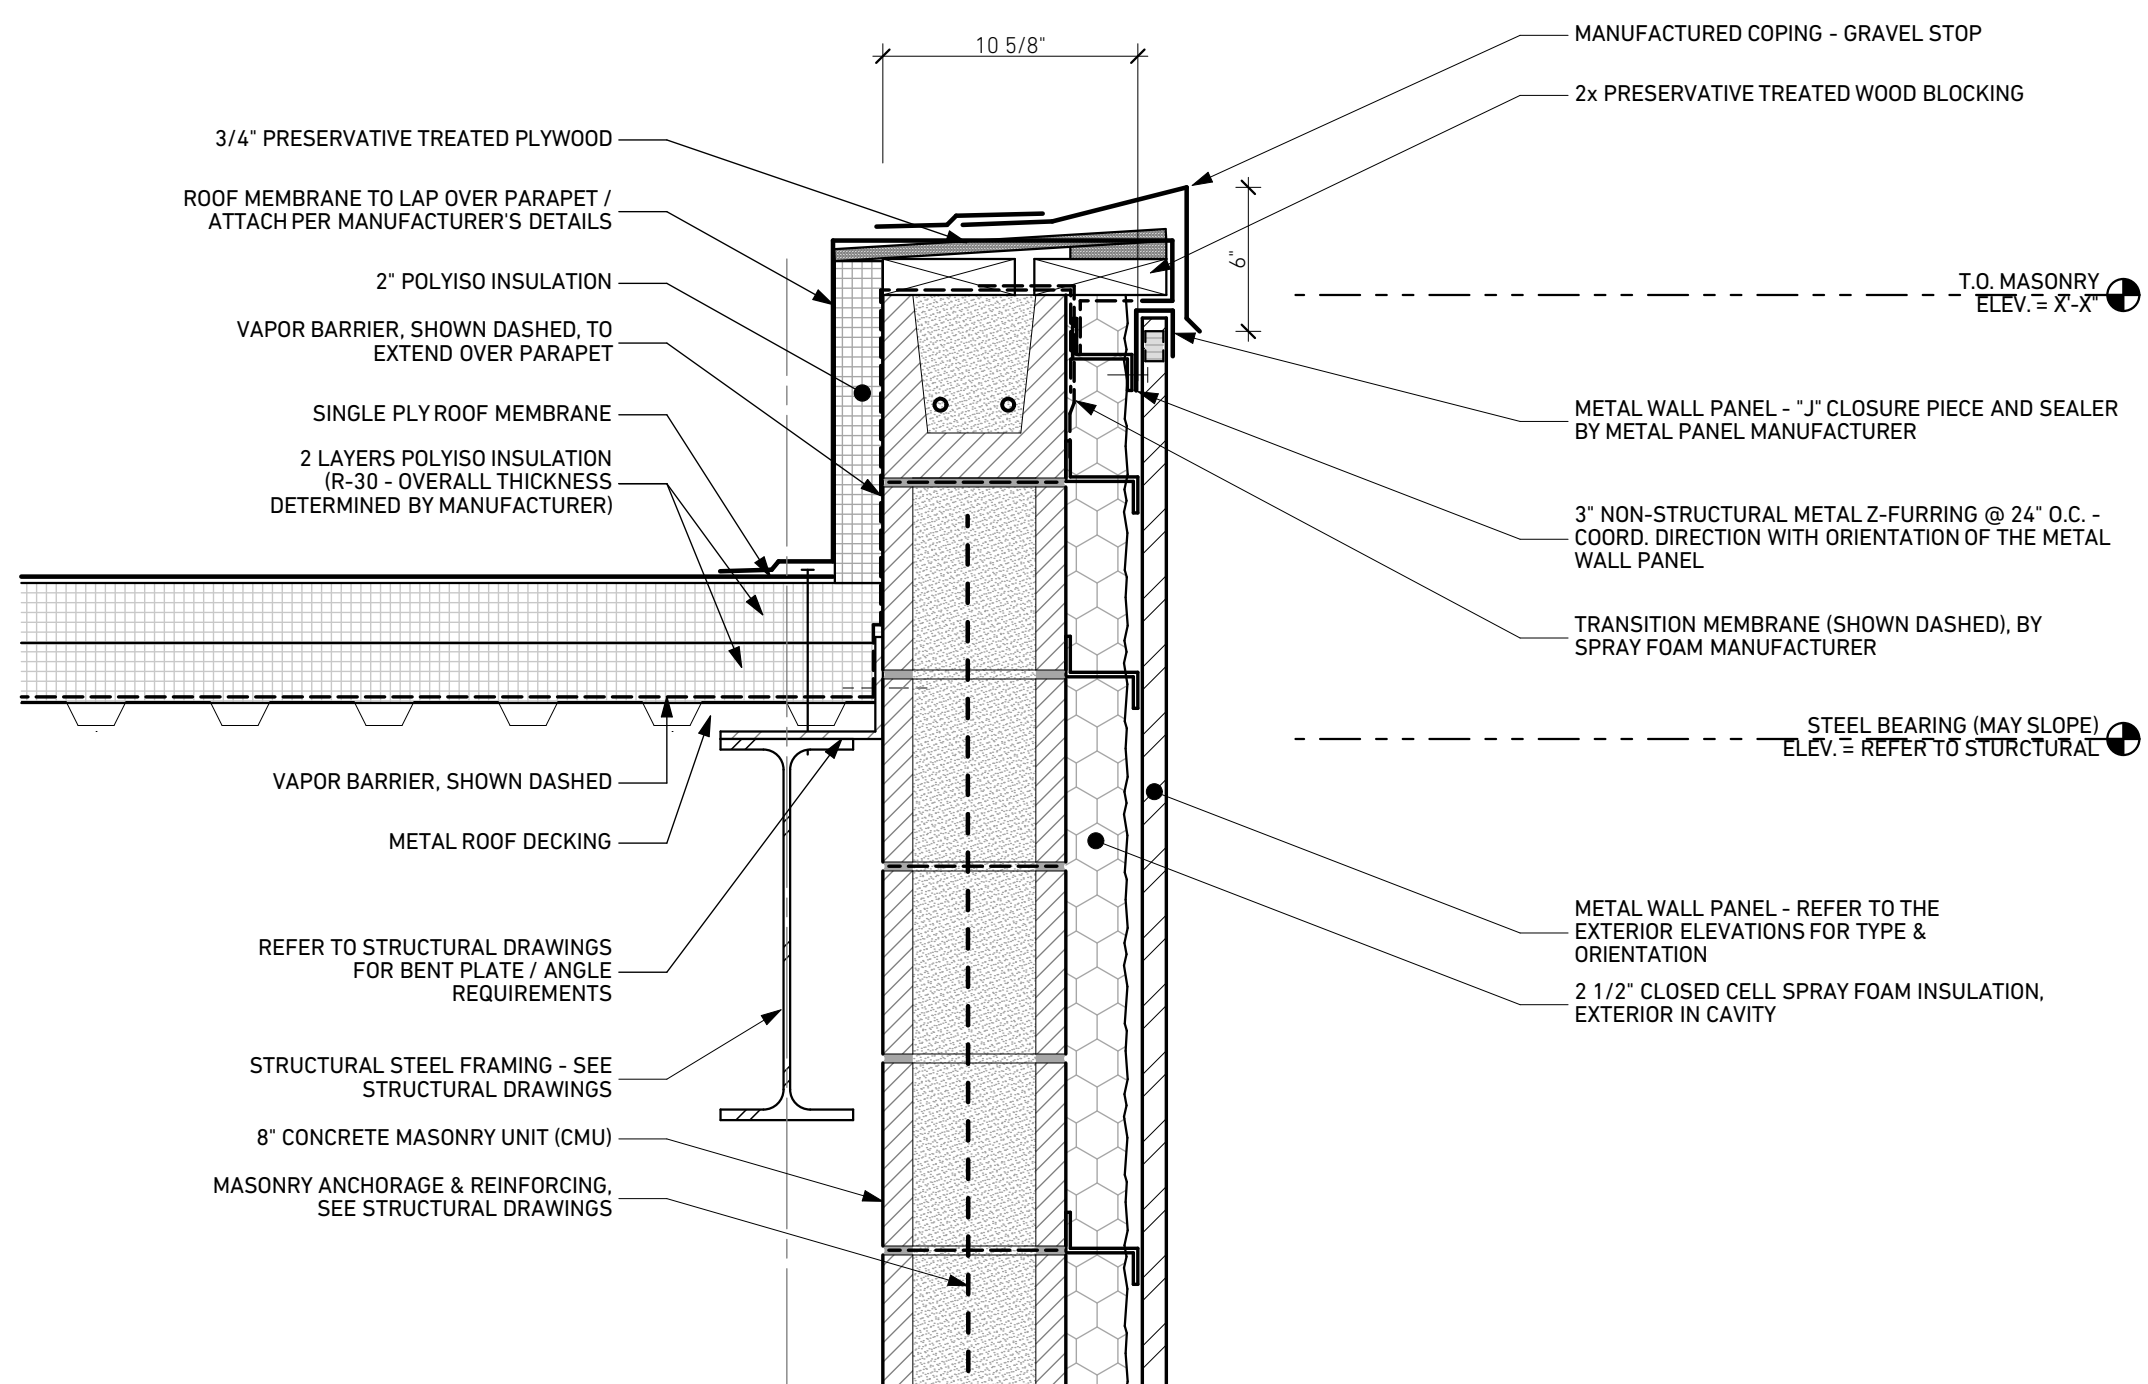


D2 TYPICAL 8" CMU WALL WITH METAL PANEL [PARAPET]

SCALE: 1 1/2" = 1'-0"

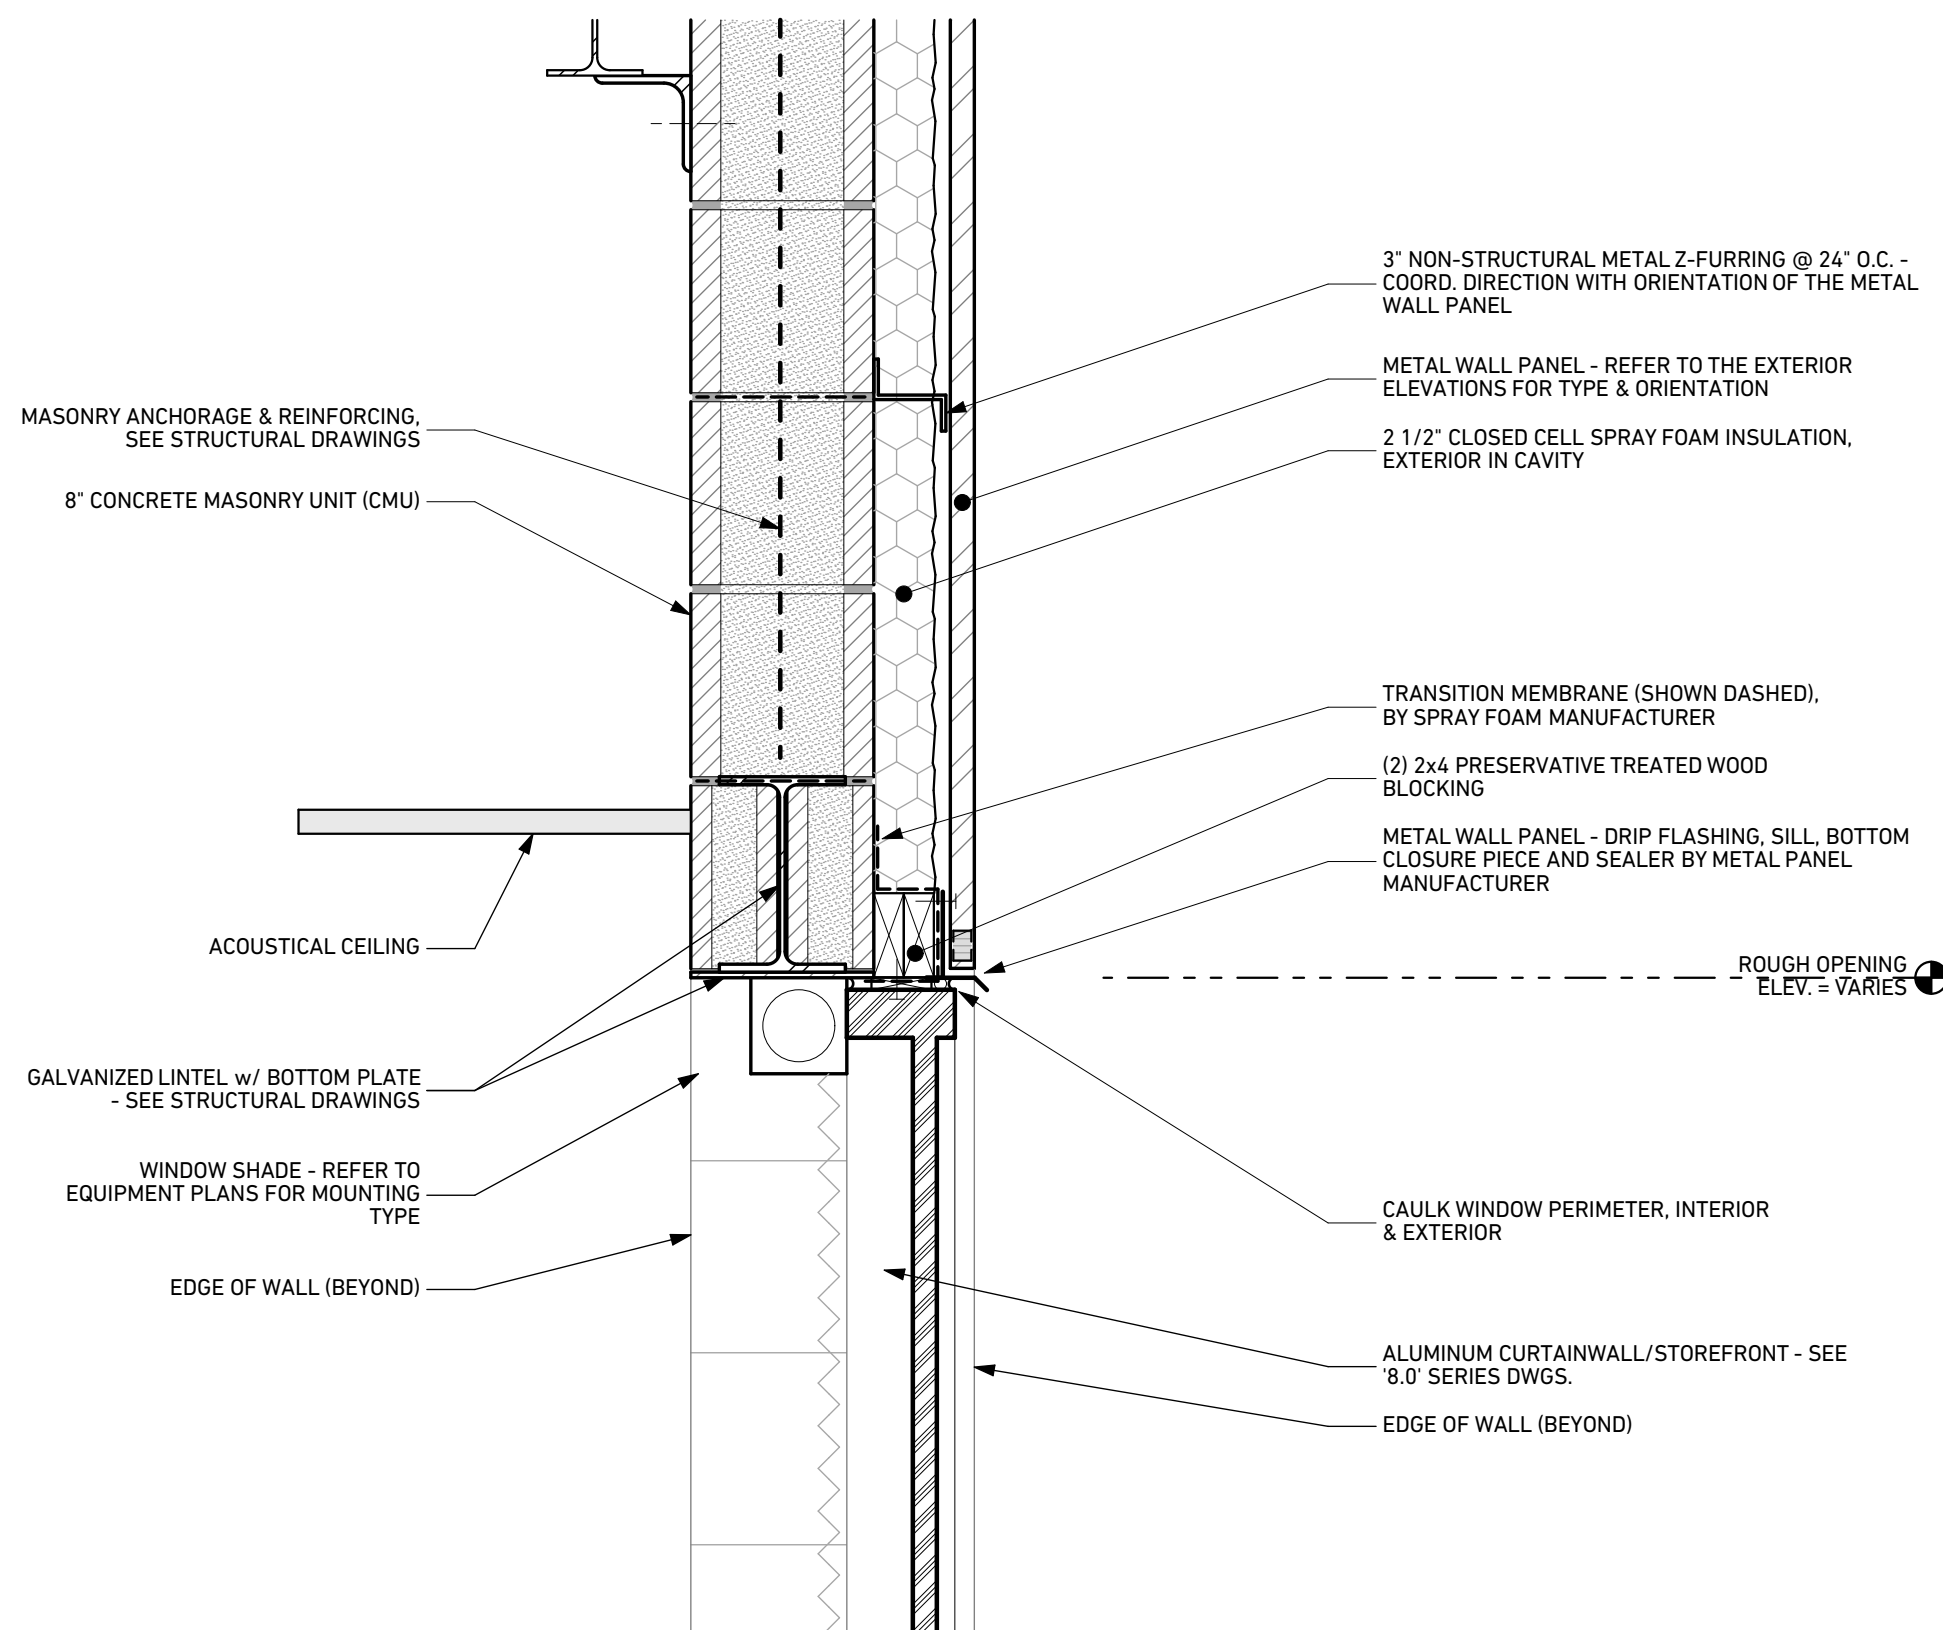


B4 TYPICAL 8" CMU WALL WITH METAL PANEL [LINTEL & PLATE HEADER]

SCALE: 1 1/2" = 1'-0"

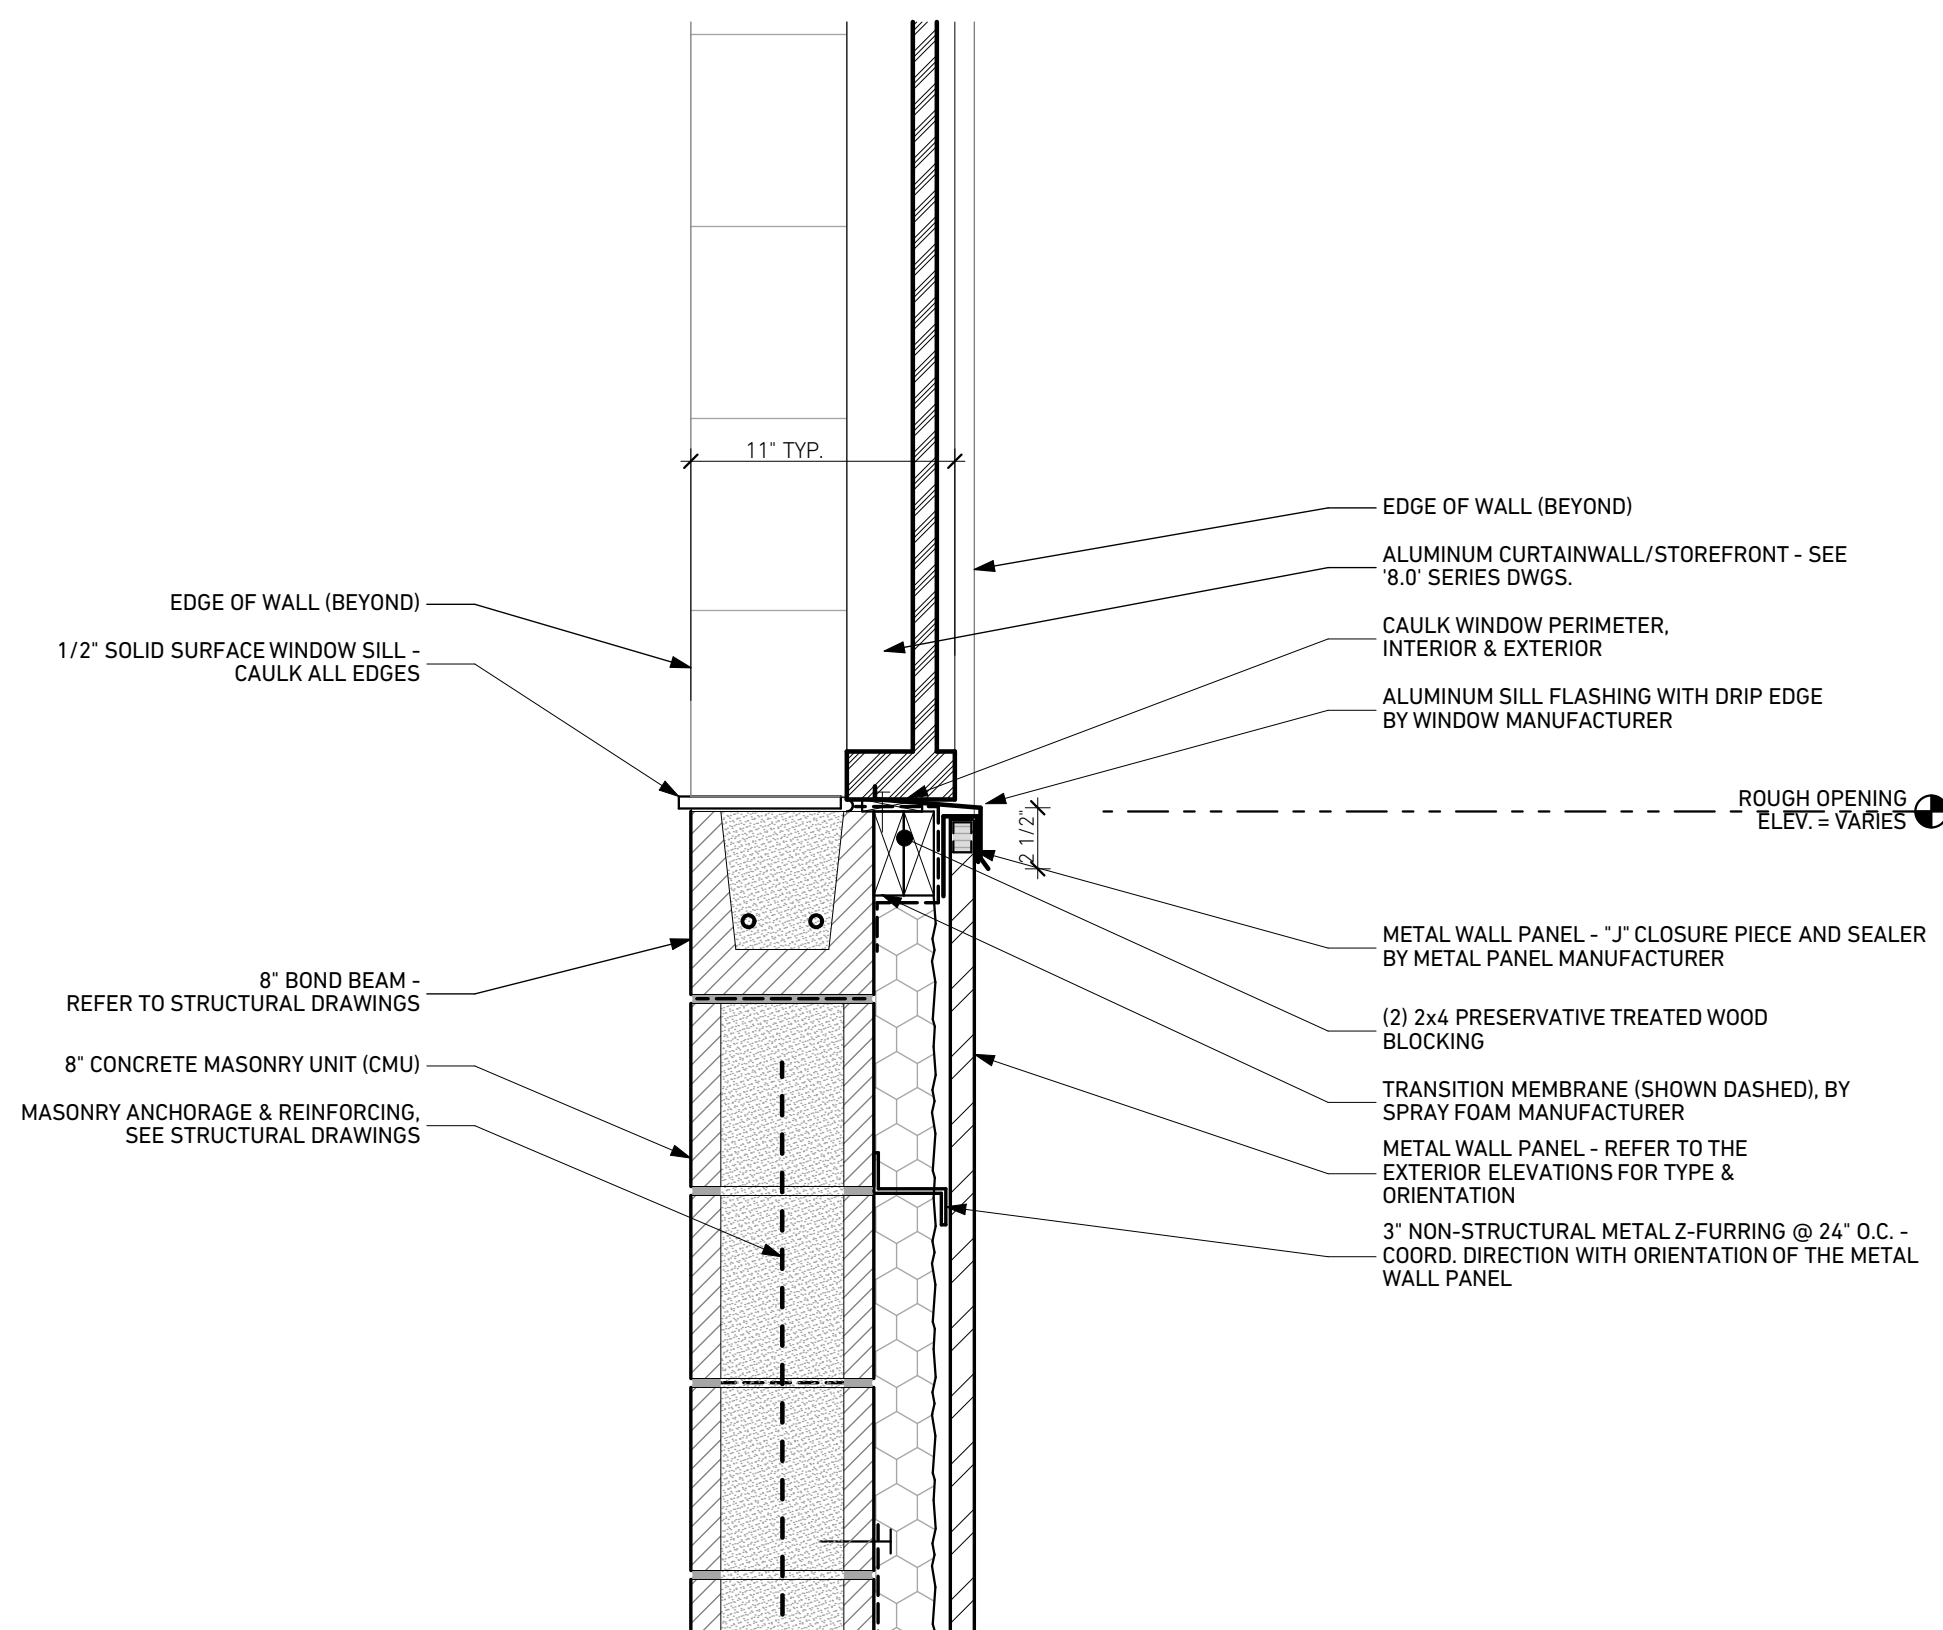

A4 TYPICAL 8" CMU WALL WITH METAL PANEL [ALUM. STOREFRONT SILL]

SCALE: 1 1/2" = 1'-0"

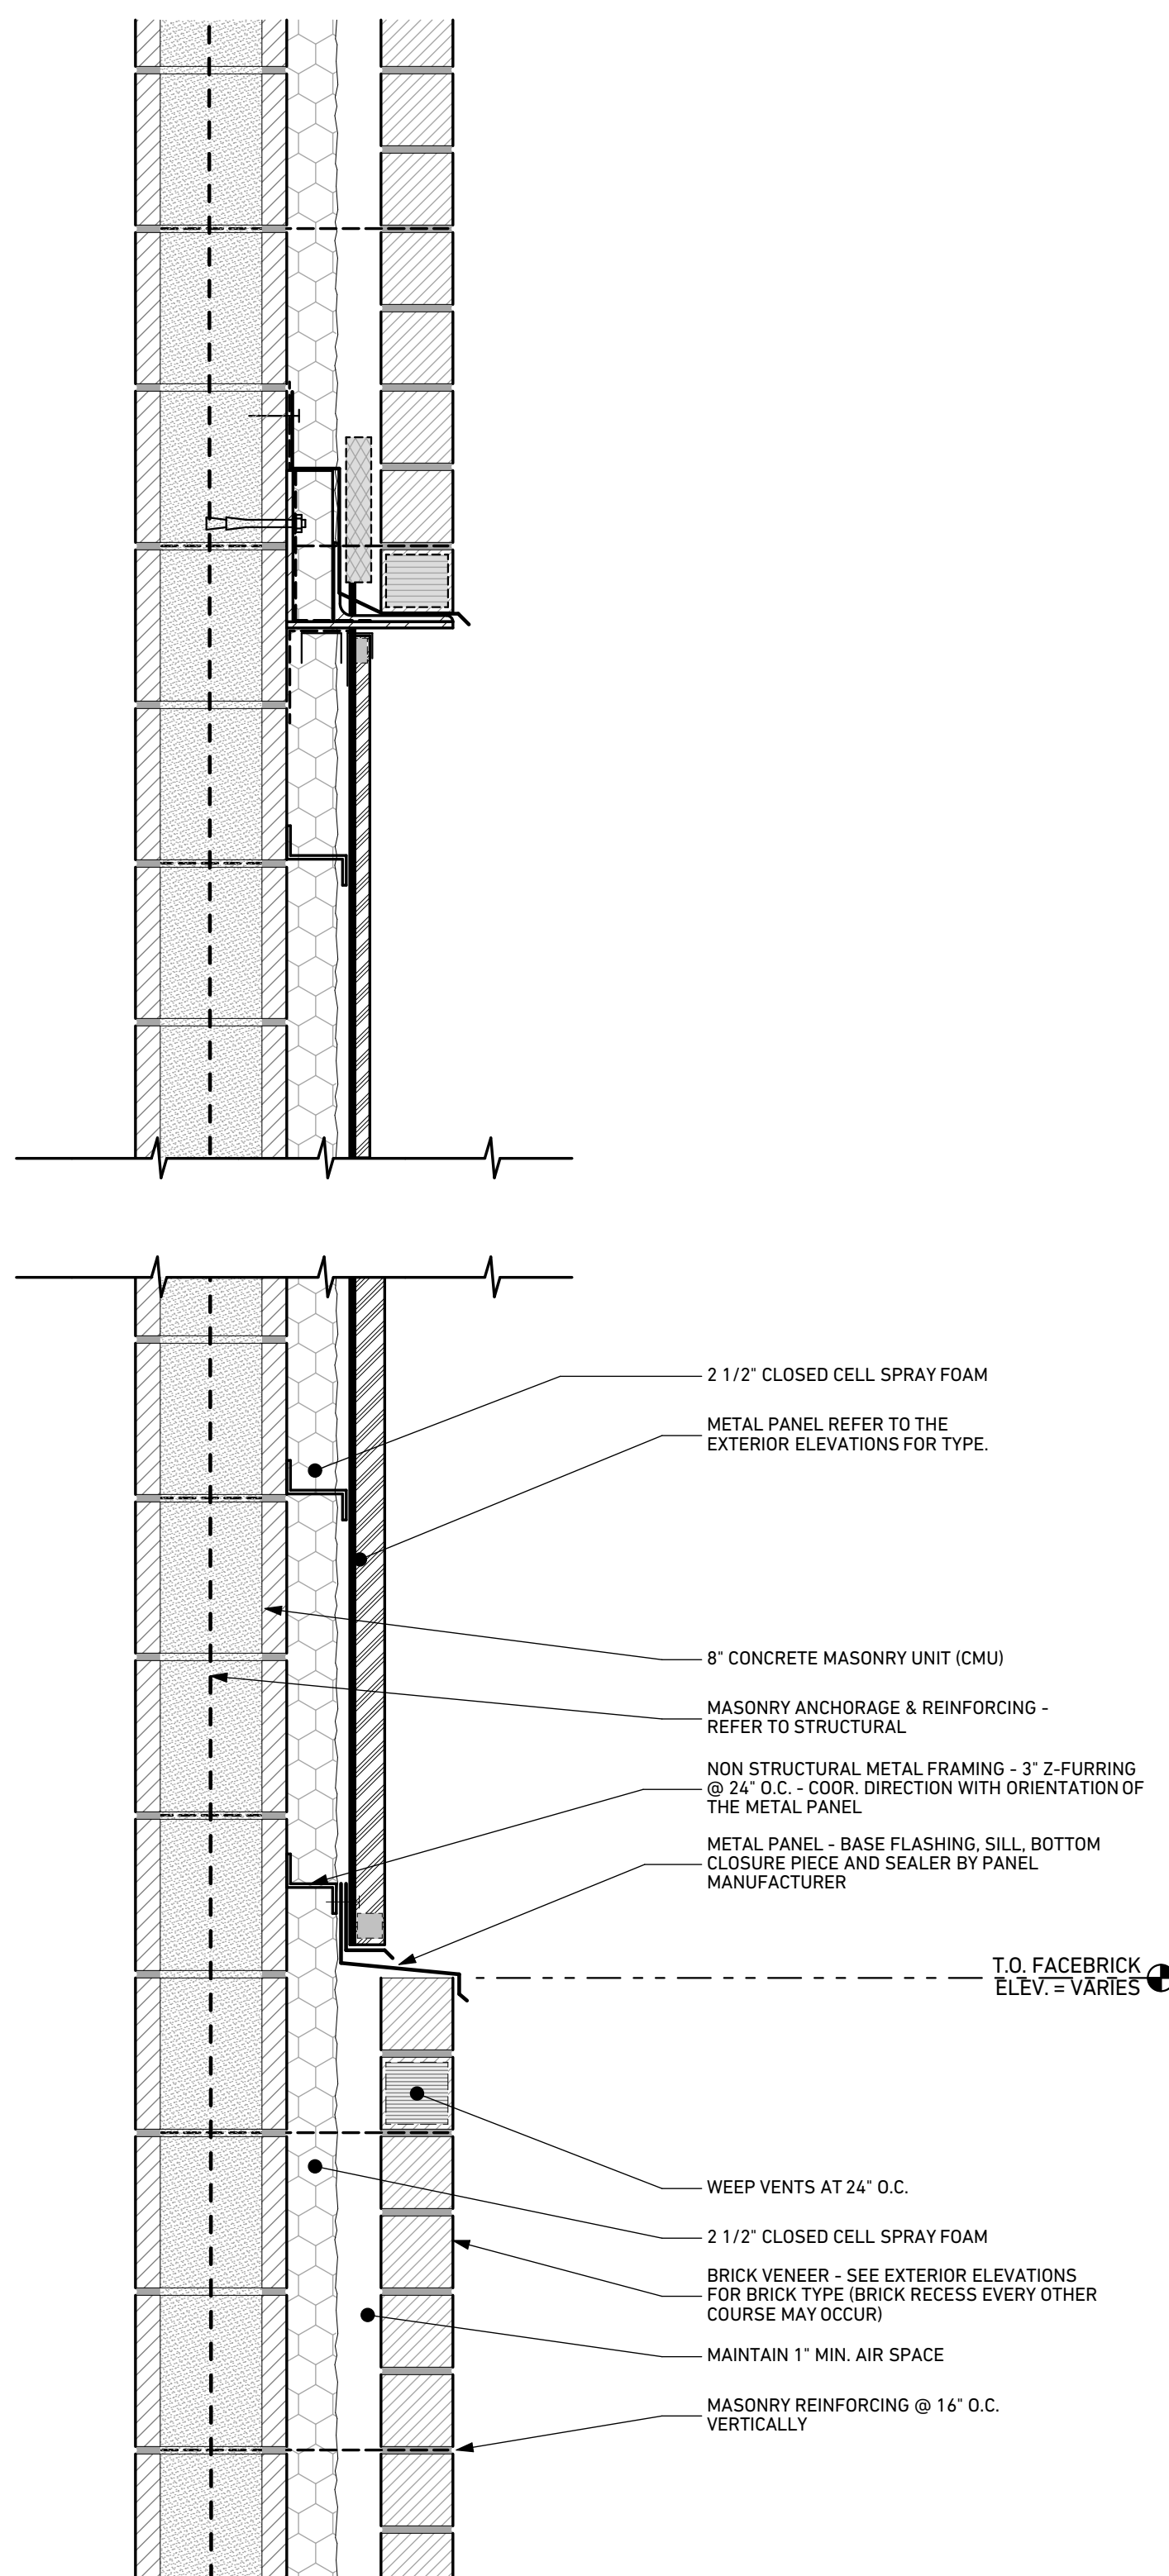

A2 TYPICAL 8" CMU WITH MASONRY / METAL PANEL TRANSITION

SCALE: 1 1/2" = 1'-0"

NORTH CANTON MIDDLE SCHOOL

495 7th Street NE
North Canton, OH 44720

PROJECT No. 23.095

100% CONSTRUCTION DOCUMENTS:
06/06/2025

DRAWING UPDATES 6/10/2025

TYPICAL WALL SECTIONS AND DETAILS

07-004