




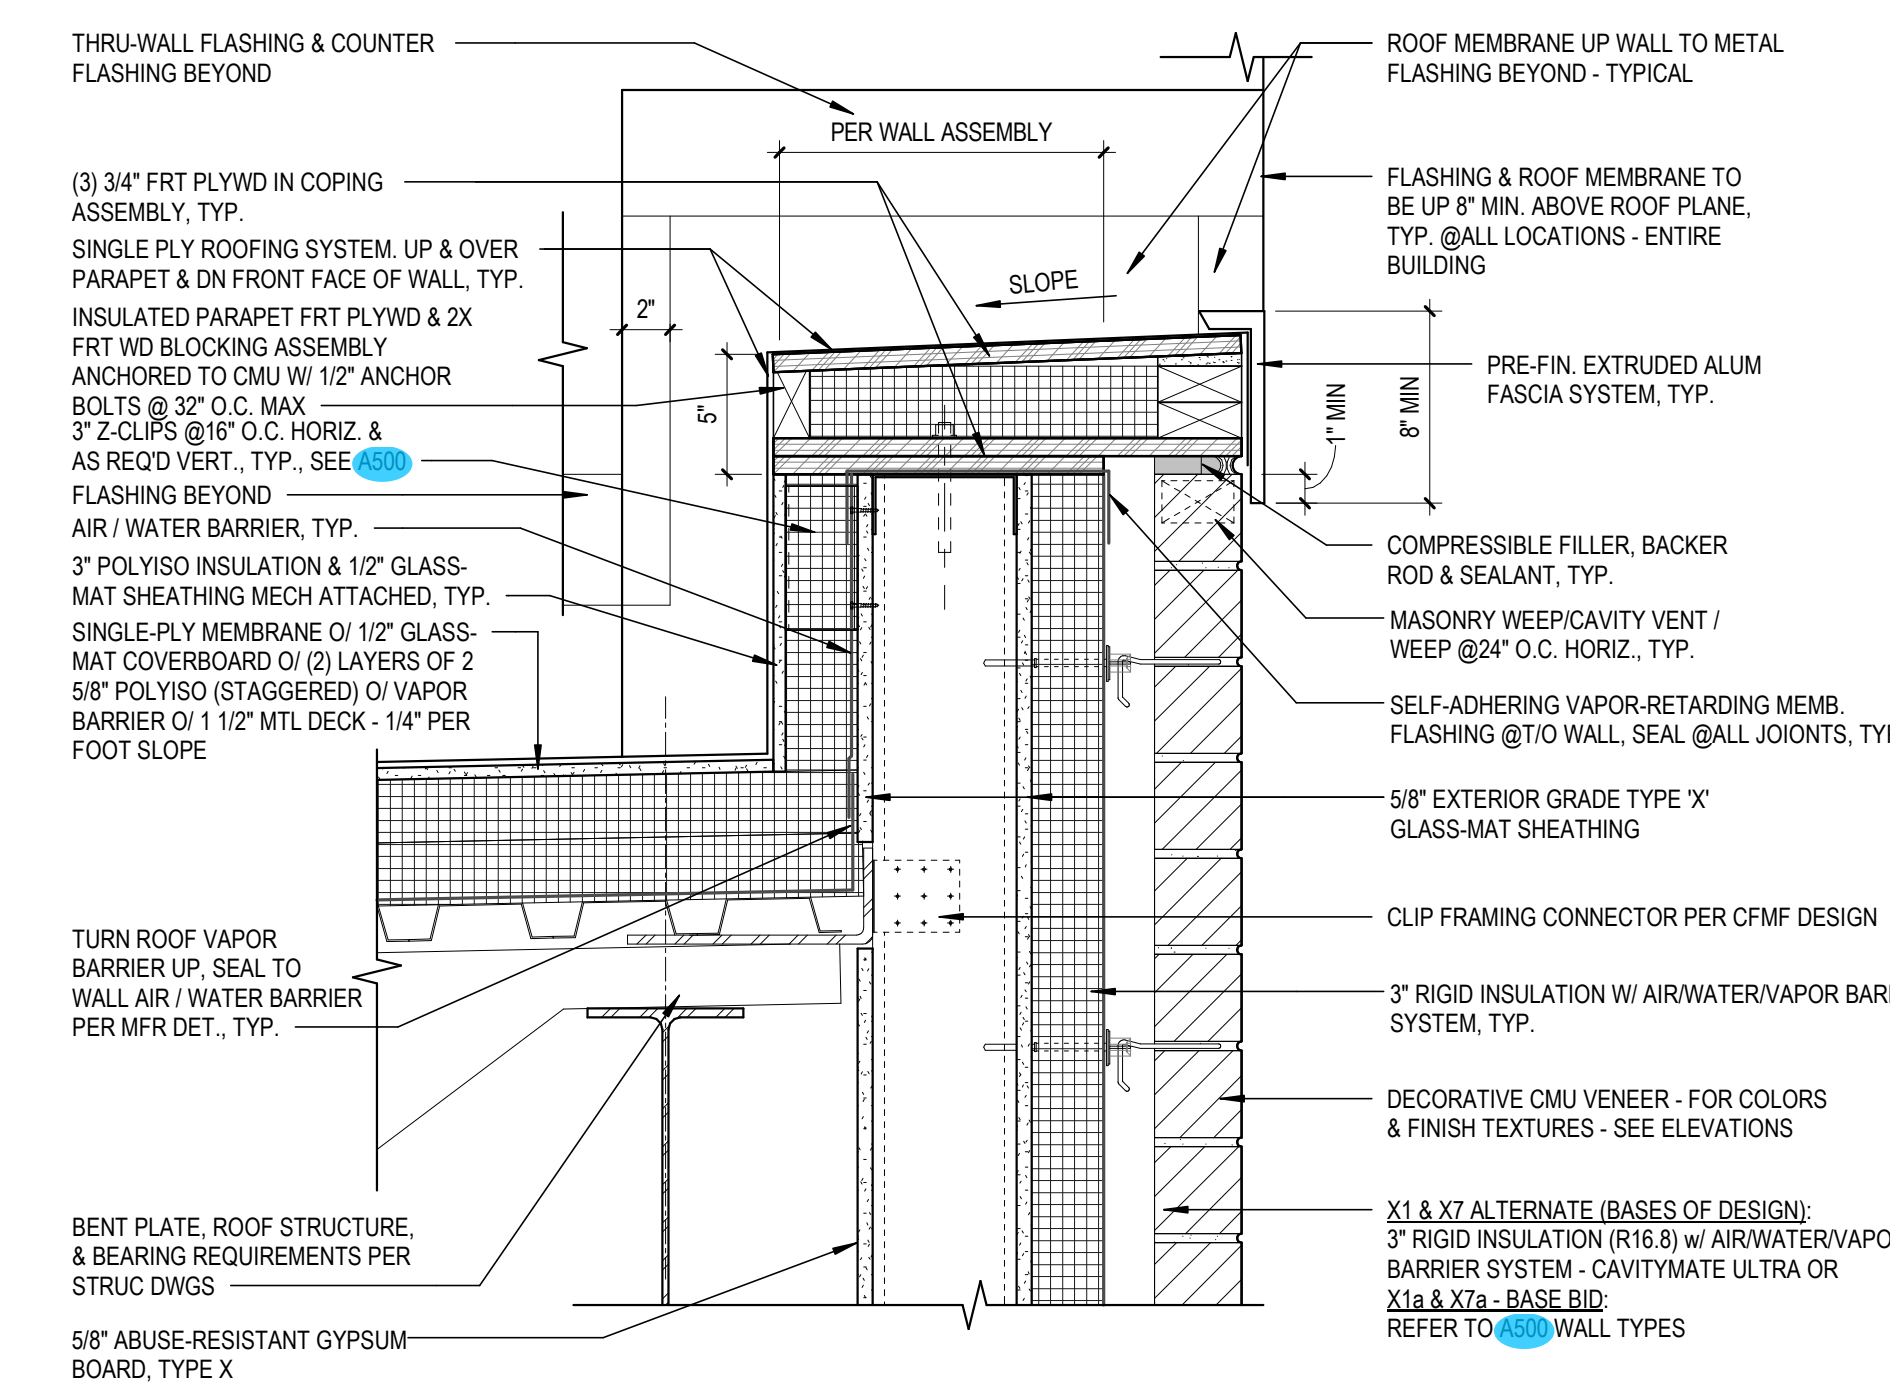


1 TYPICAL COPING DETAIL - BRICK VENEER / CFM
SCALE: 1 1/2" = 1'-0" REF. FROM: 5 / A540

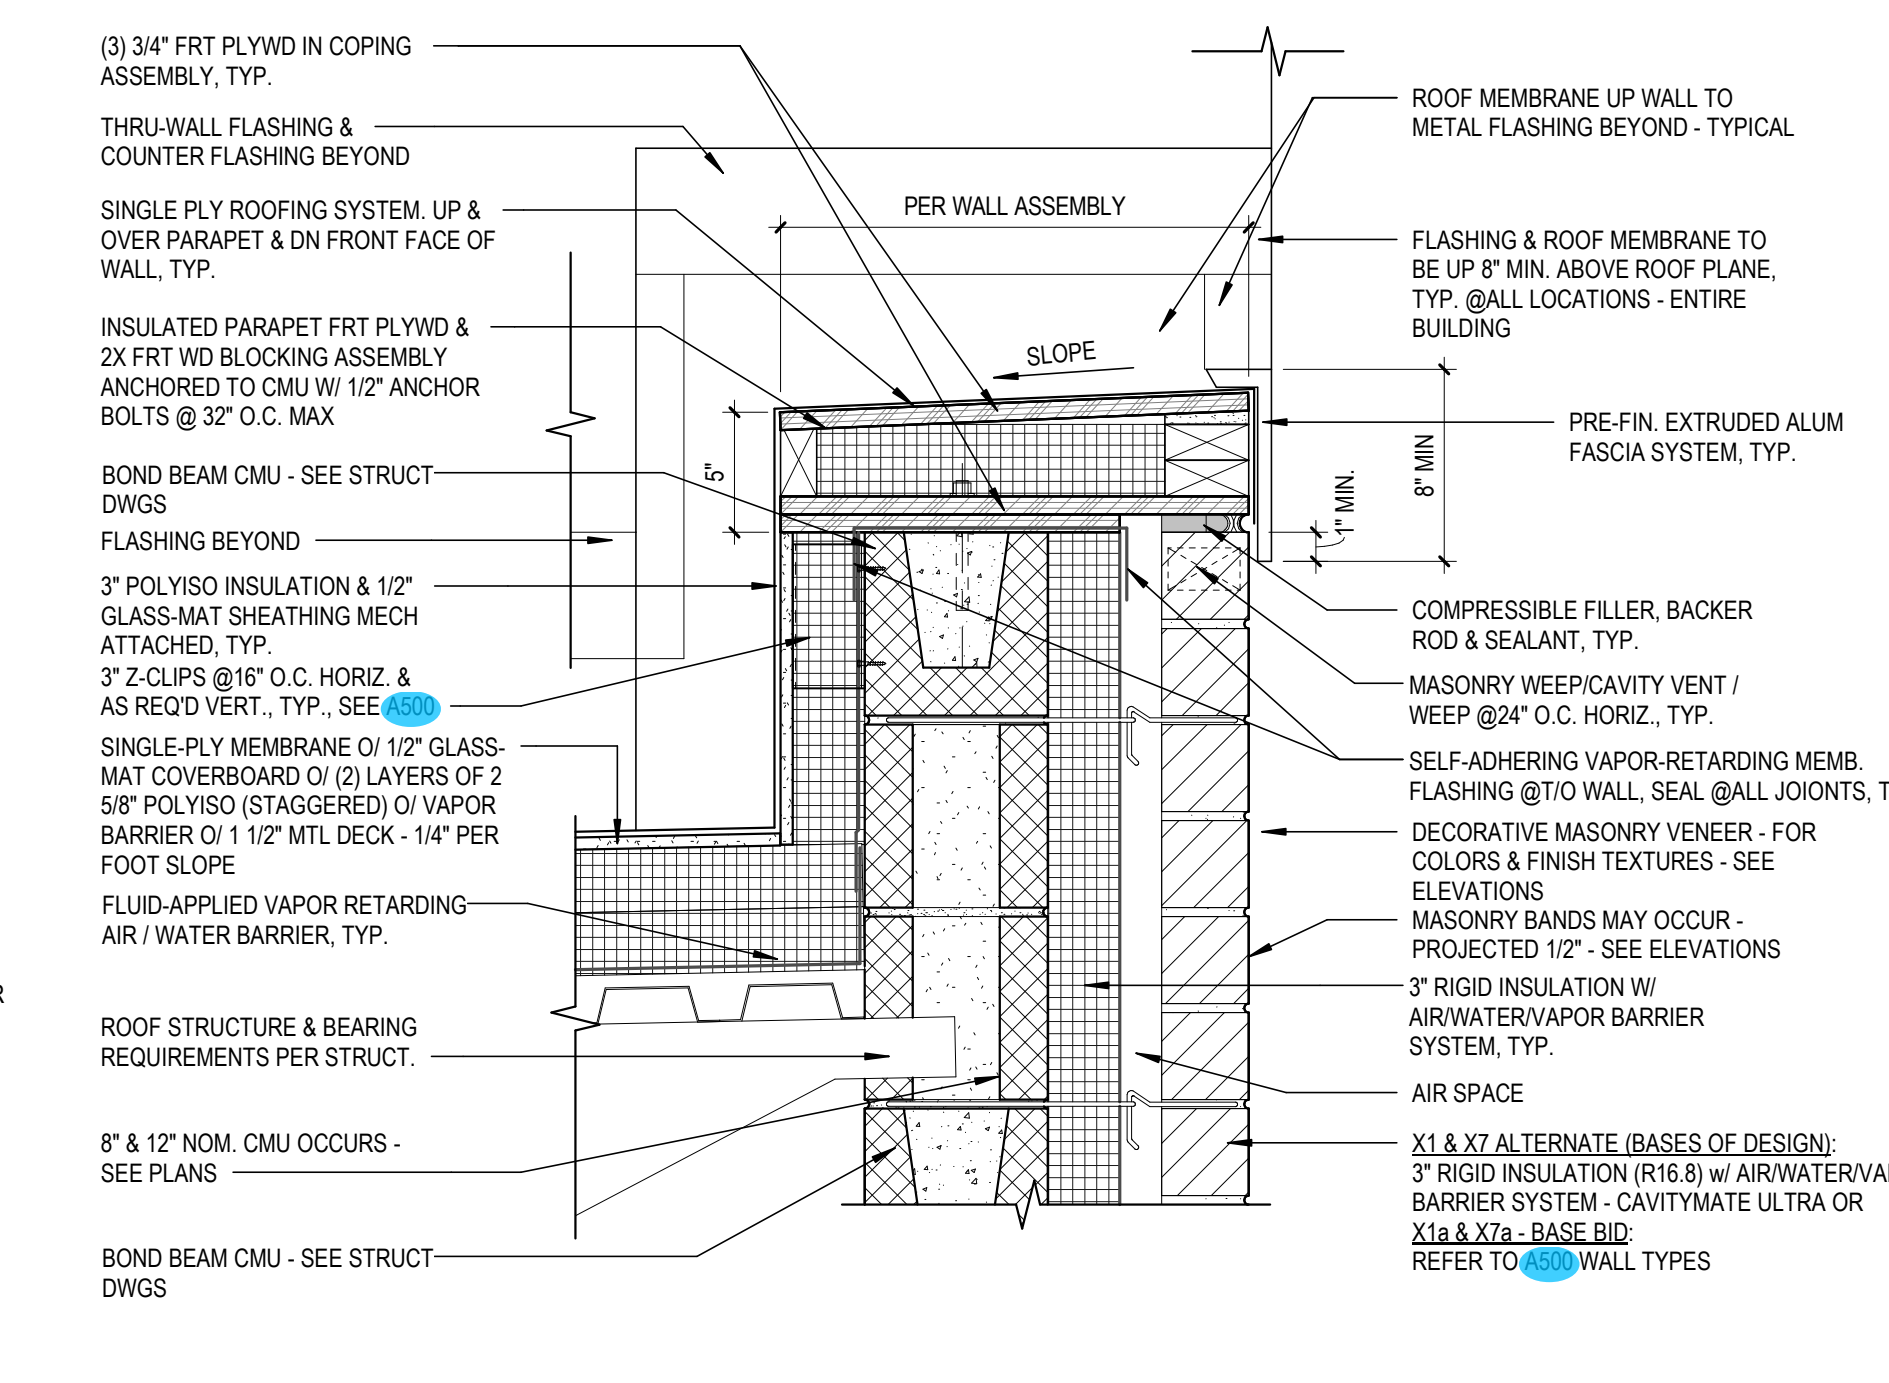


2 TYPICAL COPING DETAIL - BRICK VENEER / CMU
SCALE: 1 1/2" = 1'-0" REF. FROM: 5 / A510

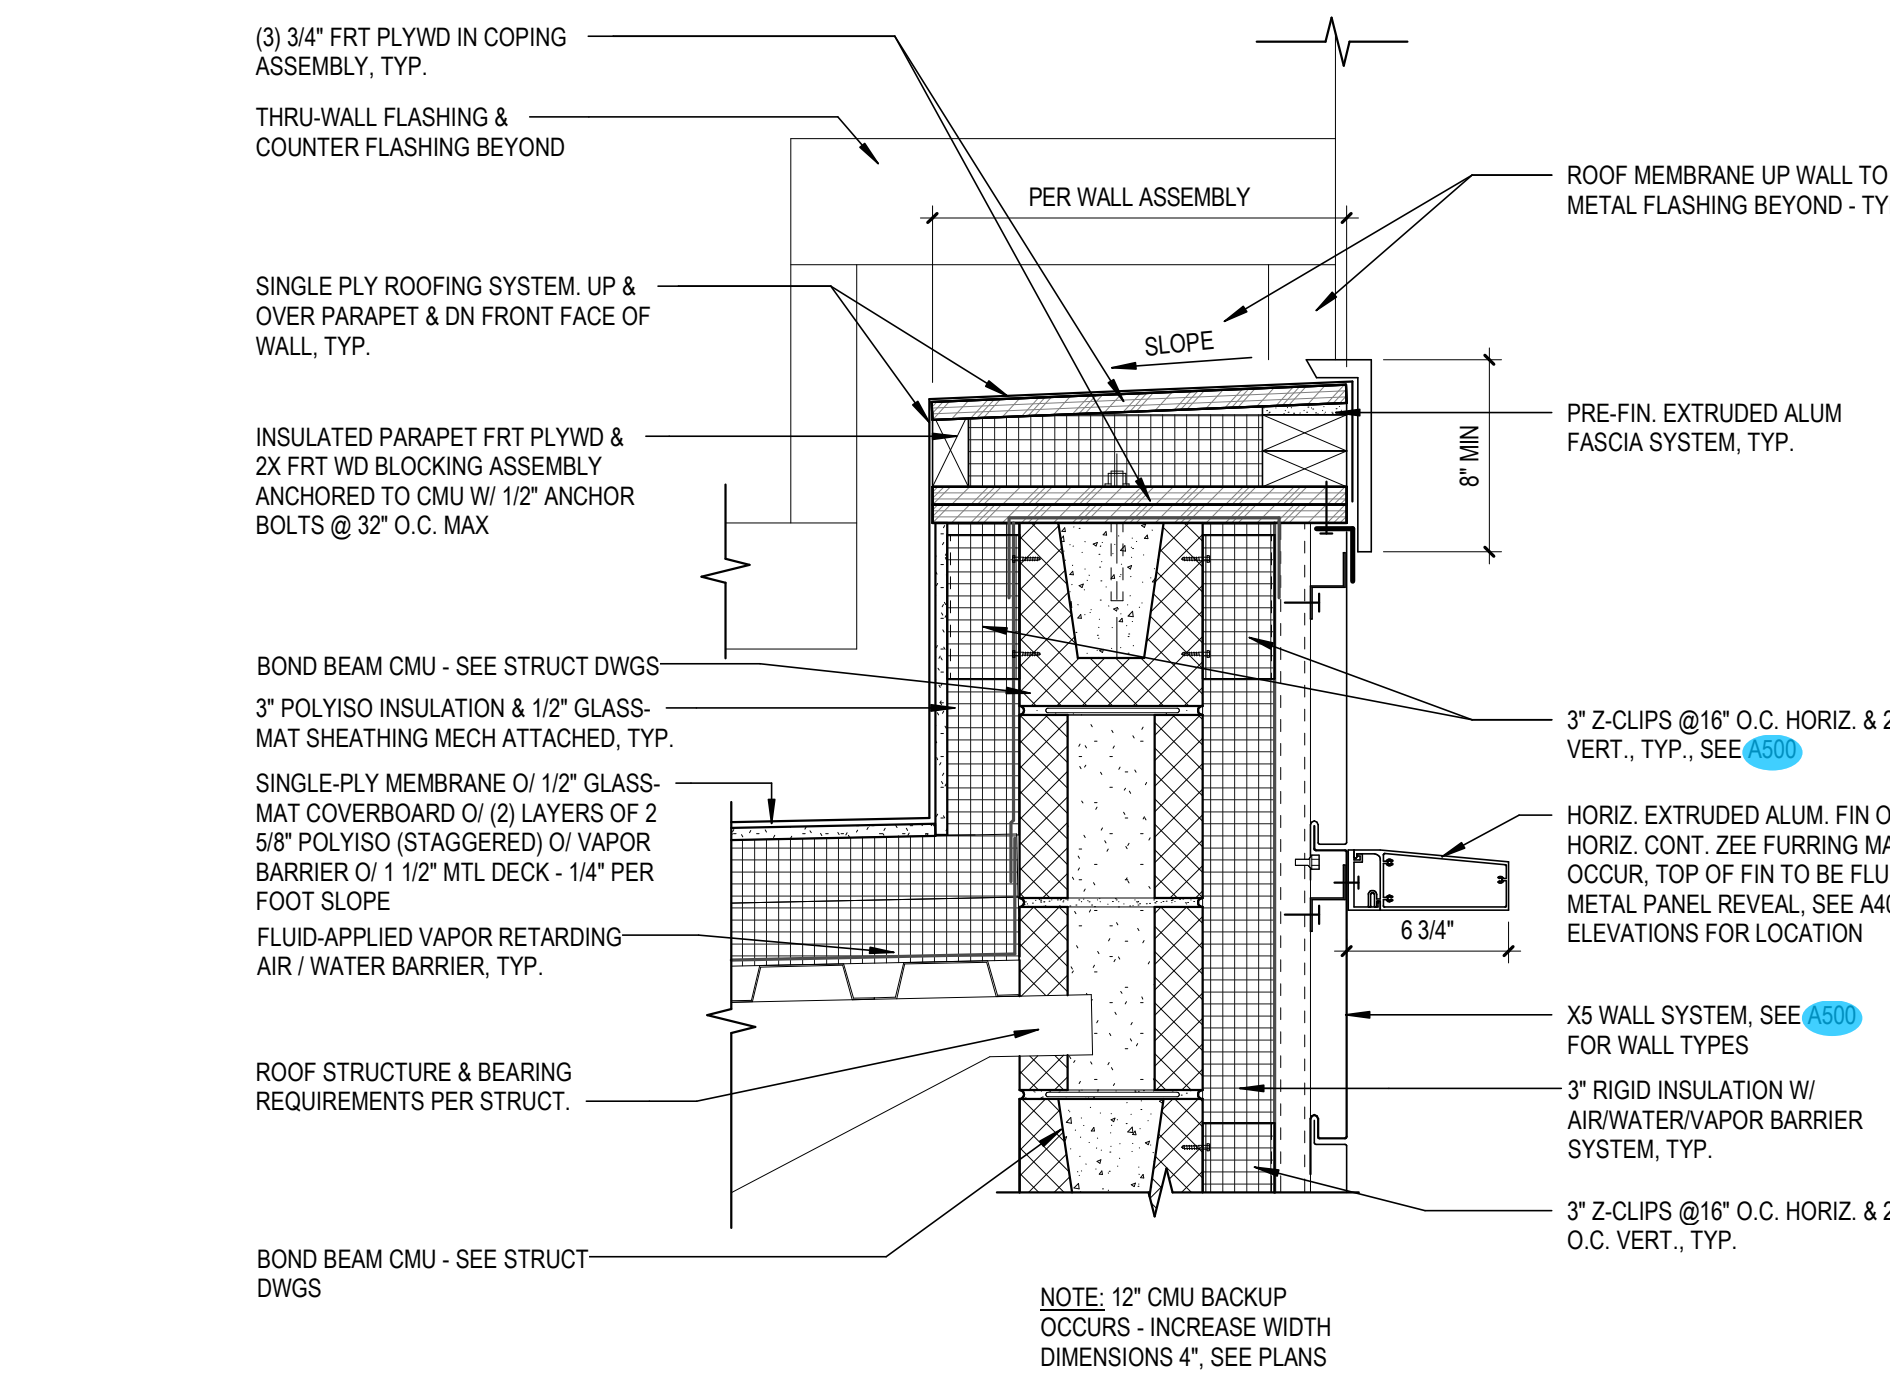


3 TYPICAL COPING DETAIL - RAINSCREEN / CMU
SCALE: 1 1/2" = 1'-0" REF. FROM: 1 / A521

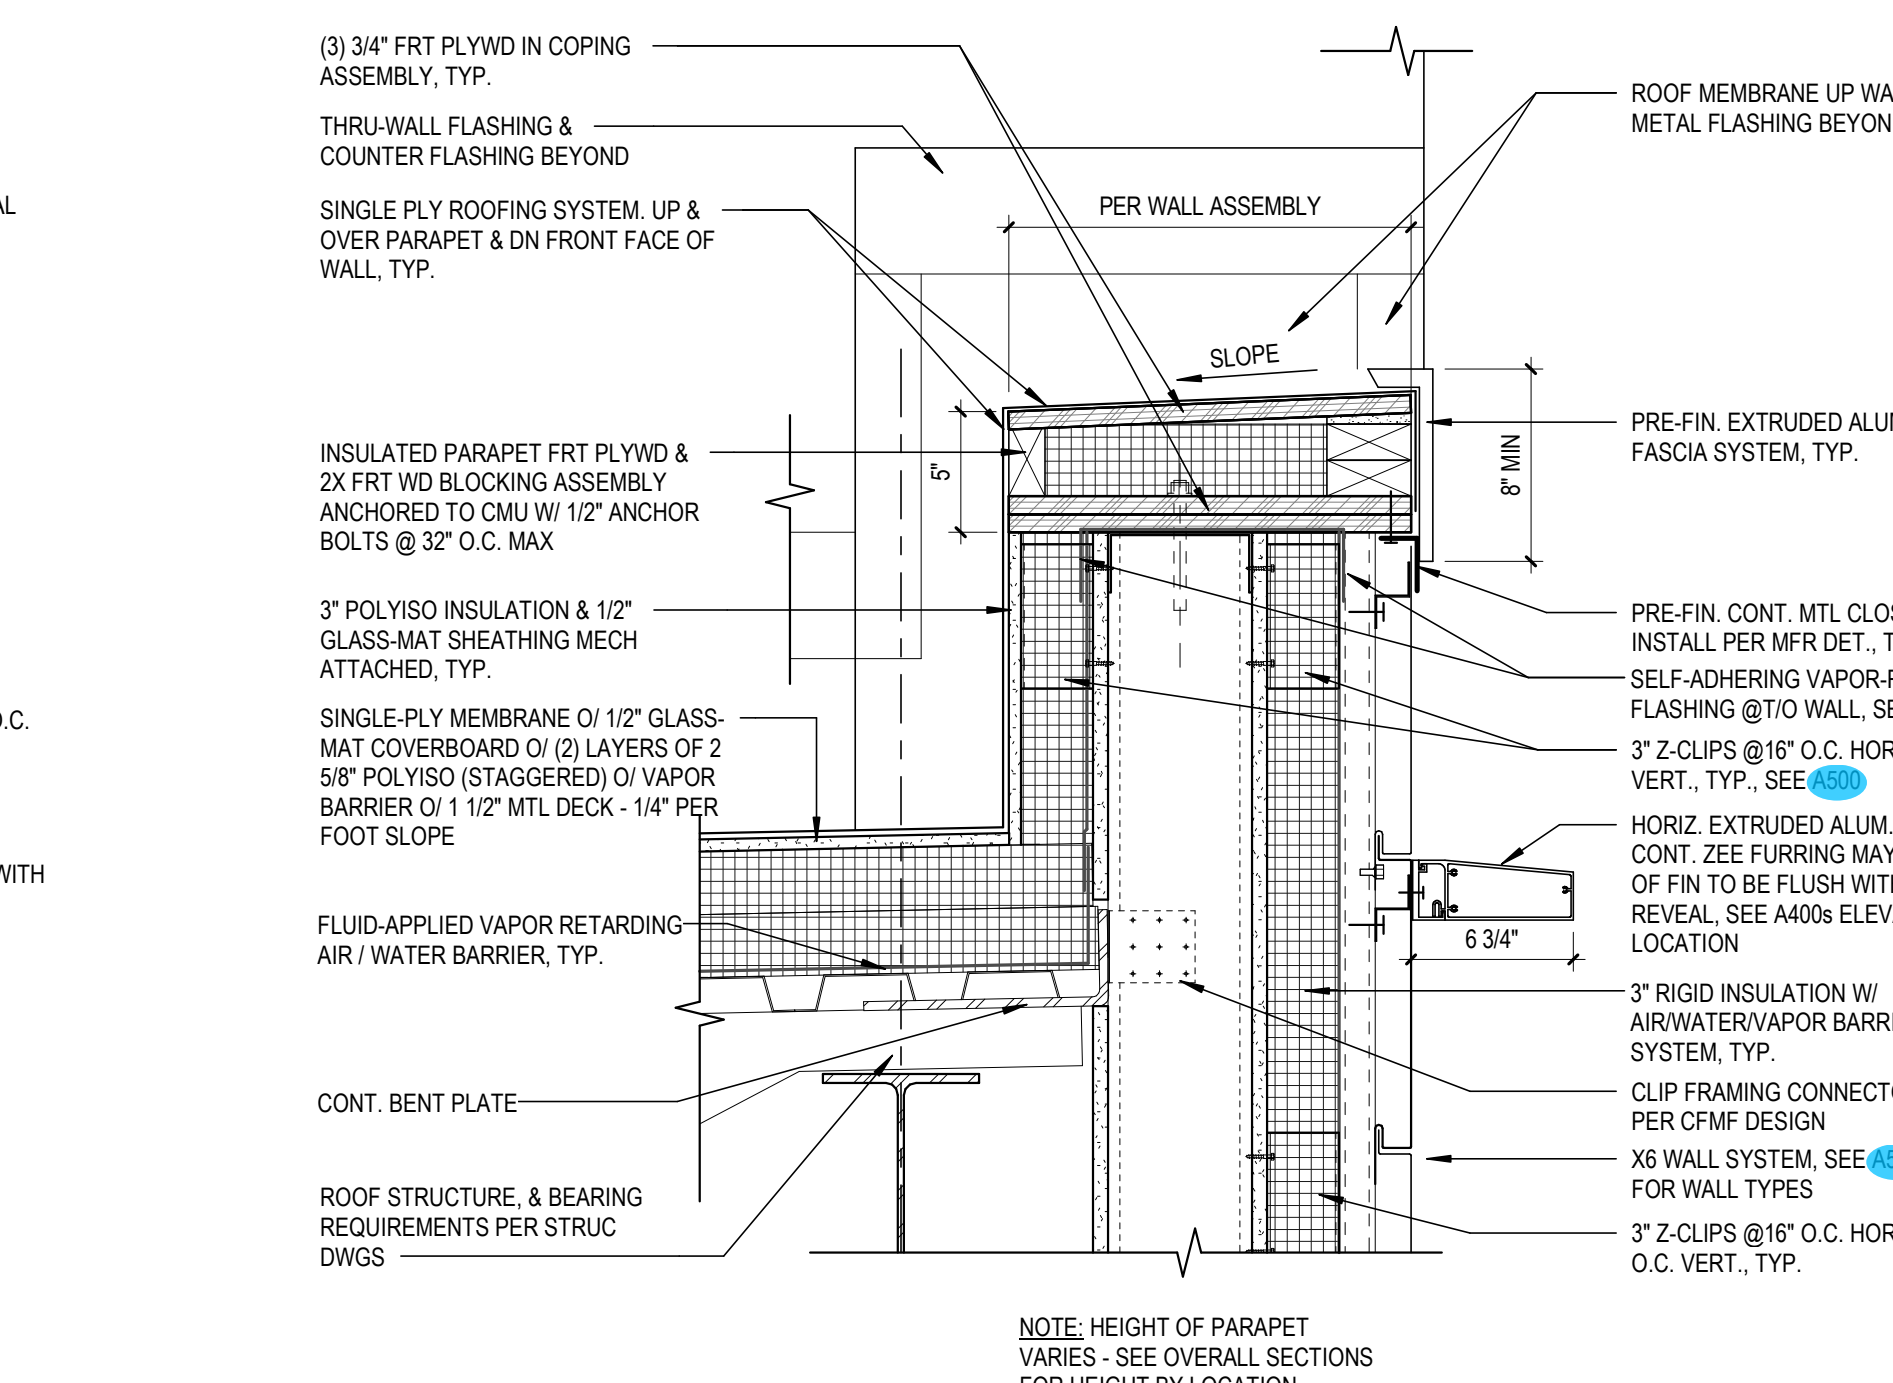


4 TYPICAL COPING DETAIL - RAINSCREEN / CFM
SCALE: 1 1/2" = 1'-0" REF. FROM: 4 / A521

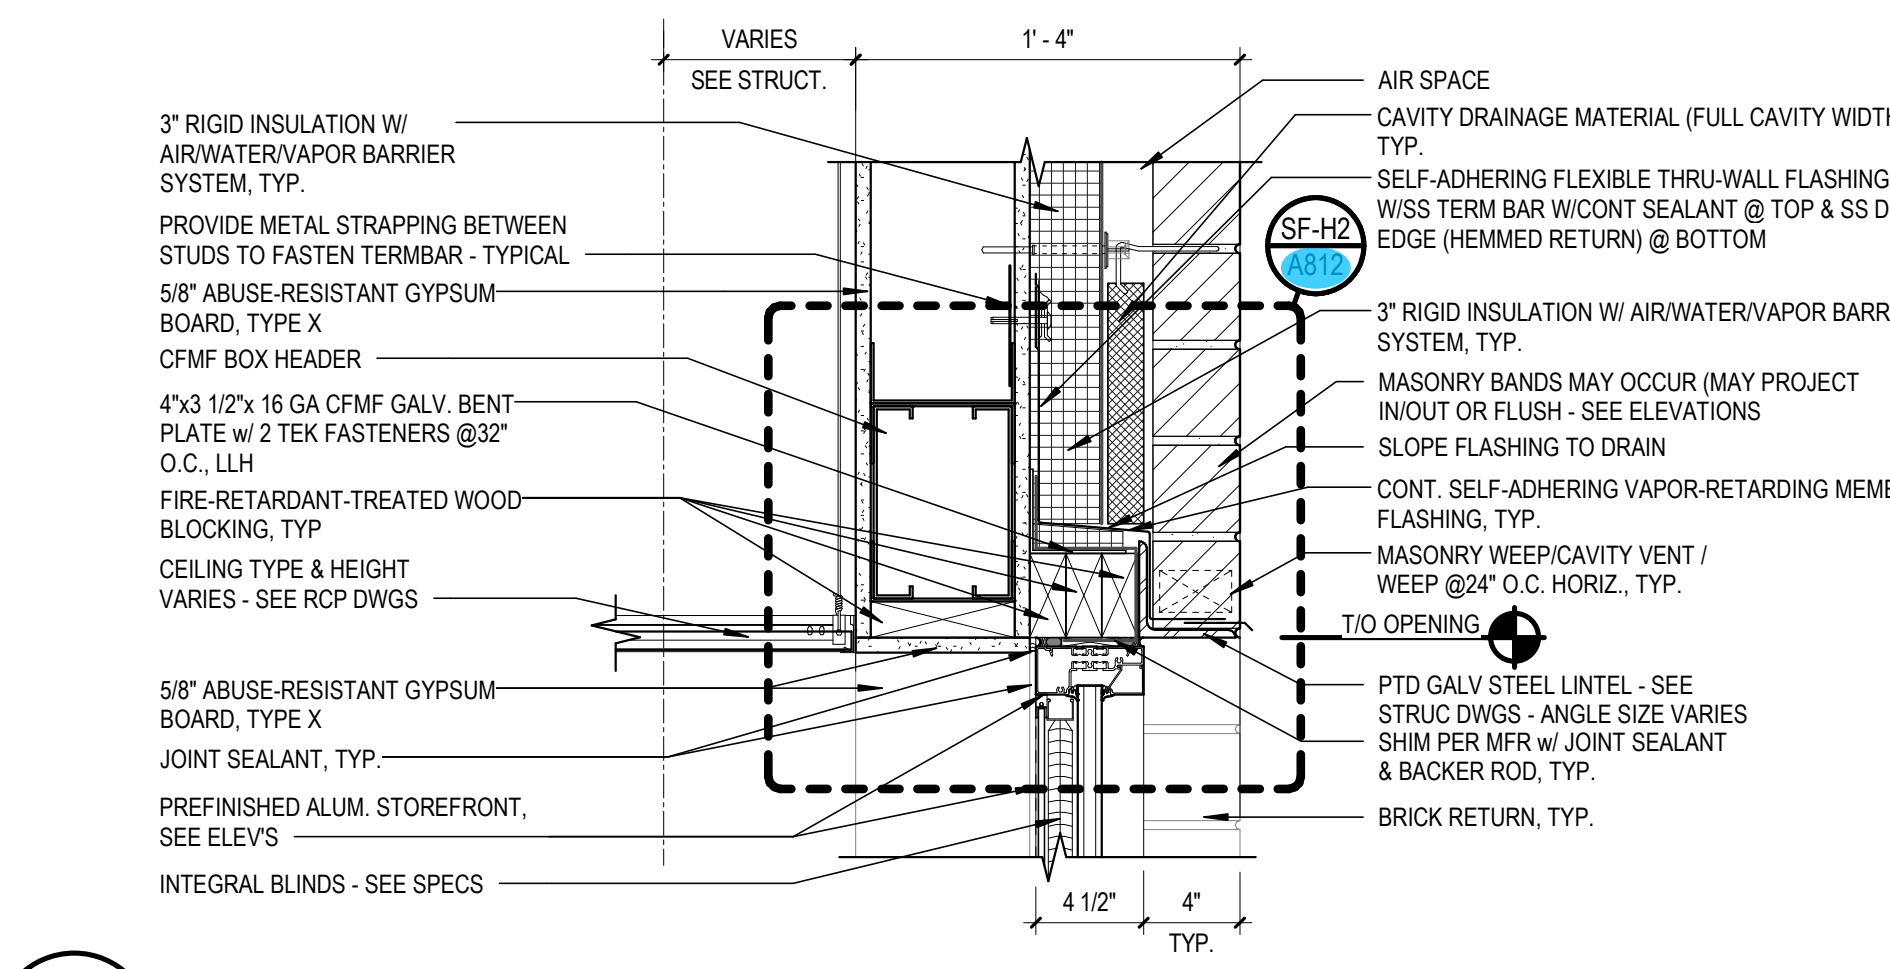


5 TYPICAL DETAIL
SCALE: 1 1/2" = 1'-0" REF. FROM: 7 / A540

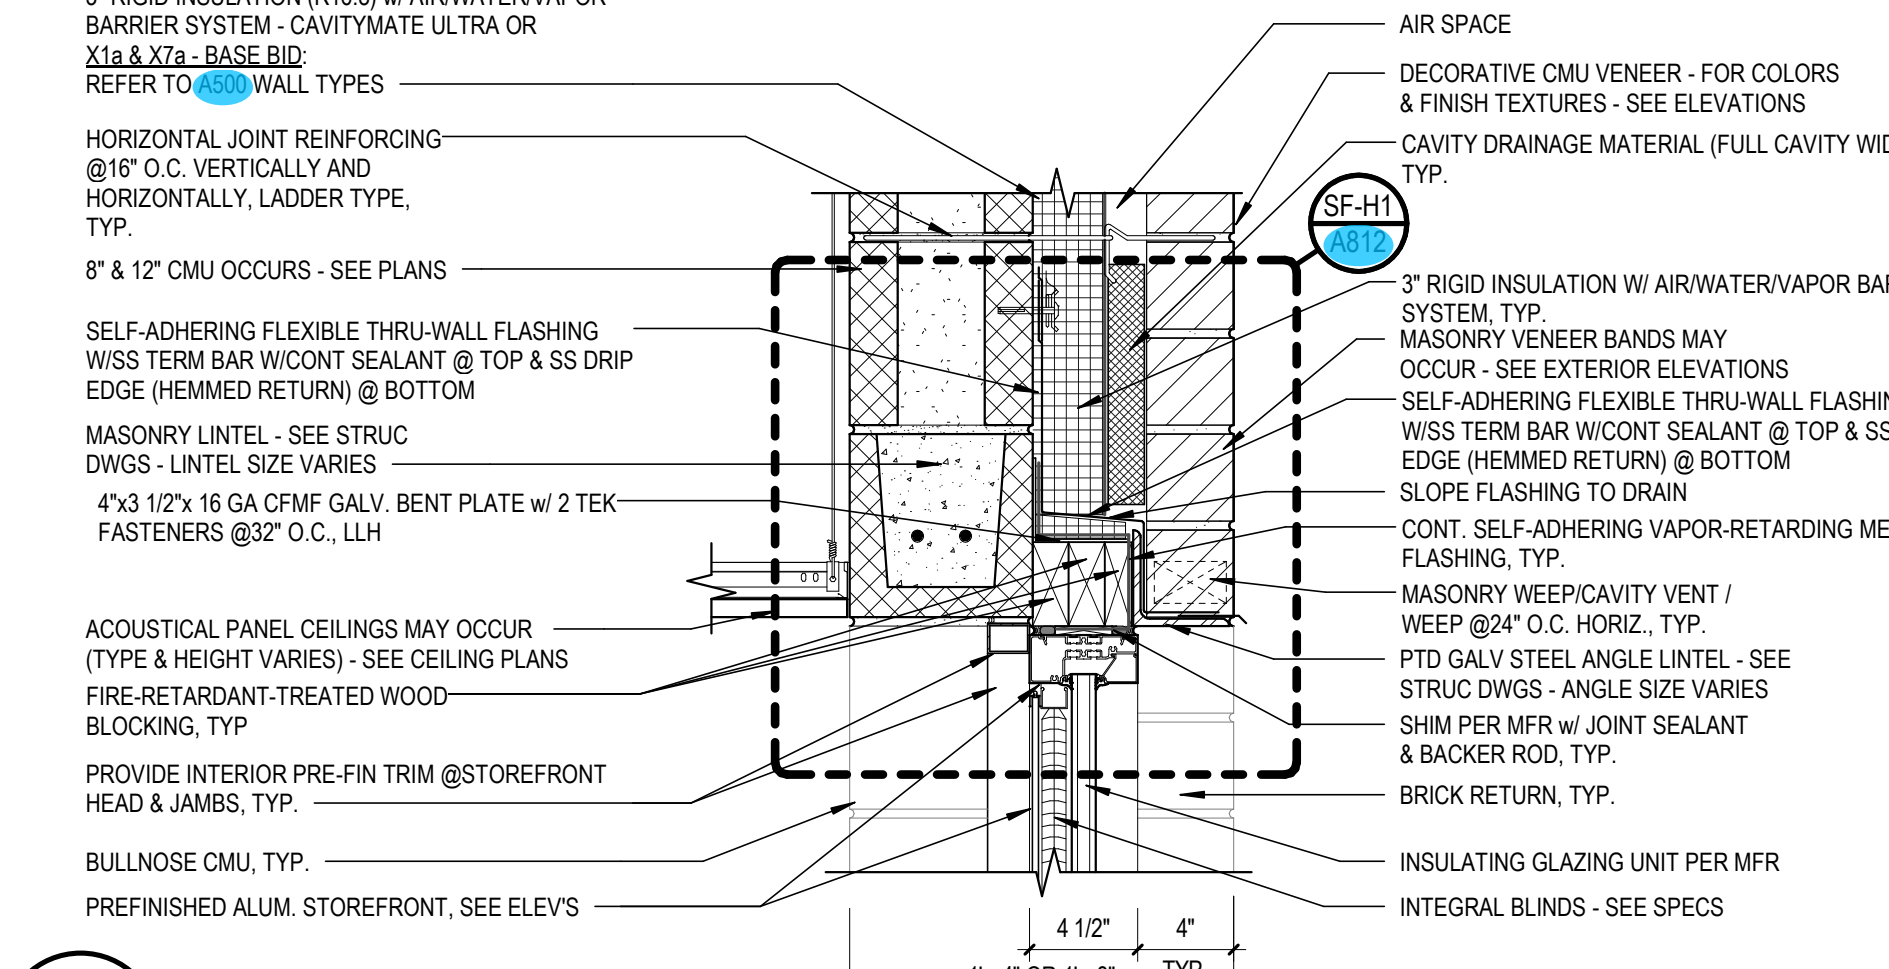


6 TYPICAL DETAIL
SCALE: 1 1/2" = 1'-0" REF. FROM: 1 / A512

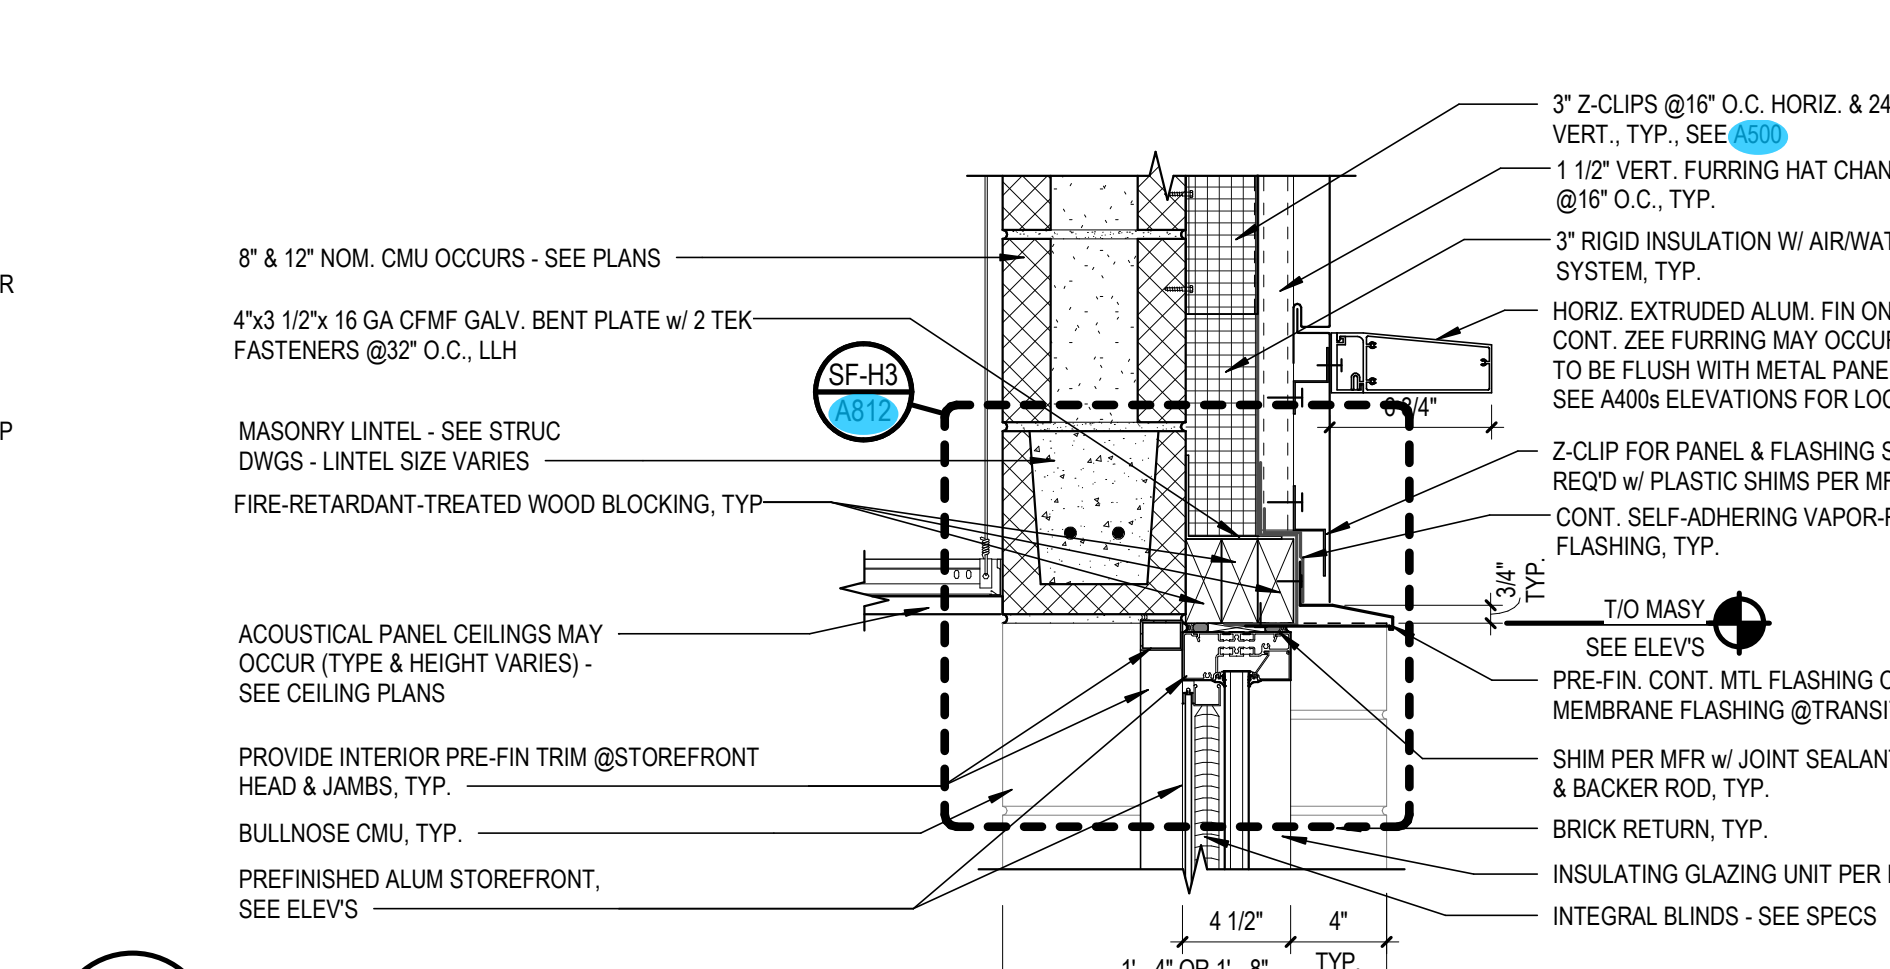


7 TYPICAL DETAIL
SCALE: 1 1/2" = 1'-0" REF. FROM: 1 / A521

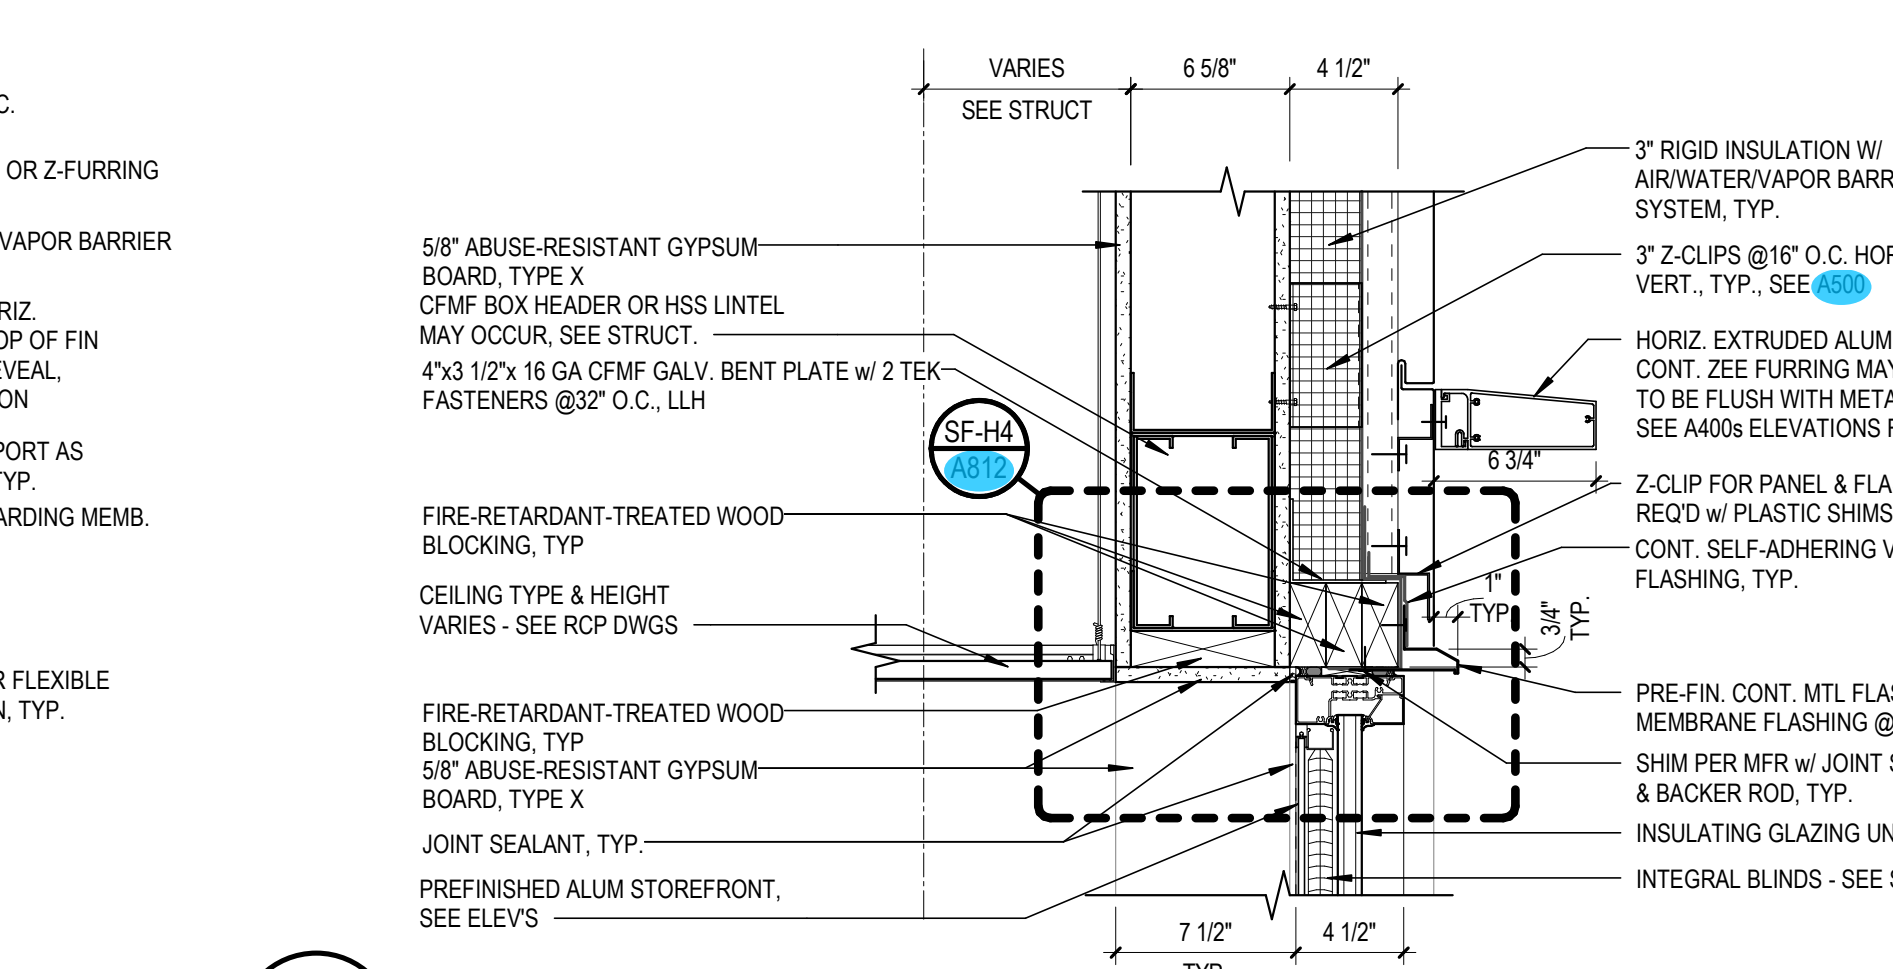


8 TYPICAL DETAIL
SCALE: 1 1/2" = 1'-0" REF. FROM: 4 / A521

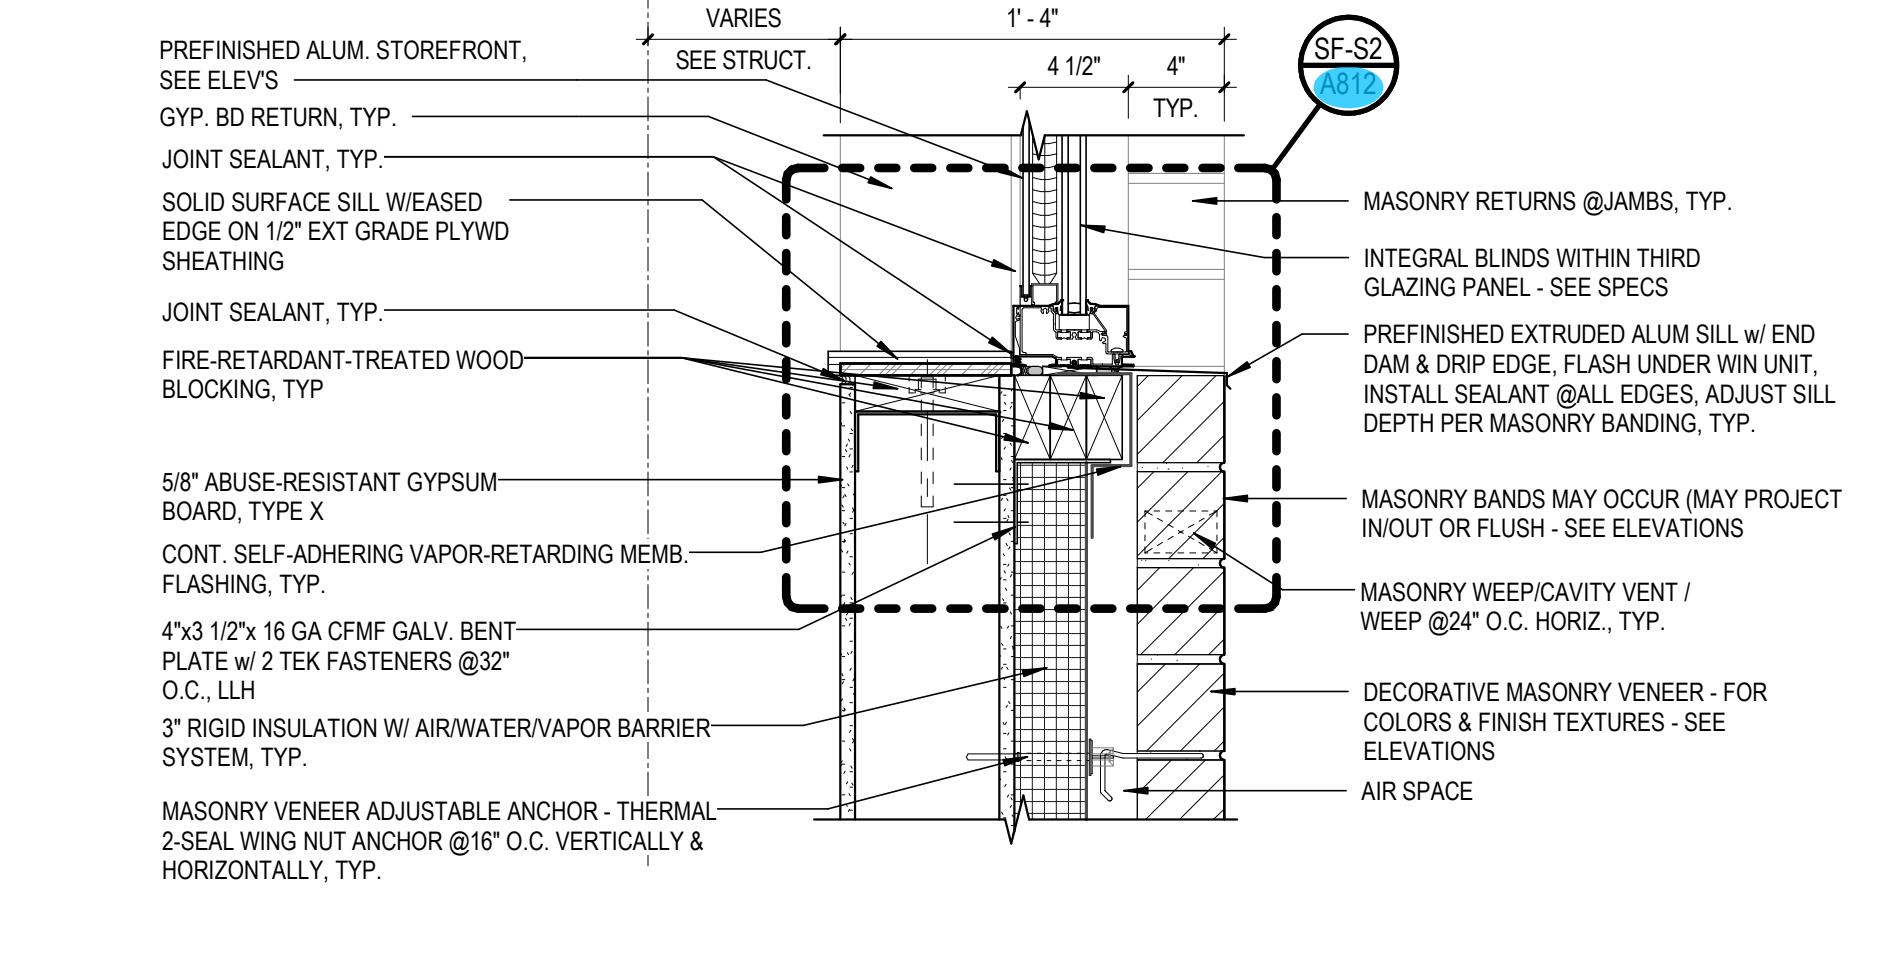


9 TYPICAL DETAIL
SCALE: 1 1/2" = 1'-0" REF. FROM: 7 / A540

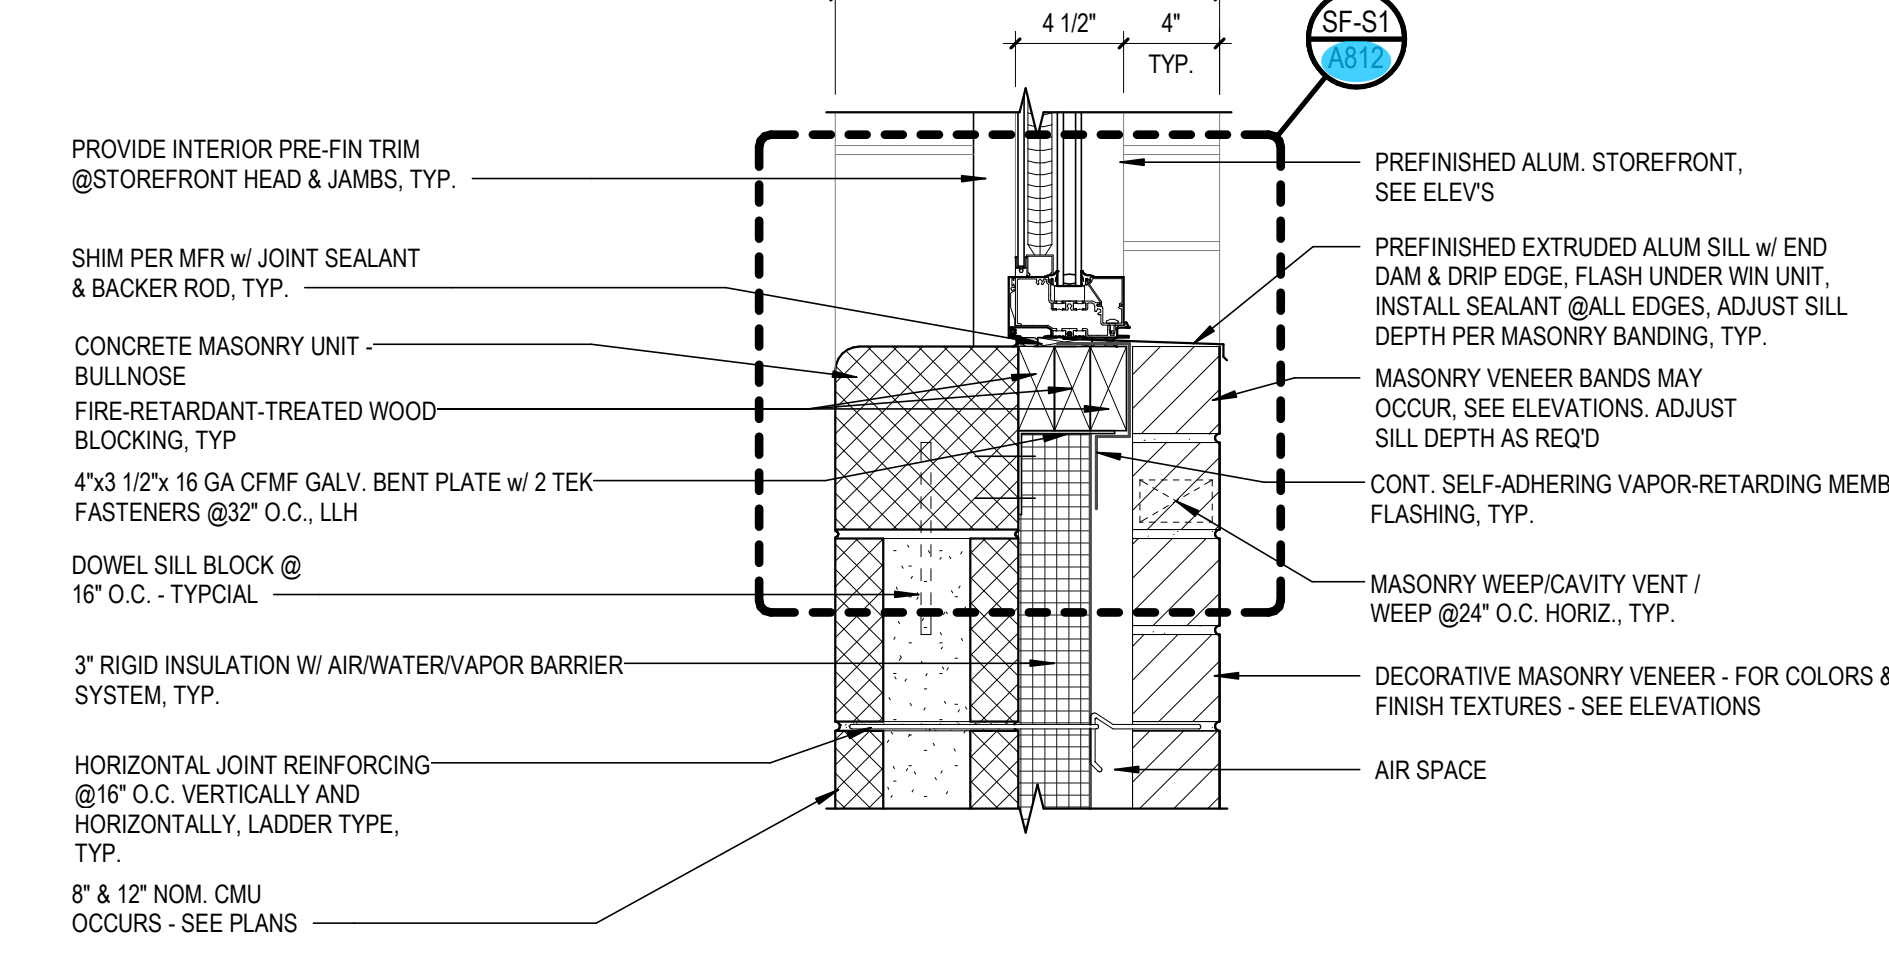


10 TYPICAL DETAIL
SCALE: 1 1/2" = 1'-0" REF. FROM: 1 / A512

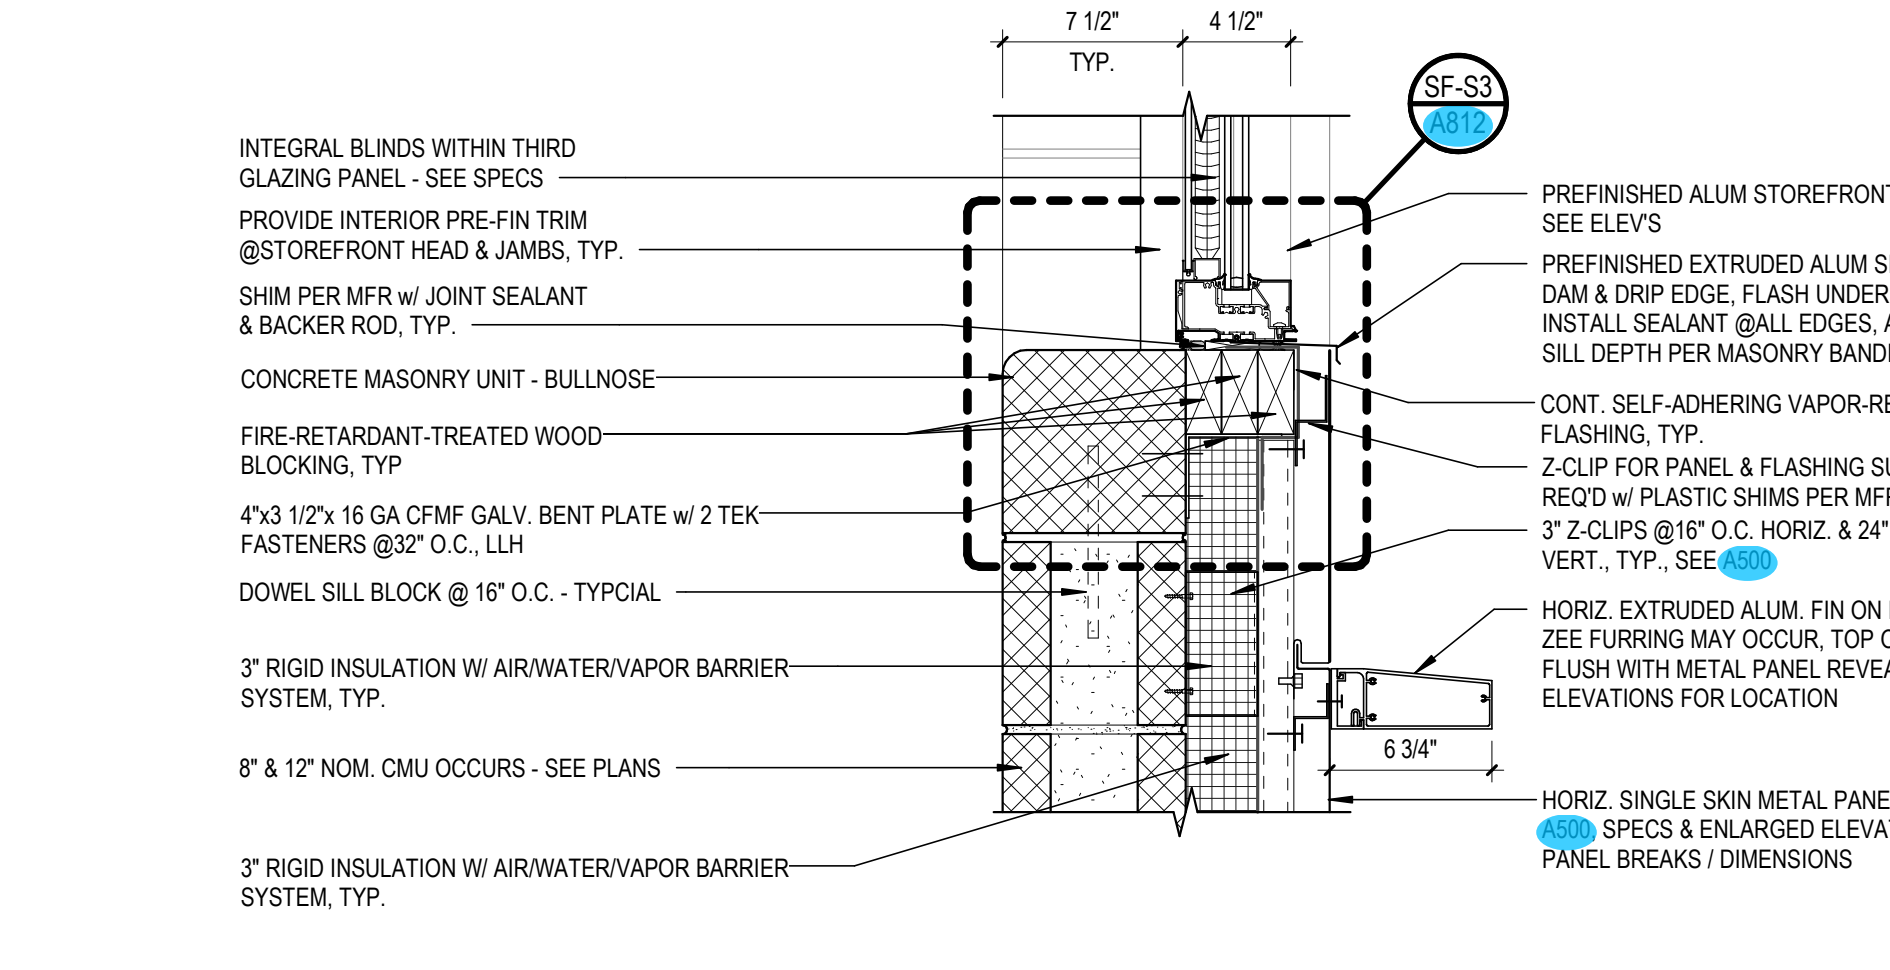


11 TYPICAL DETAIL
SCALE: 1 1/2" = 1'-0" REF. FROM: 1 / A521

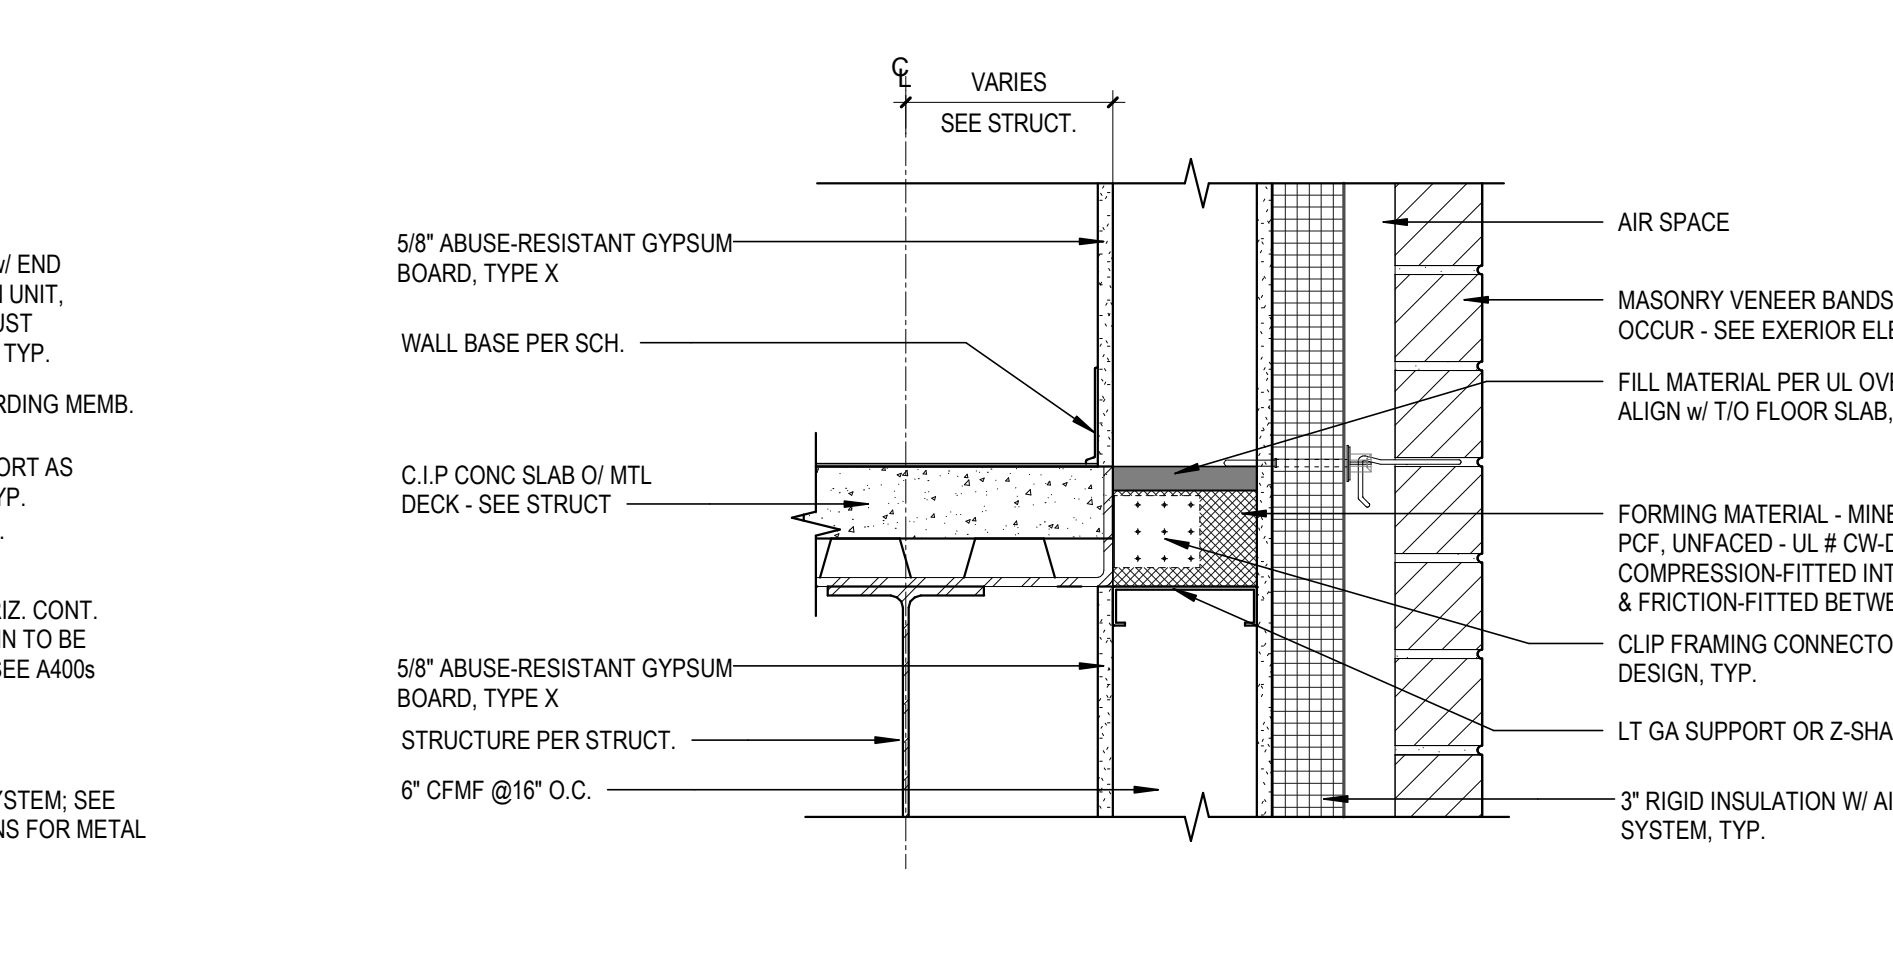


15 TYPICAL SAFB IN CFM PLENUM DETAIL
SCALE: 1 1/2" = 1'-0" REF. FROM: 5 / A540

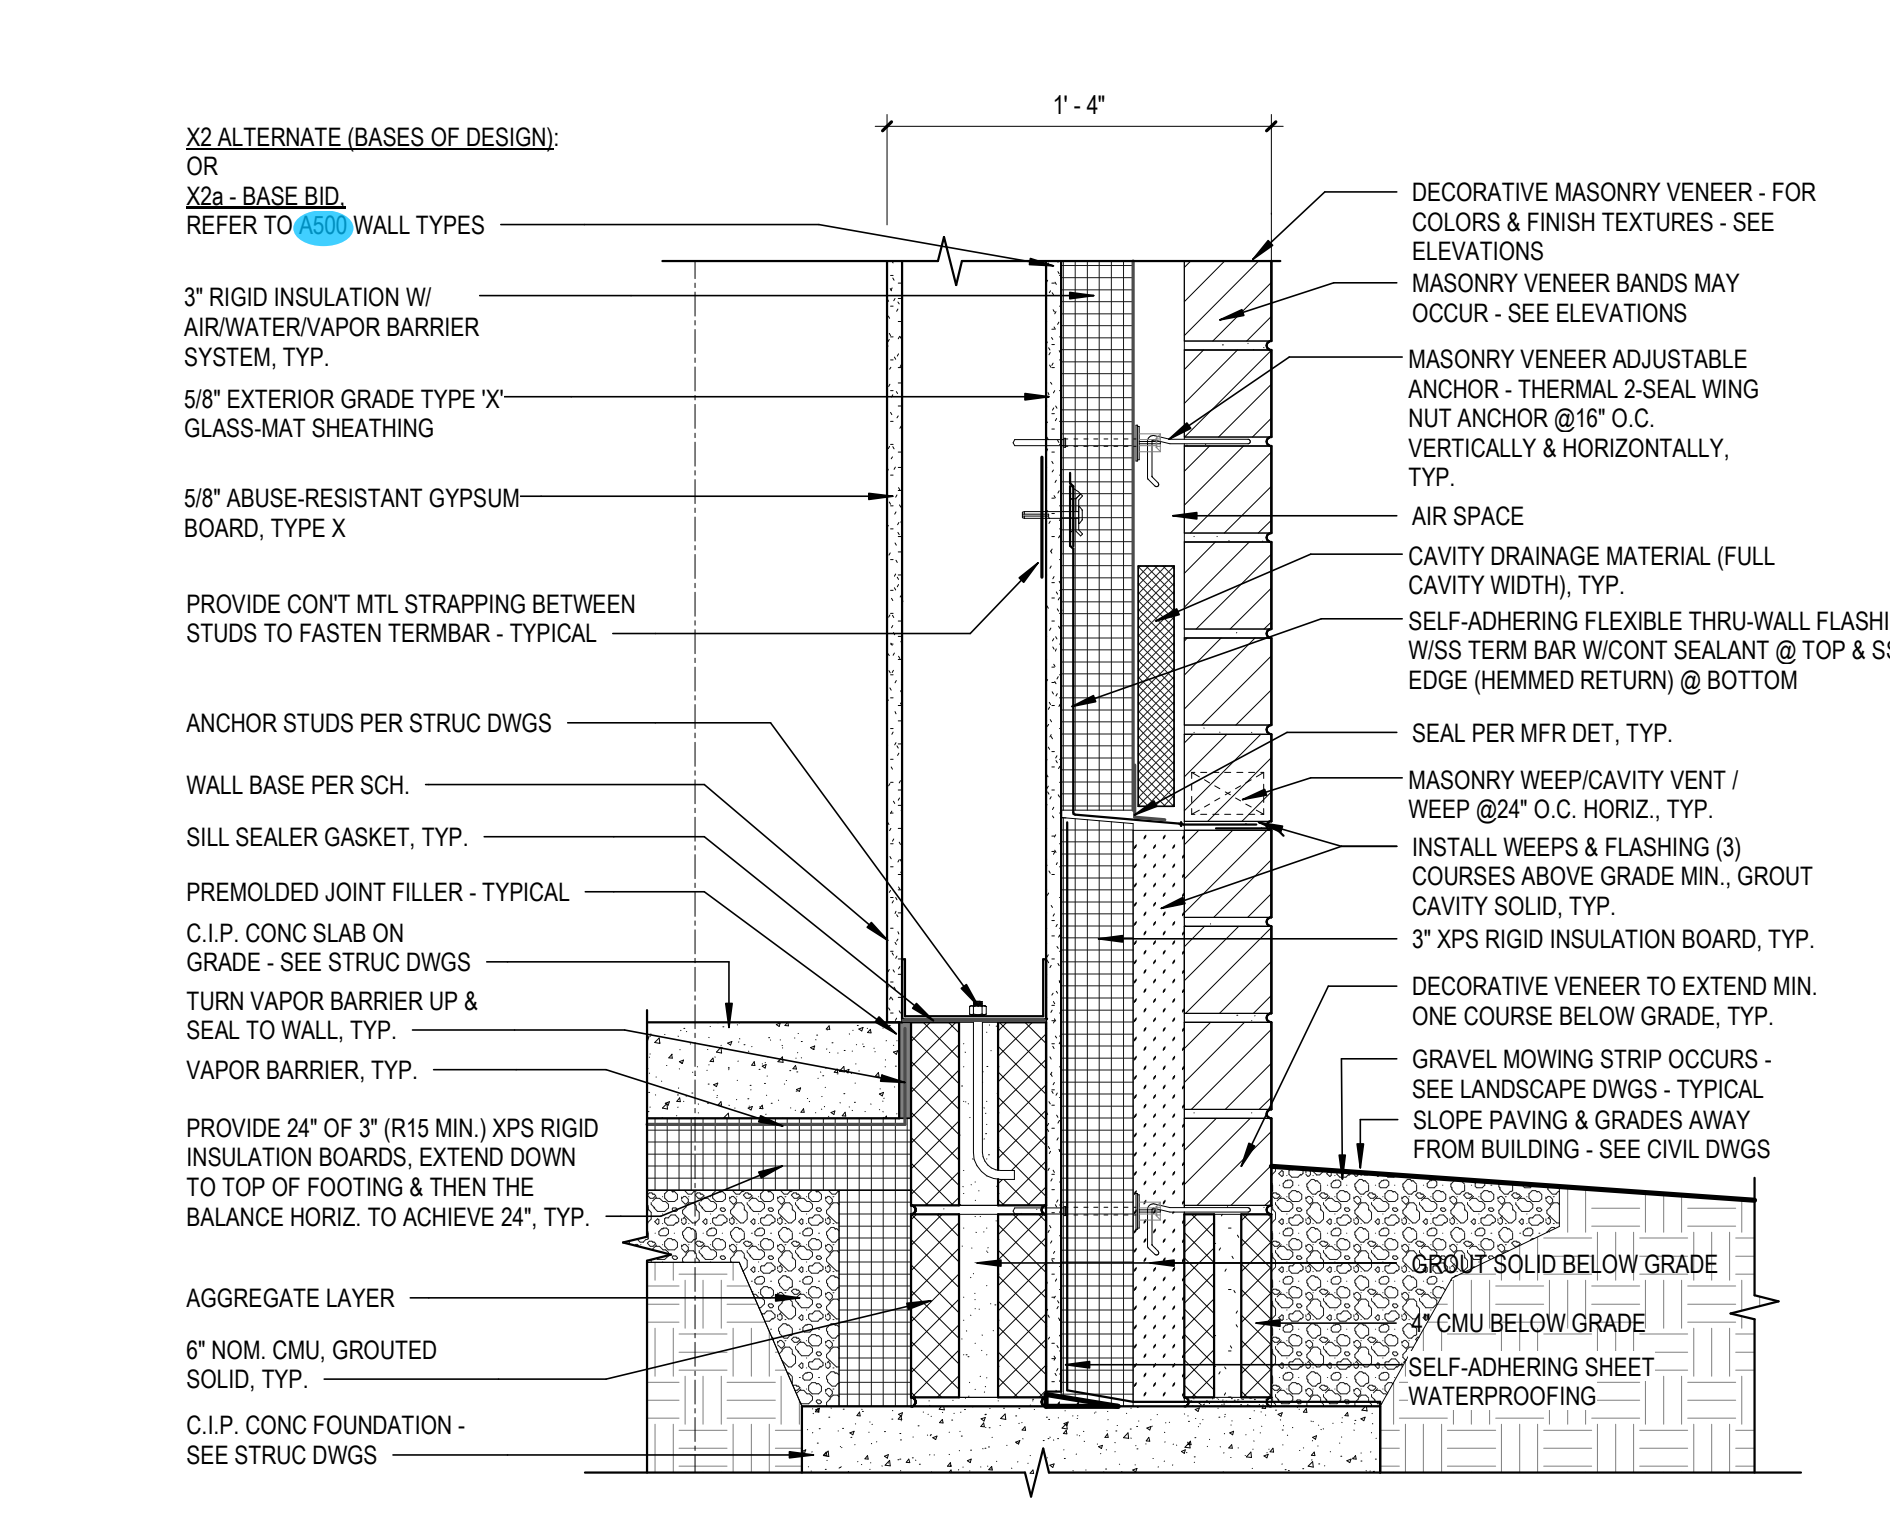


12 TYPICAL DETAIL
SCALE: 1 1/2" = 1'-0" REF. FROM: 5 / A540

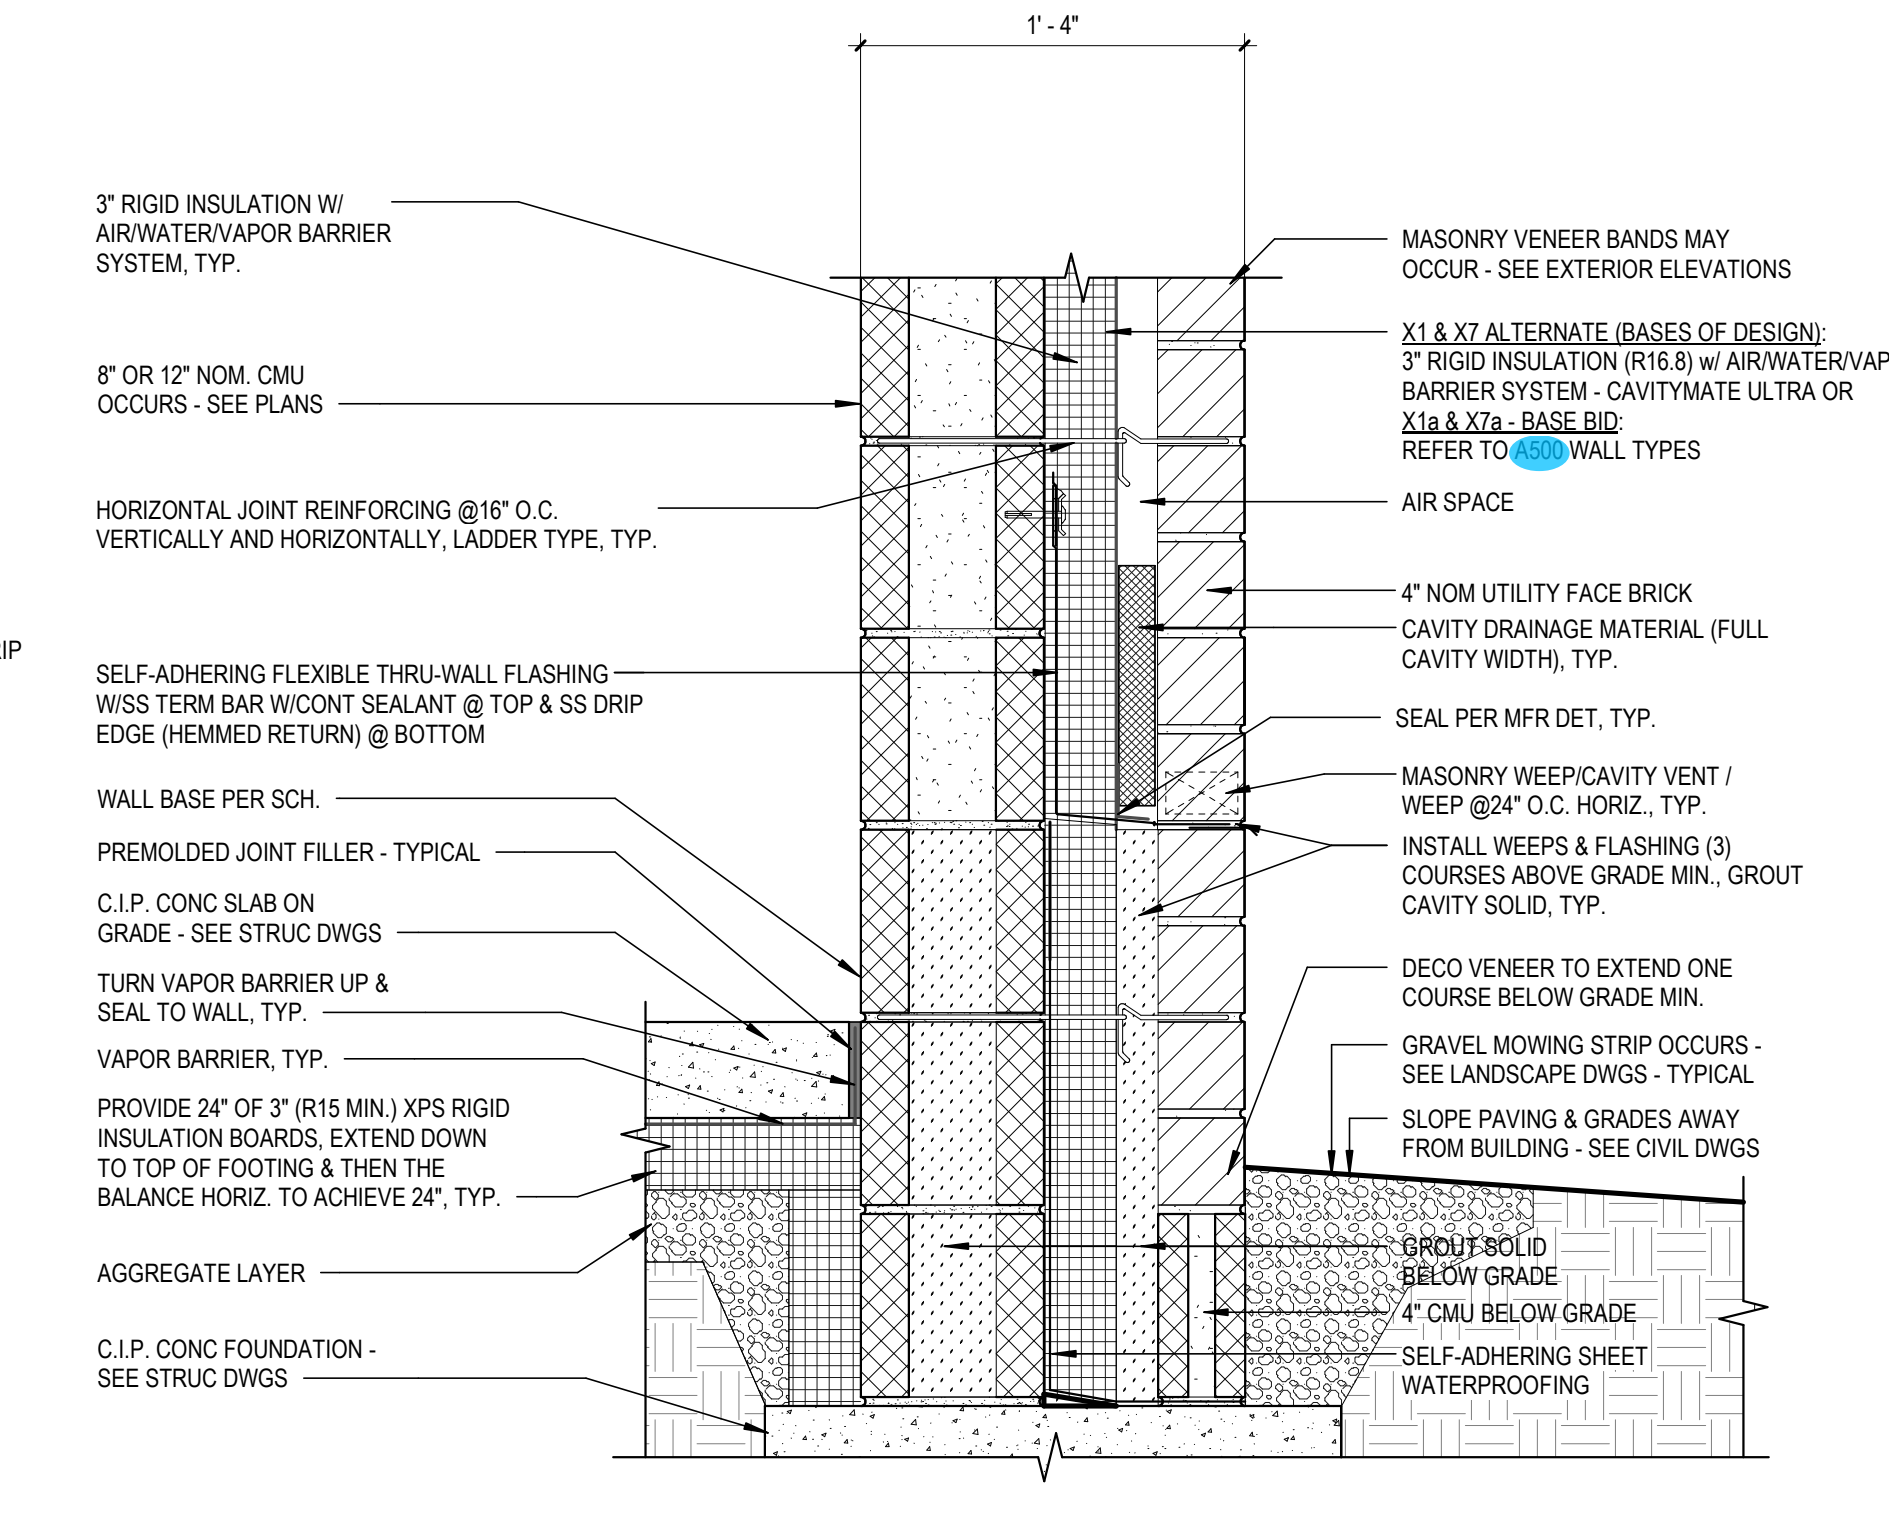

13 TYPICAL DETAIL
SCALE: 1 1/2" = 1'-0" REF. FROM: 1 / A511

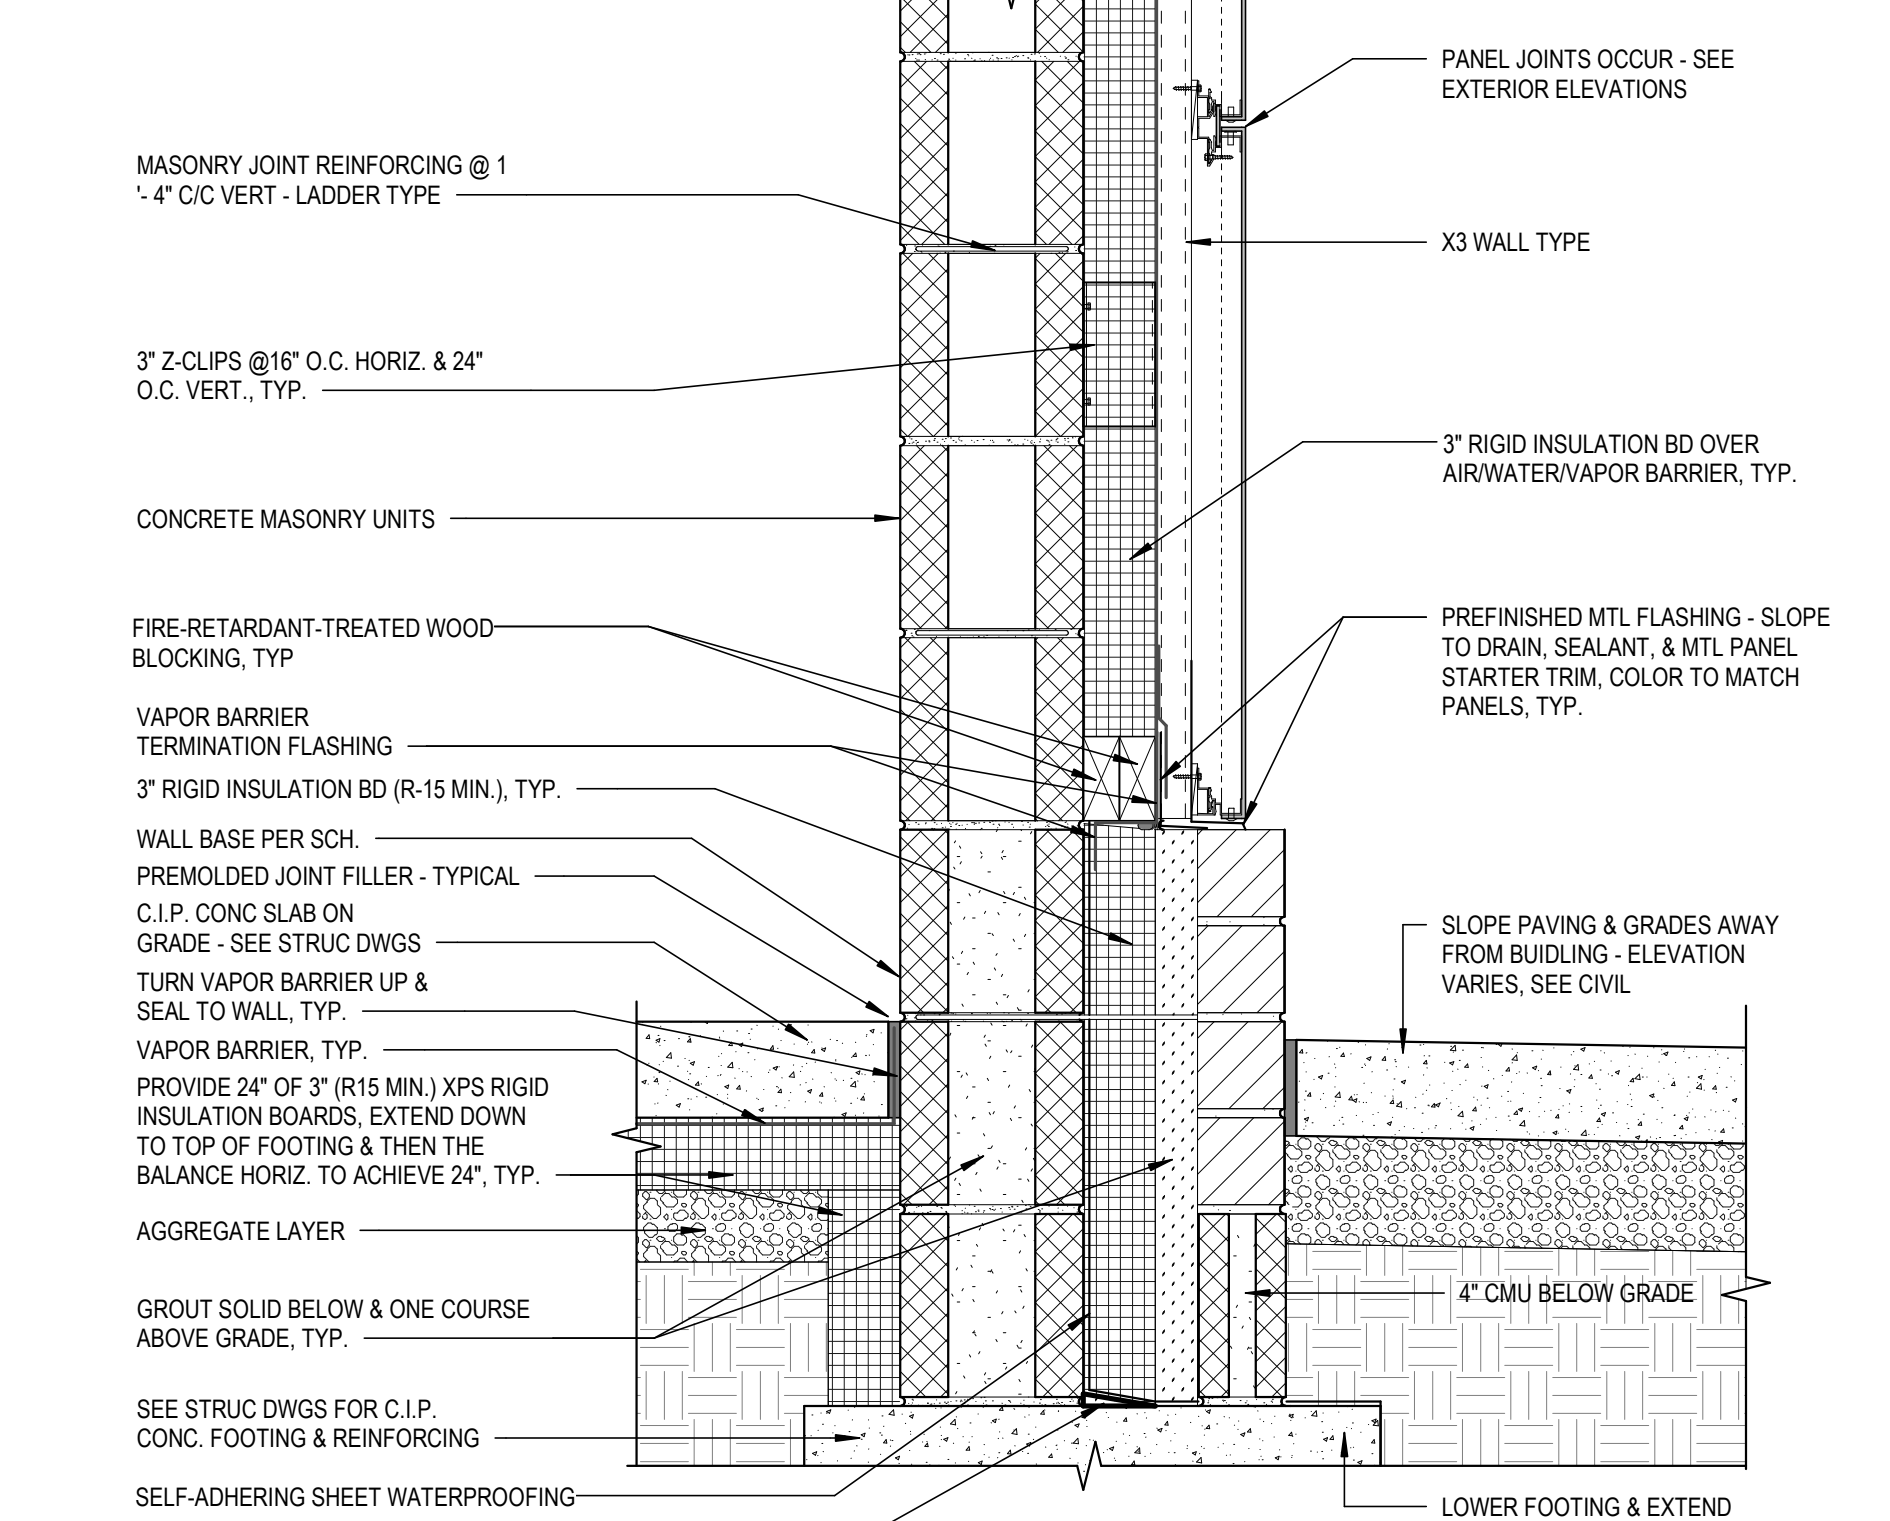

14 TYPICAL DETAIL
SCALE: 1 1/2" = 1'-0" REF. FROM: 6 / A521

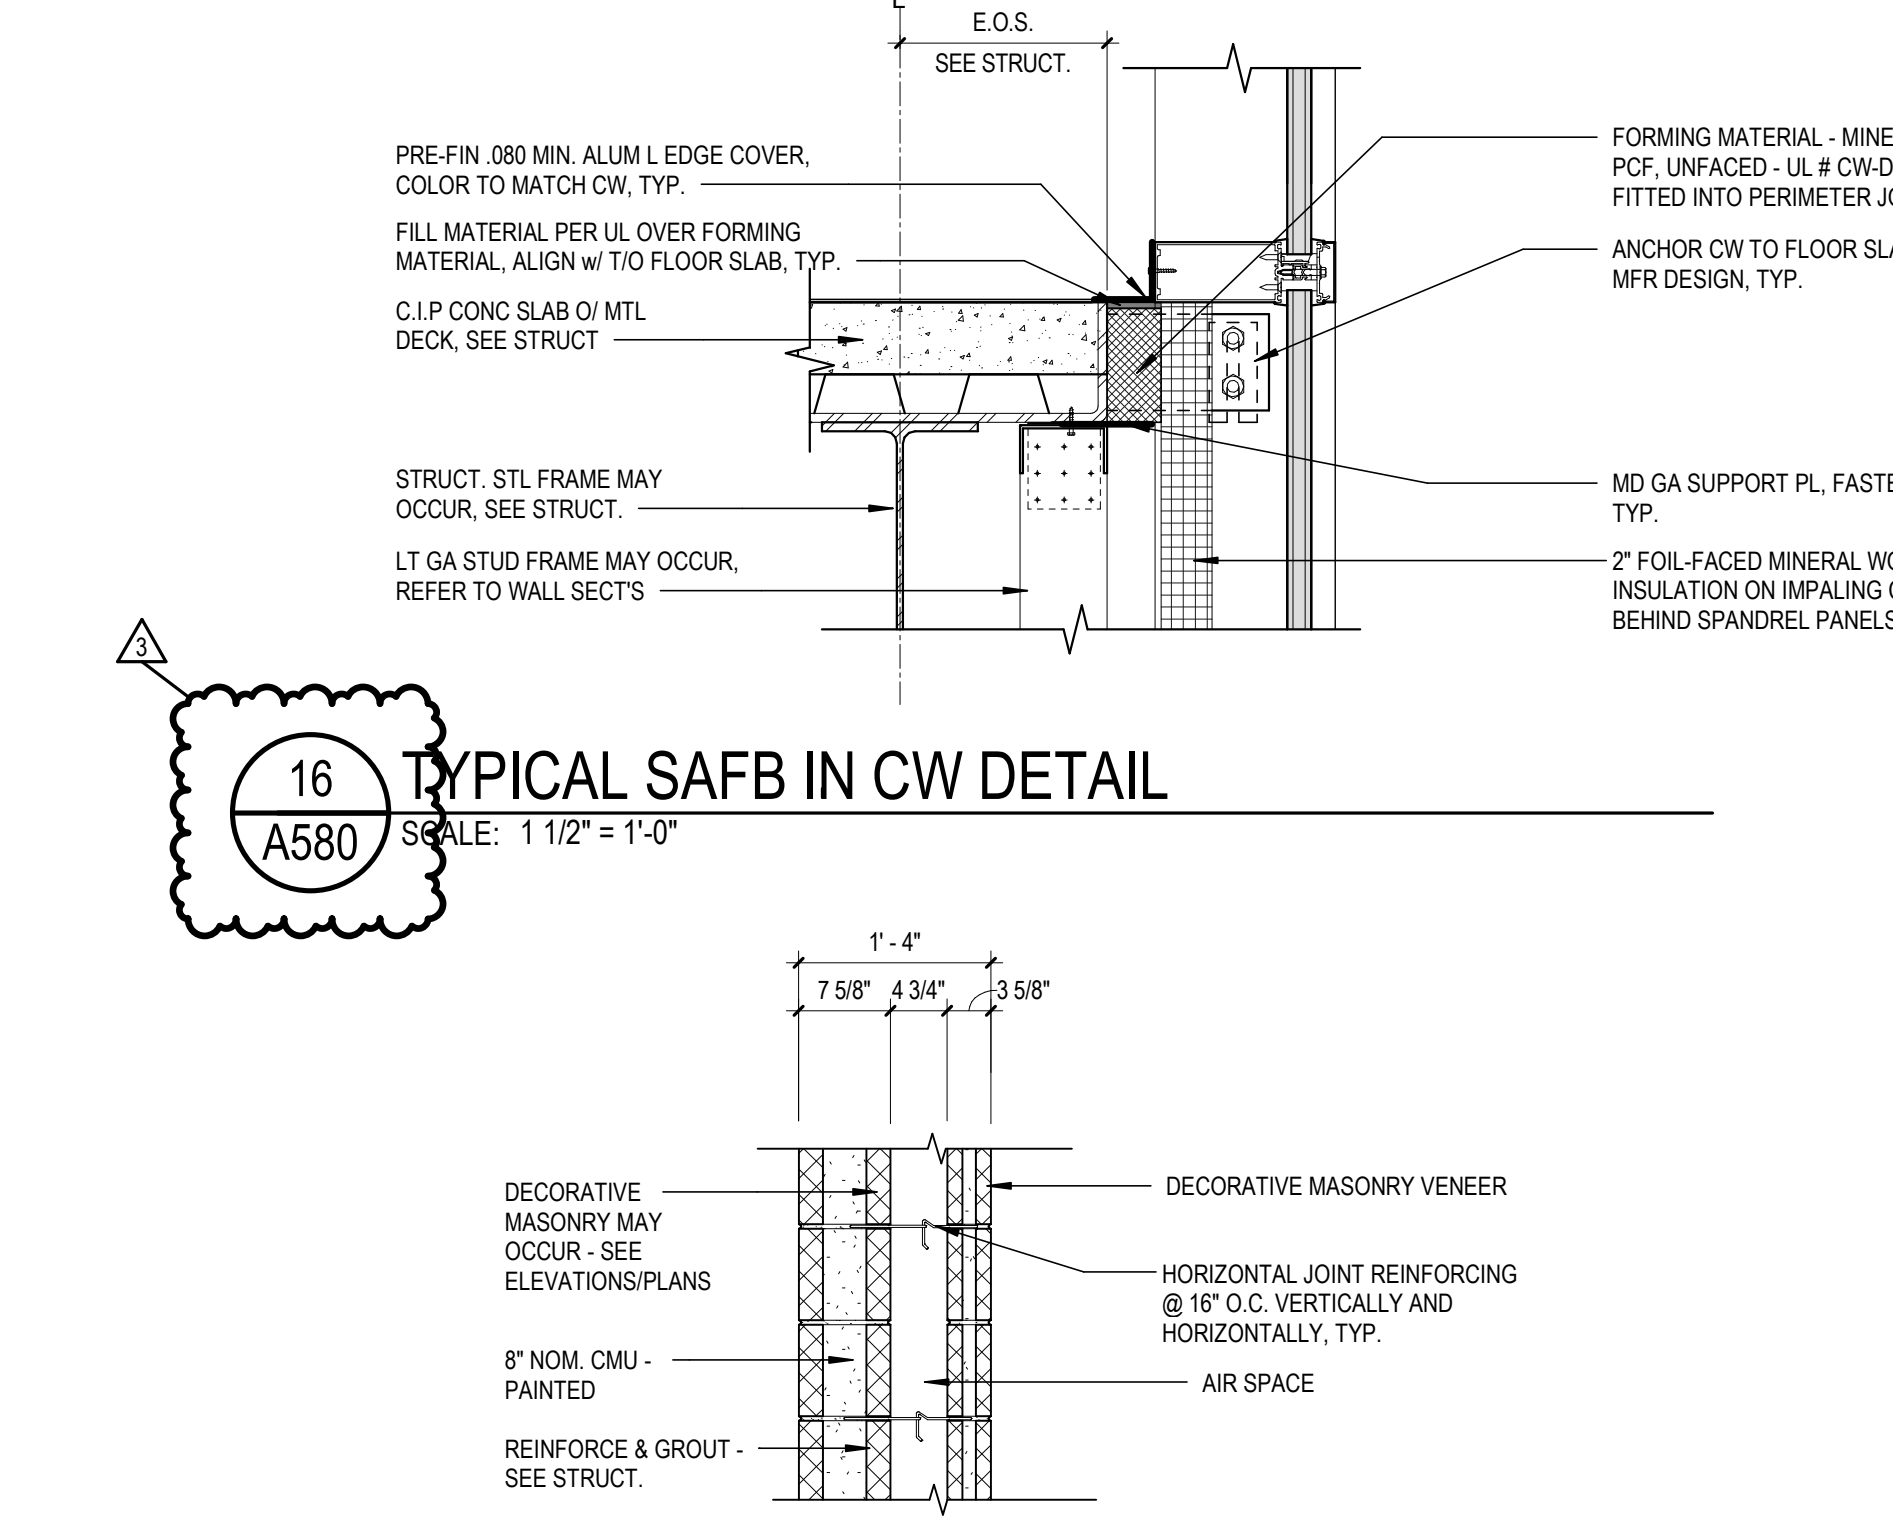

16 TYPICAL SAFB IN CW DETAIL
SCALE: 1 1/2" = 1'-0"

17 EXTERIOR MASONRY SCREEN WALL
SCALE: 3/4" = 1'-0"

3 ADDENDUM 02		01/22/26
no.	description	999
Sheet Revisions		
06	CD	12/05/25
07	CD	09/04/25
04	PERMIT	07/25/25
02	DD	12/20/24
Project Issues		
no.	description	999
Project Issues		
Design and construction documents are instruments of service and are to be used only for the project and site specified. Any other use without the written consent of the architect is prohibited. The architect shall not be responsible for construction methods or materials not specified in the documents.		
drawn by:	TDA	
checked by:	TDA	
sheet number:	A580	
job number:	23099	