



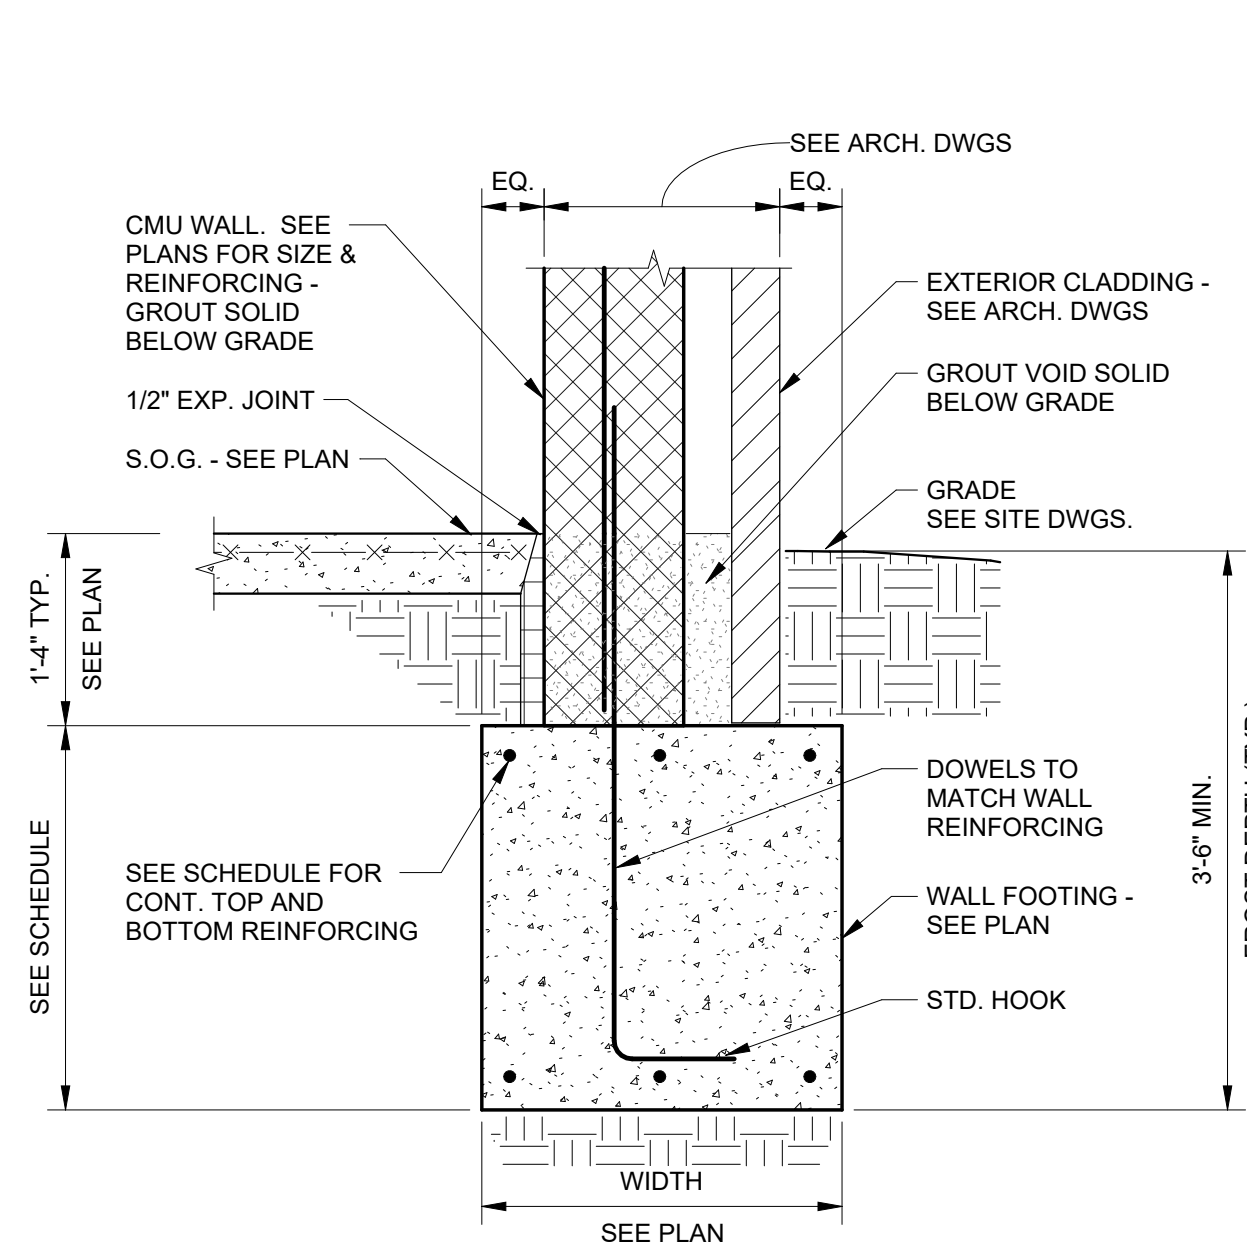


EXTERIOR TRENCH FOOTING DETAIL

SECTION 1
3/4" = 1'-0"

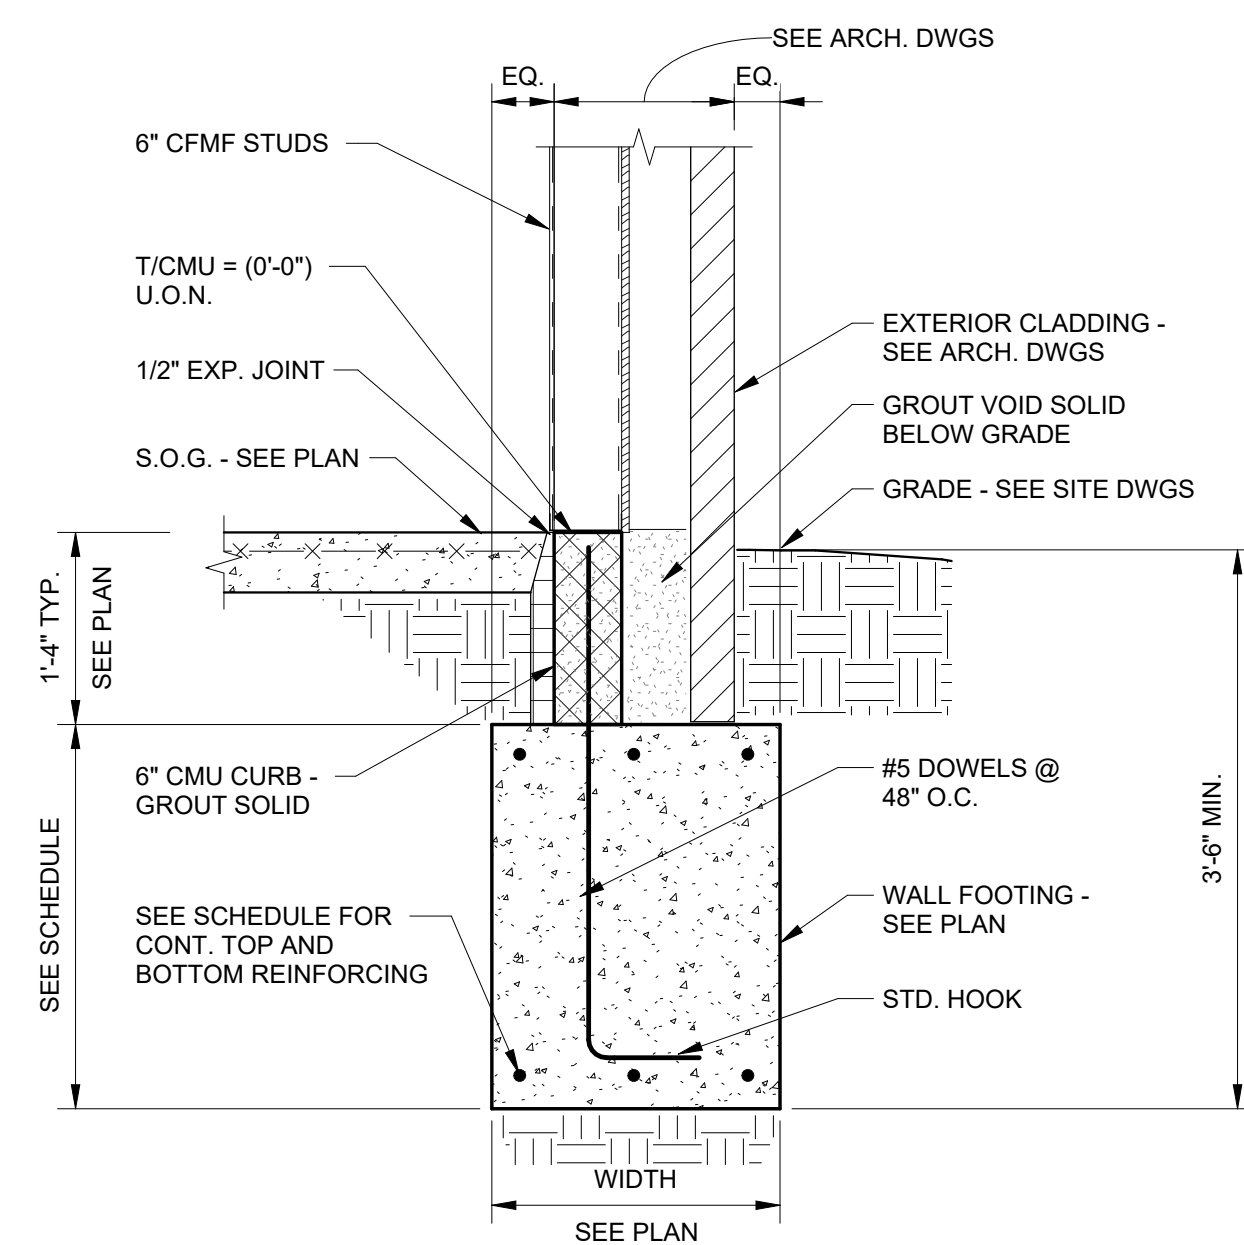


EXTERIOR TRENCH FOOTING DETAIL

SECTION 2
3/4" = 1'-0"

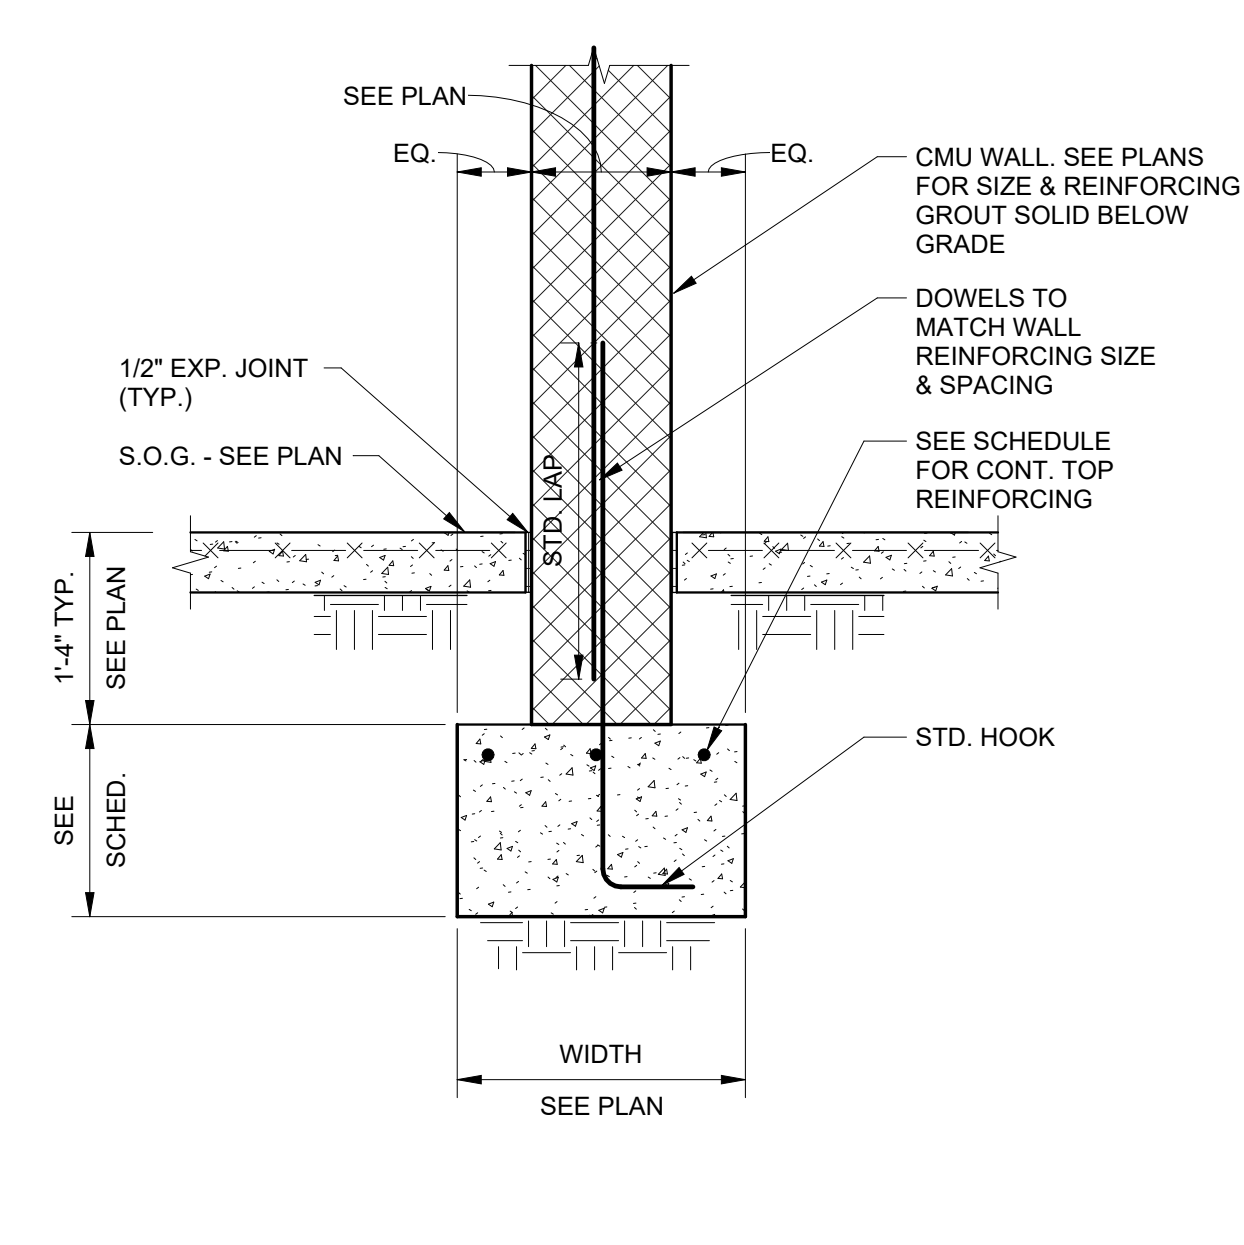


INTERIOR TRENCH FOOTING DETAIL

SECTION 3
3/4" = 1'-0"

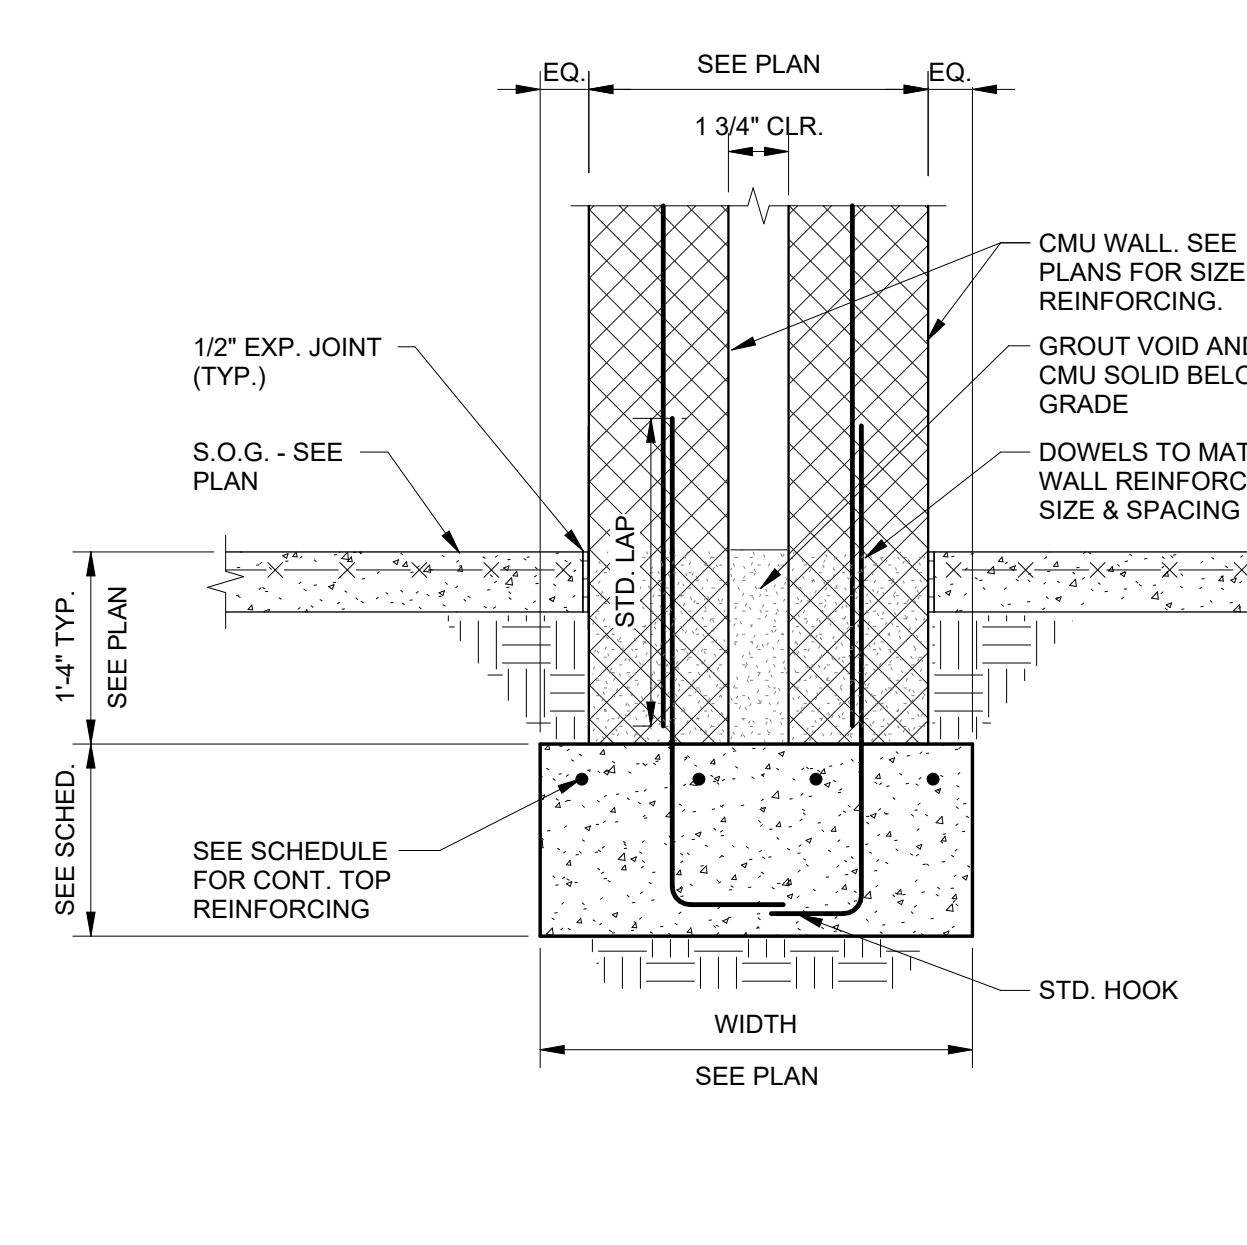


FIREWALL TRENCH FOOTING DETAIL

SECTION 4
3/4" = 1'-0"

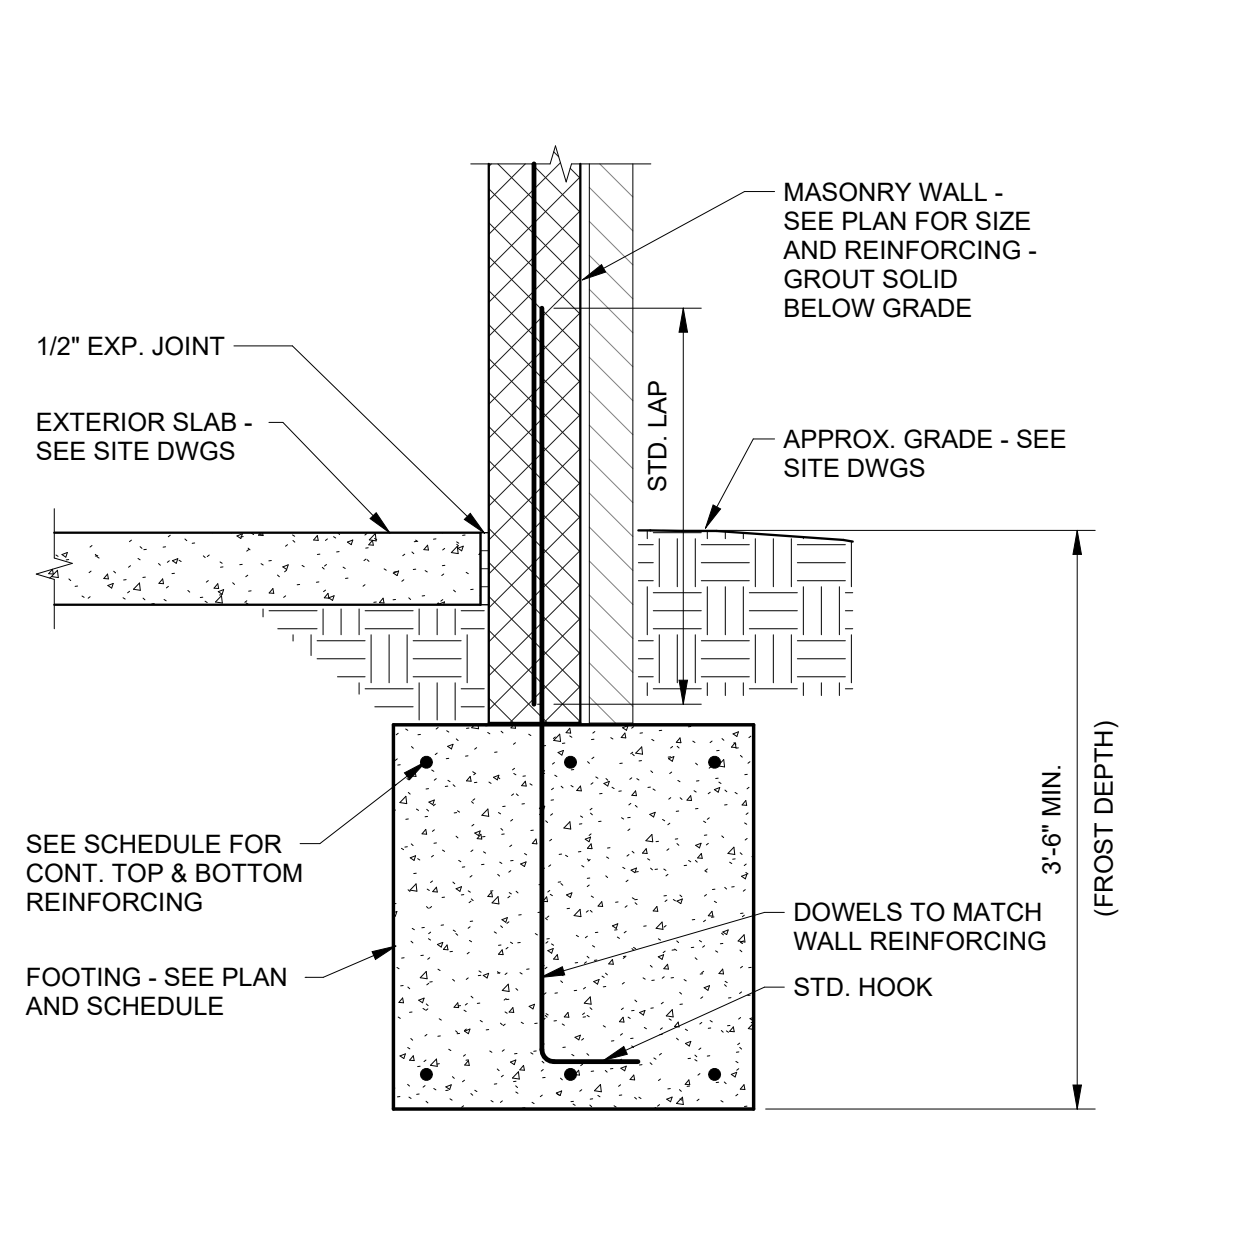


MASONRY SCREEN WALL DETAIL

SECTION 5
3/4" = 1'-0"

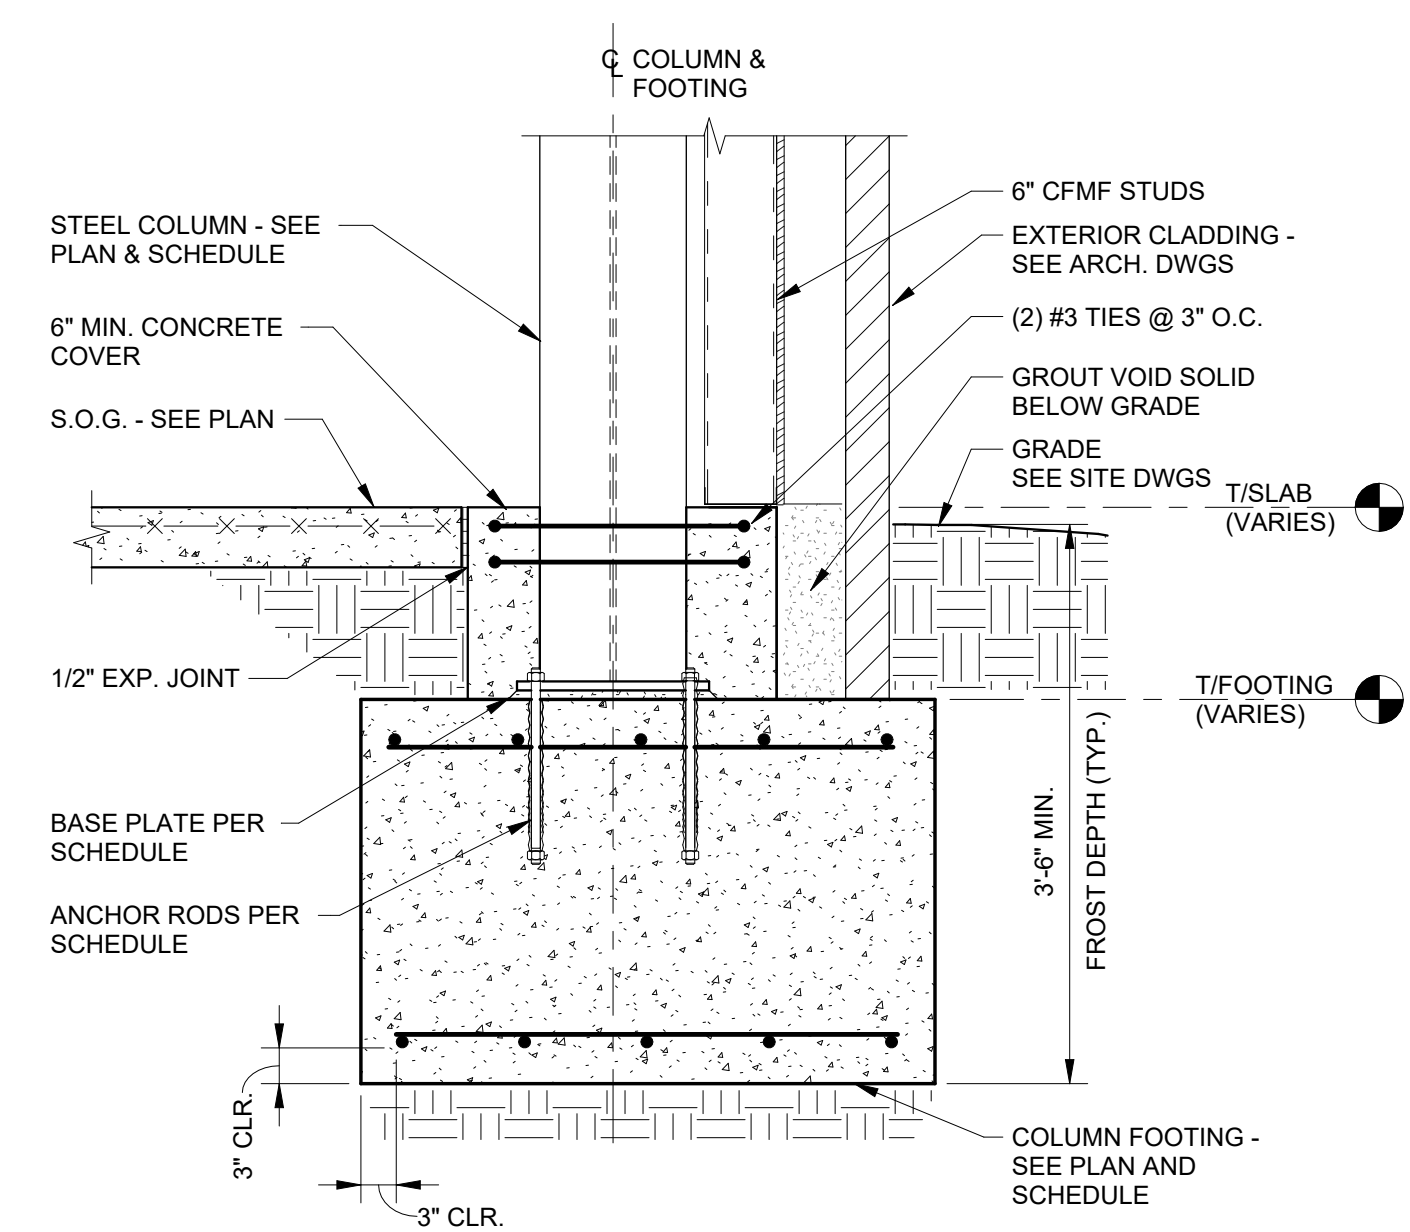


EXTERIOR COLUMN FOOTING DETAIL


SECTION 6
3/4" = 1'-0"

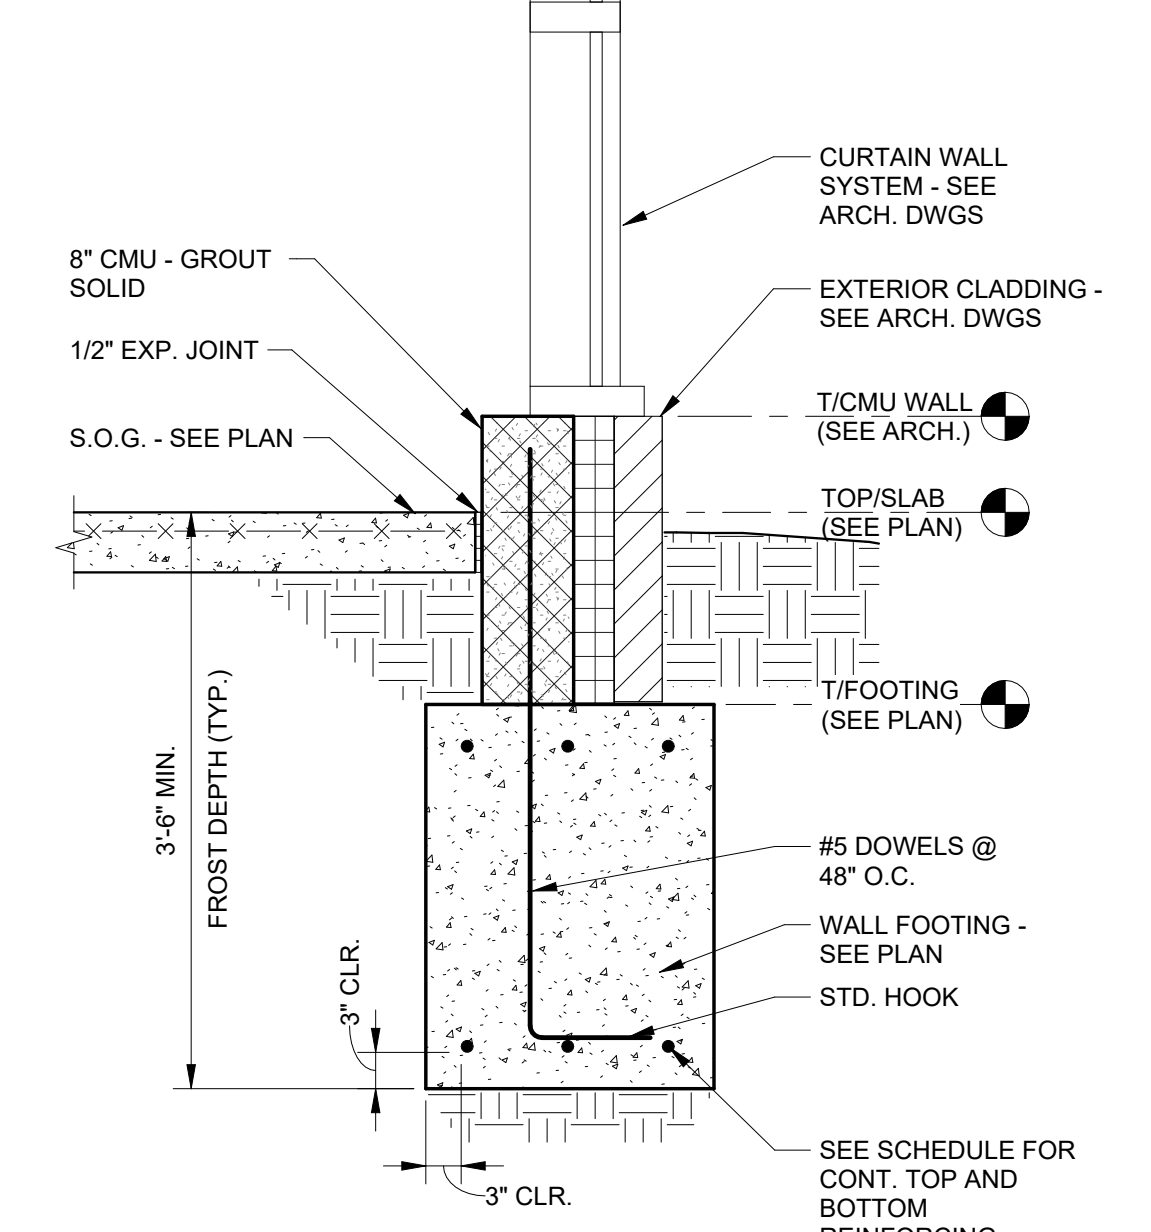

SECTION 7
3/4" = 1'-0"

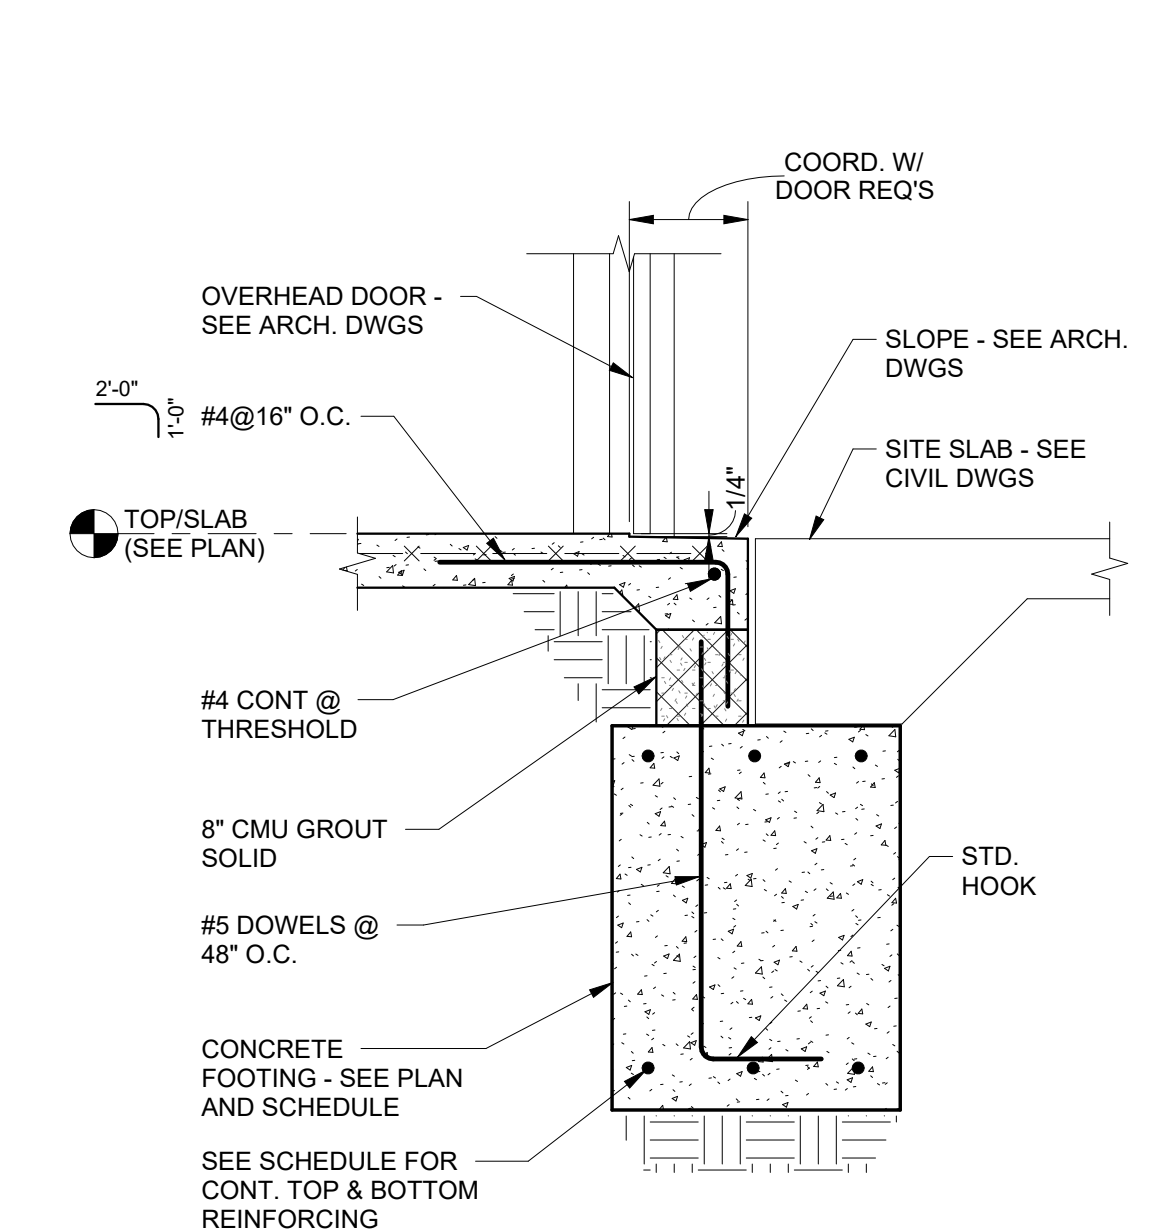


SECTION 8
3/4" = 1'-0"

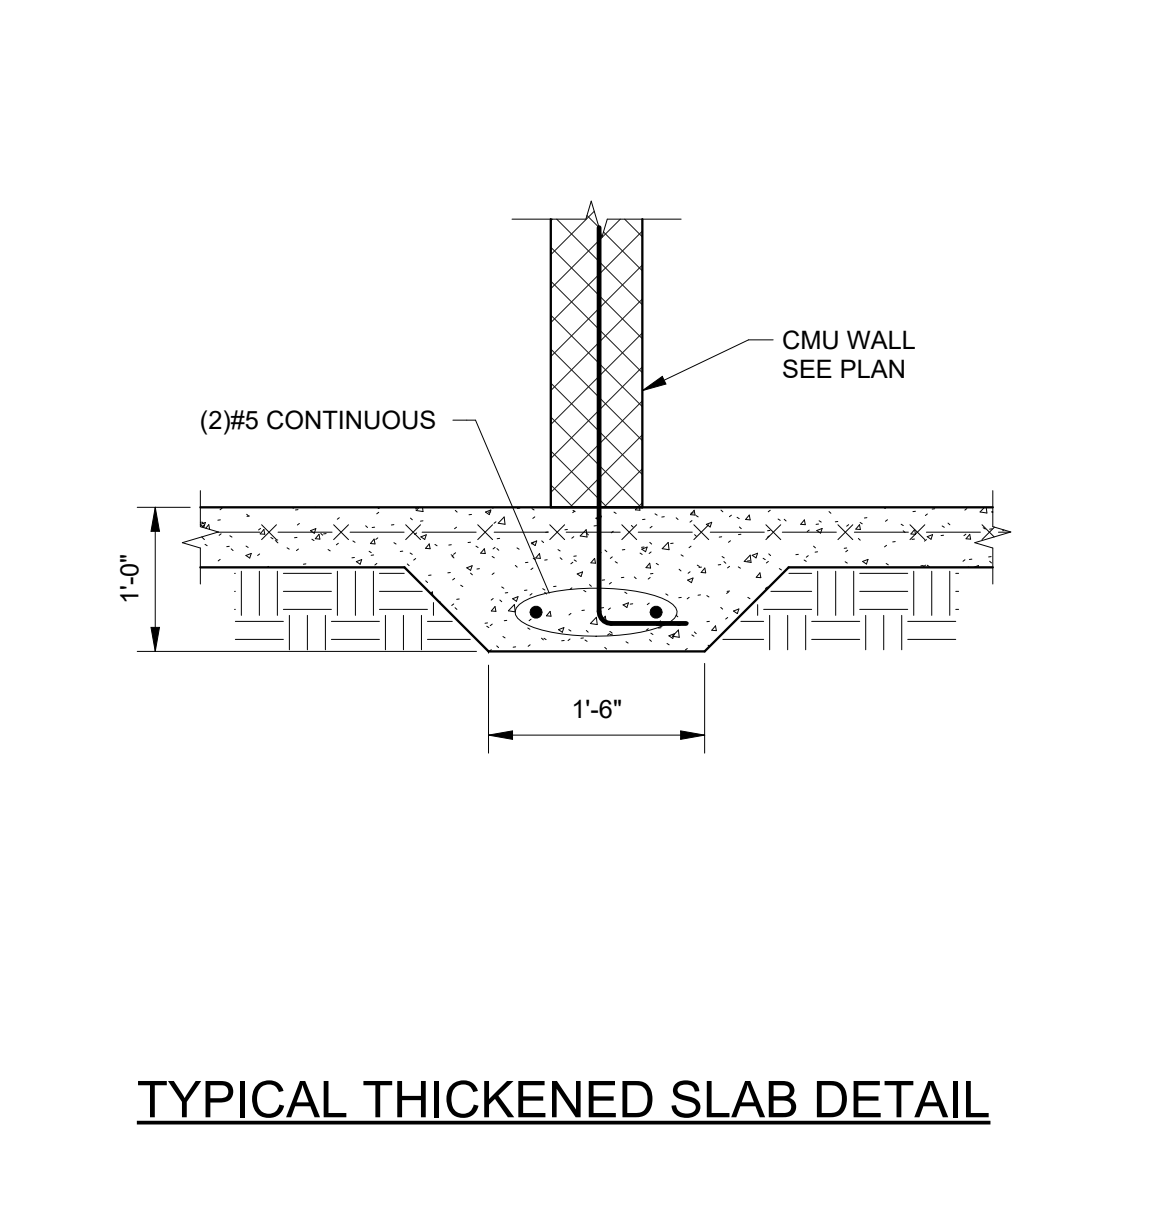


TYPICAL THICKENED SLAB DETAIL


SECTION 9
3/4" = 1'-0"

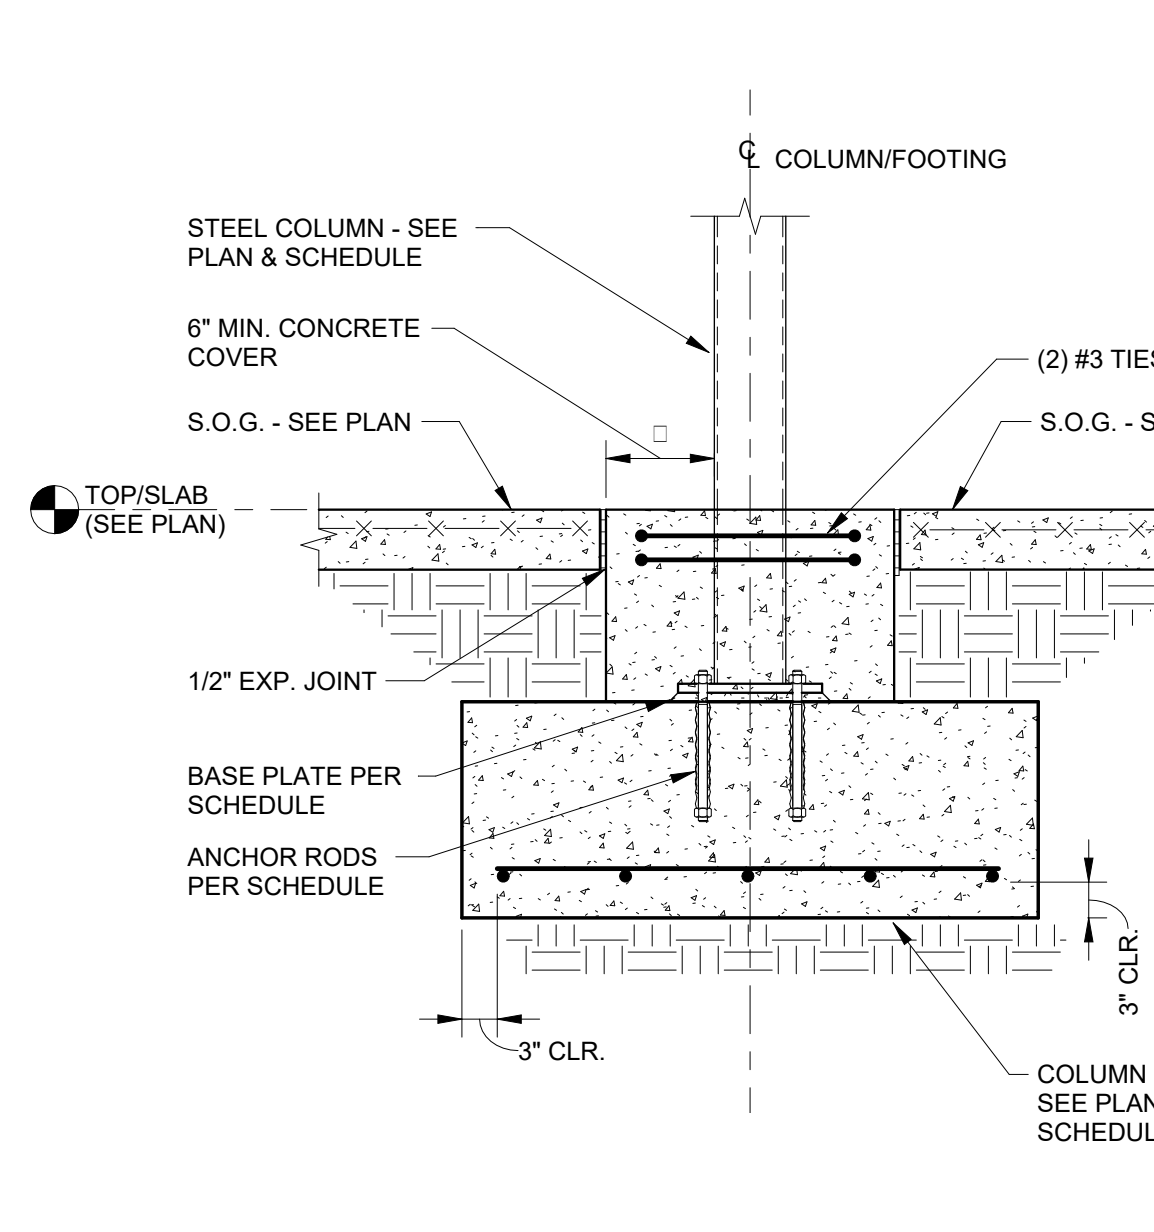


SECTION 10
3/4" = 1'-0"

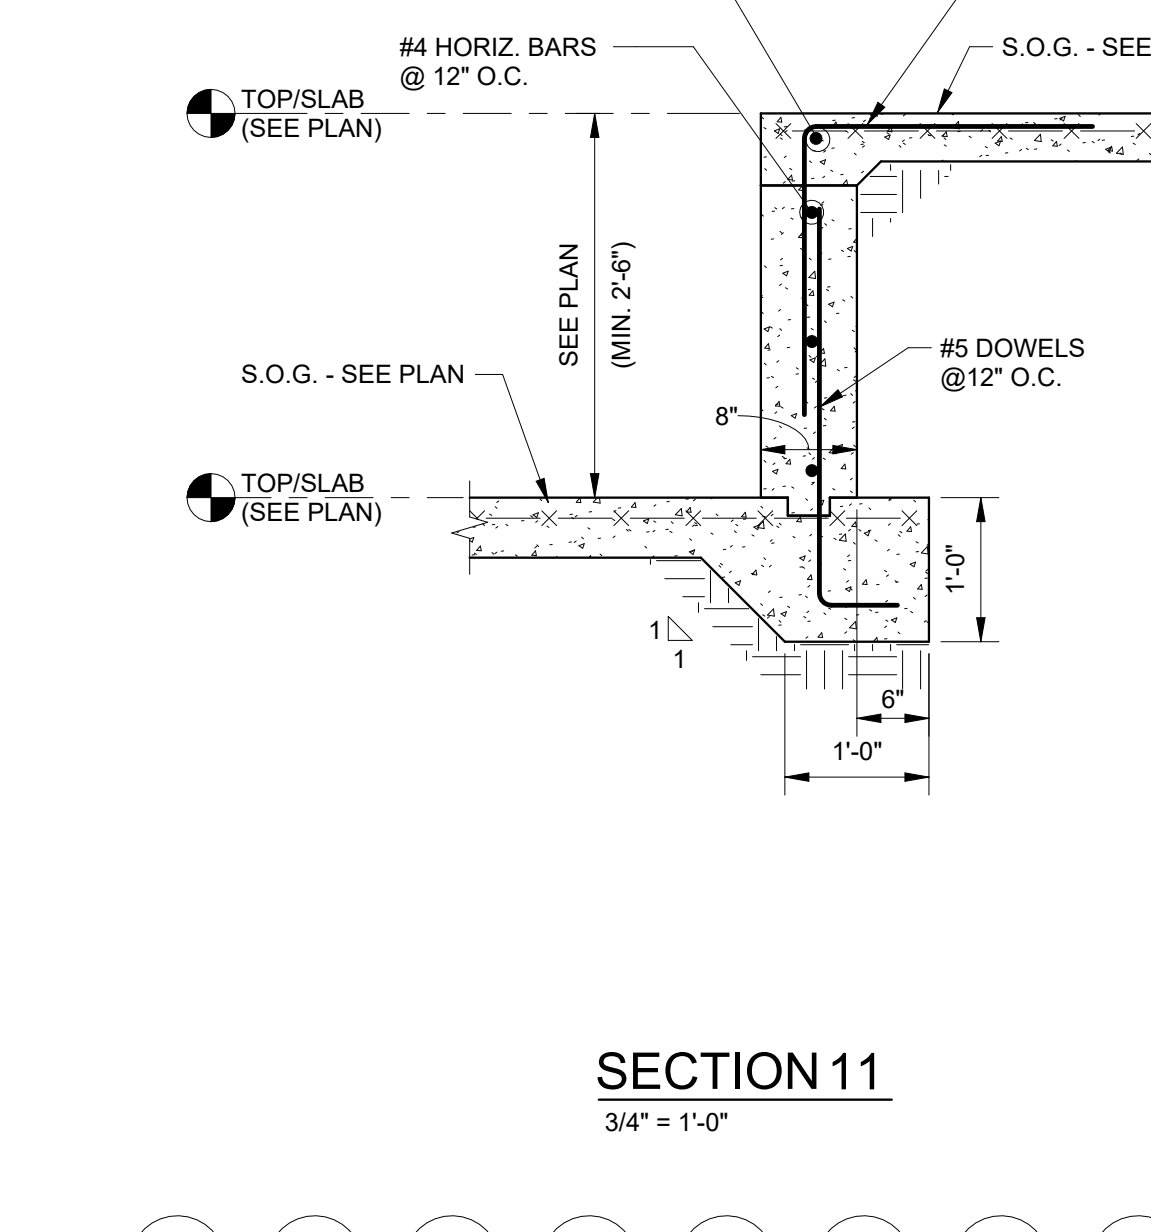


SECTION 11
3/4" = 1'-0"

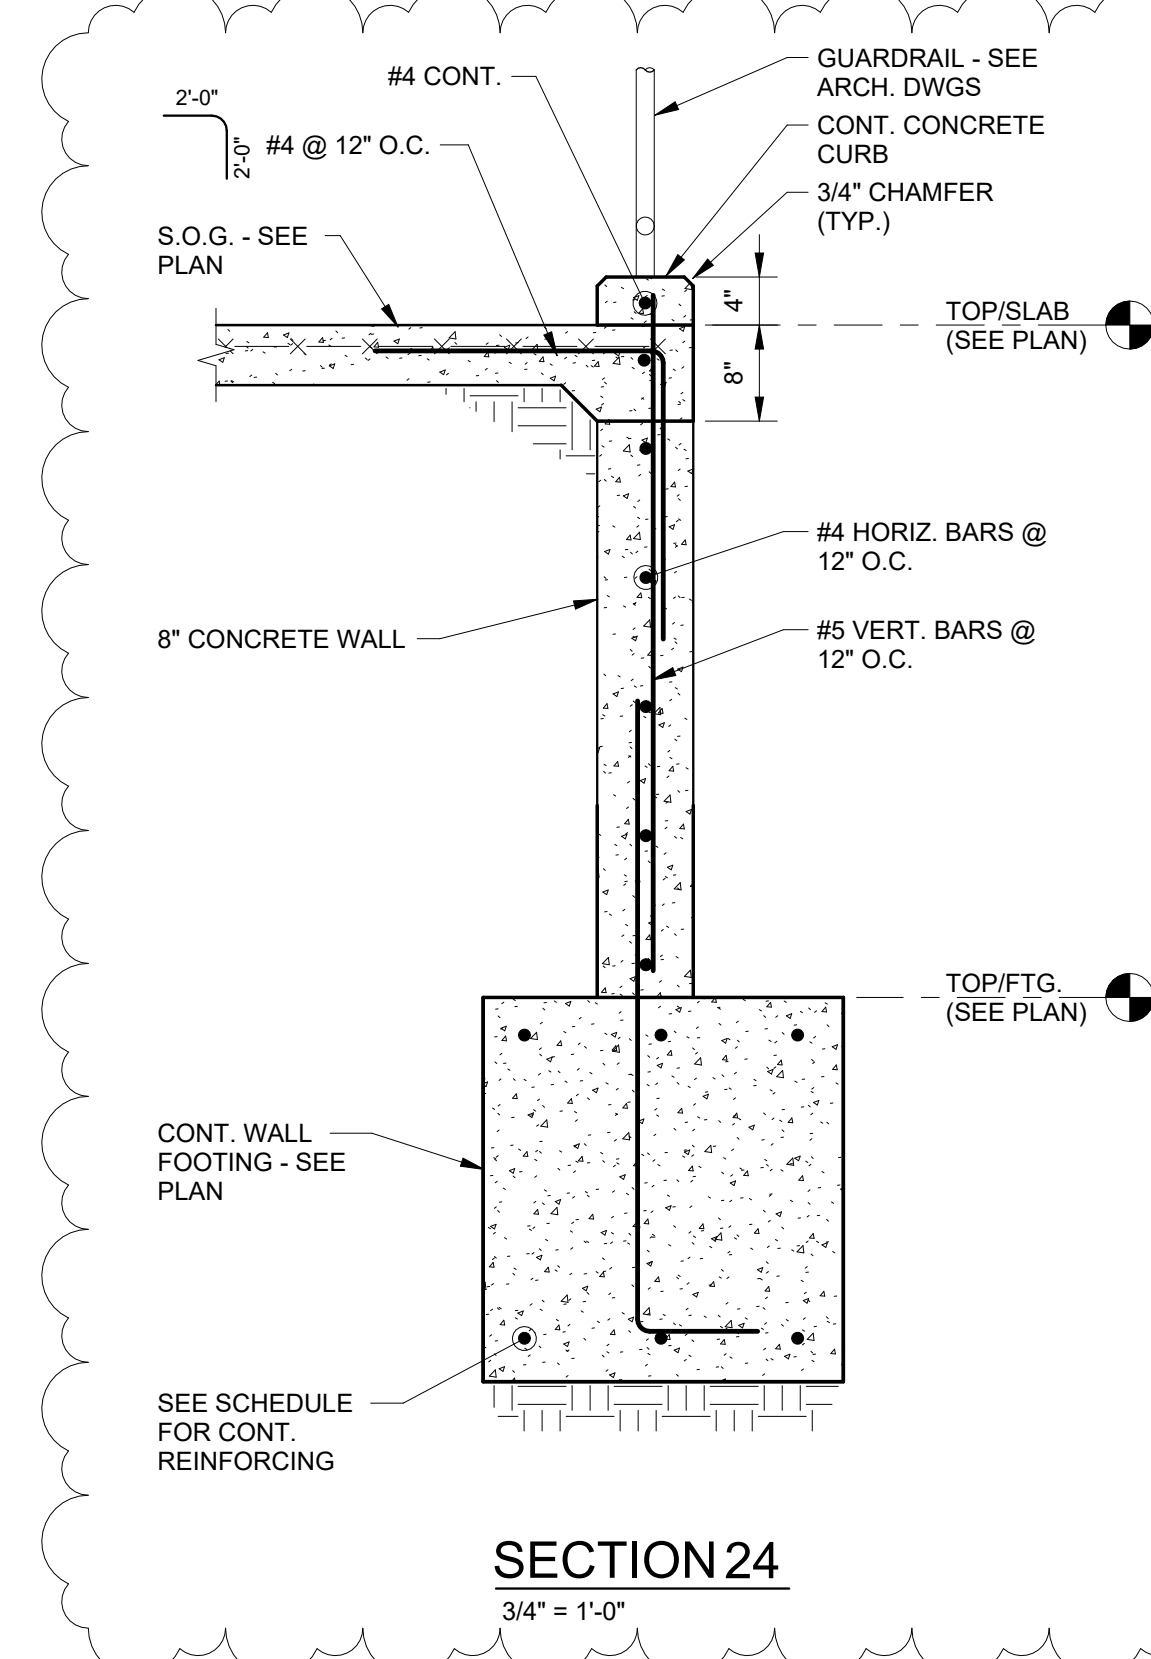


SECTION 24
3/4" = 1'-0"

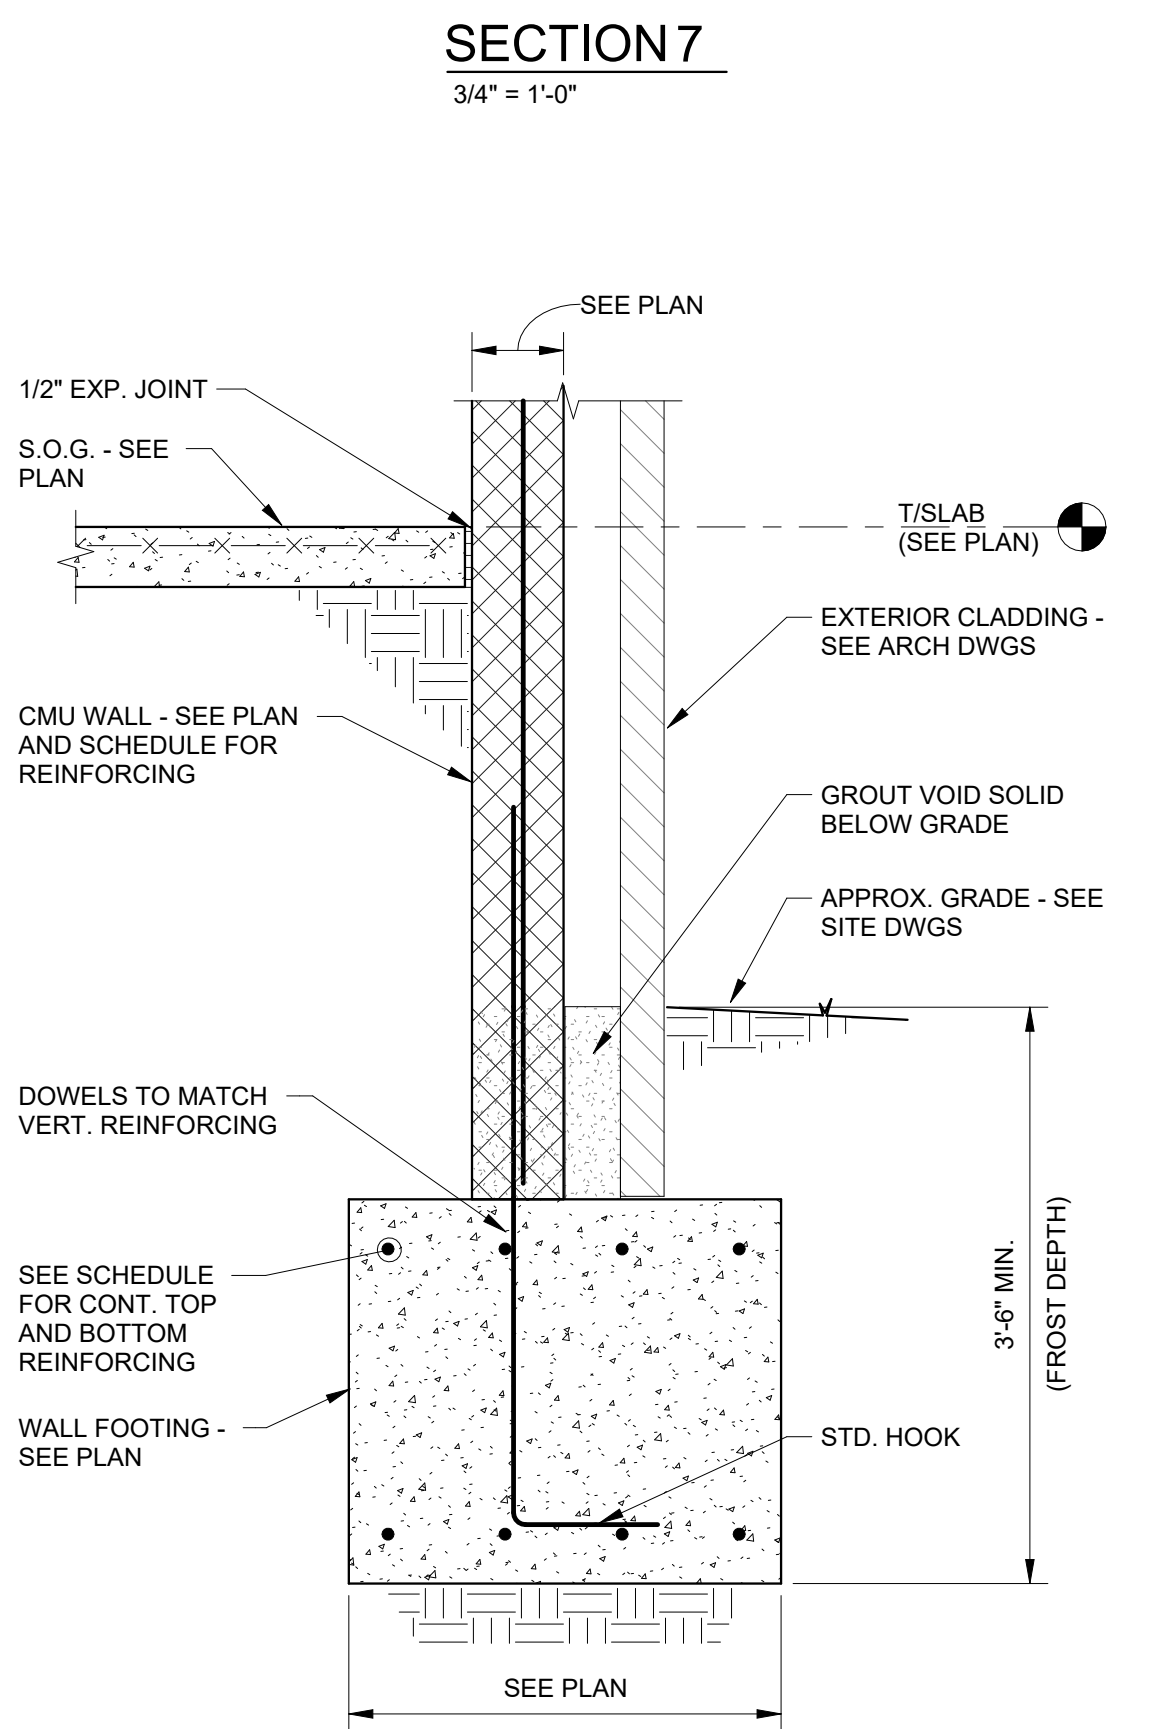

SECTION 14
3/4" = 1'-0"

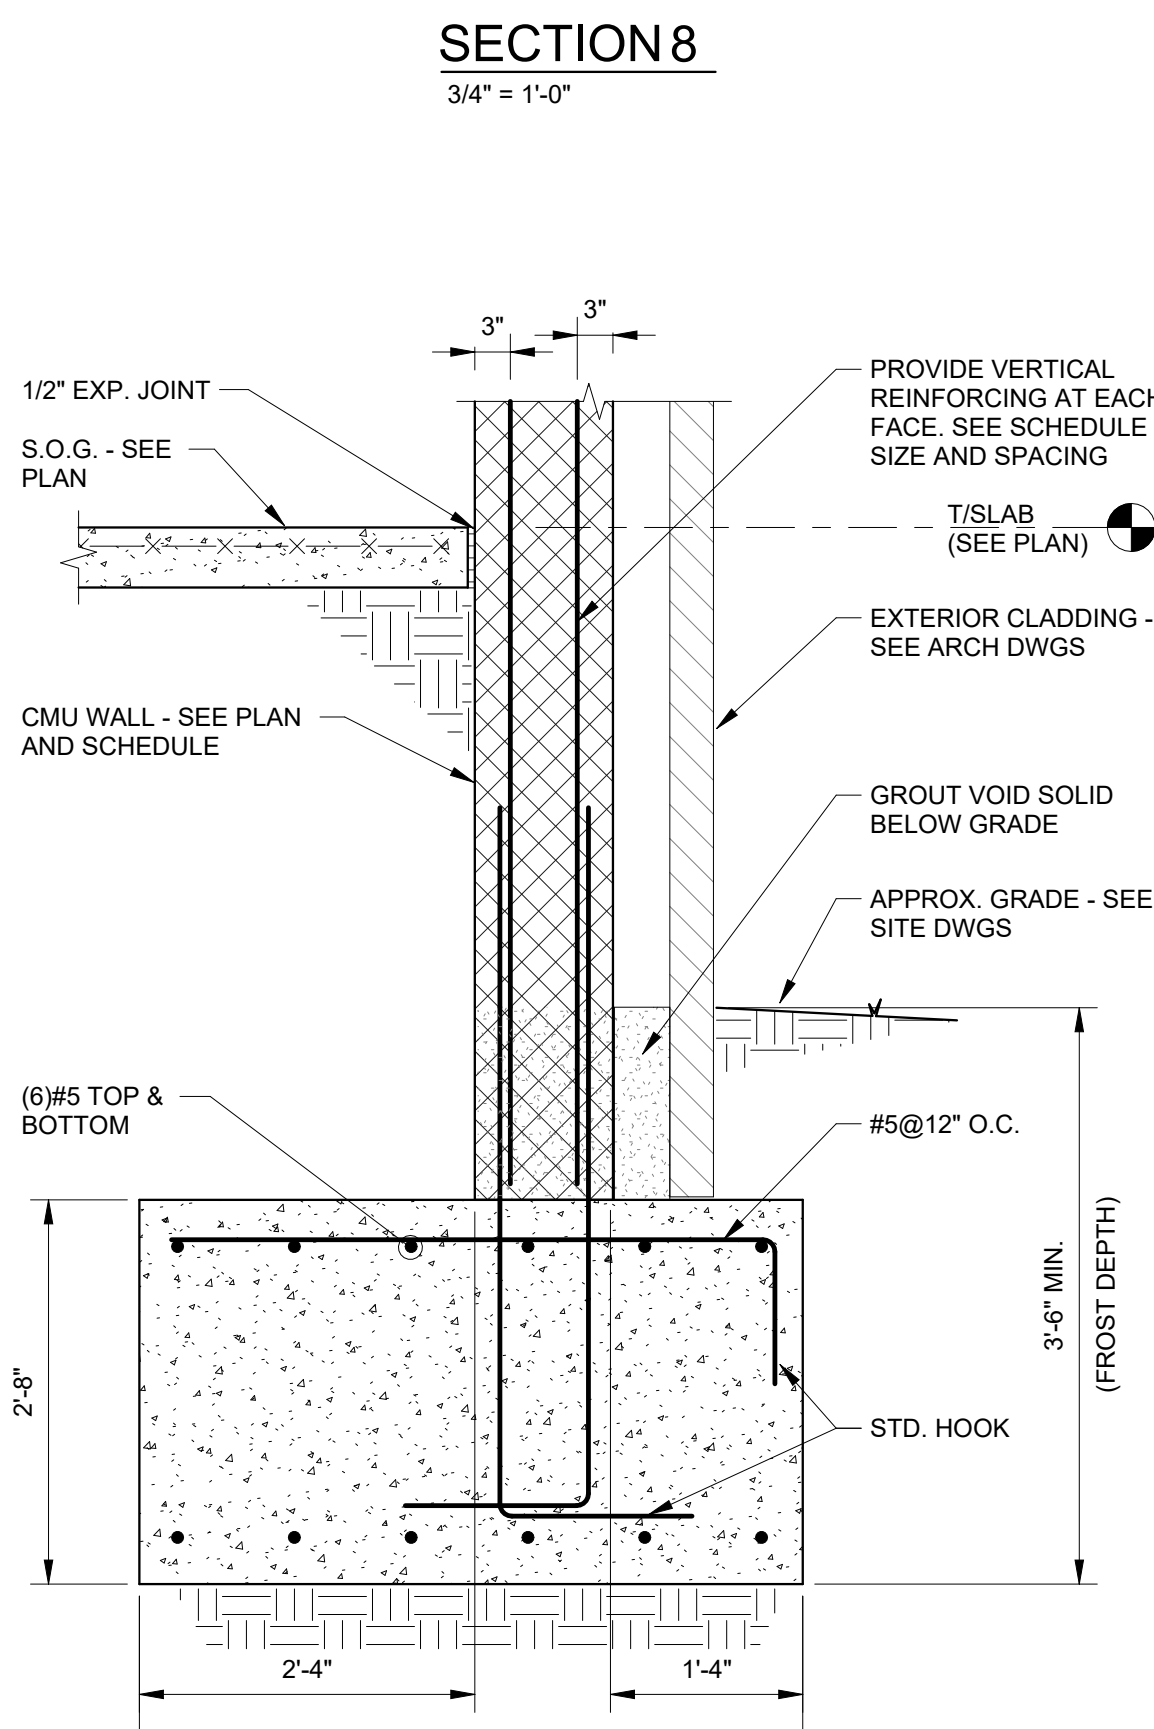


SECTION 15
3/4" = 1'-0"

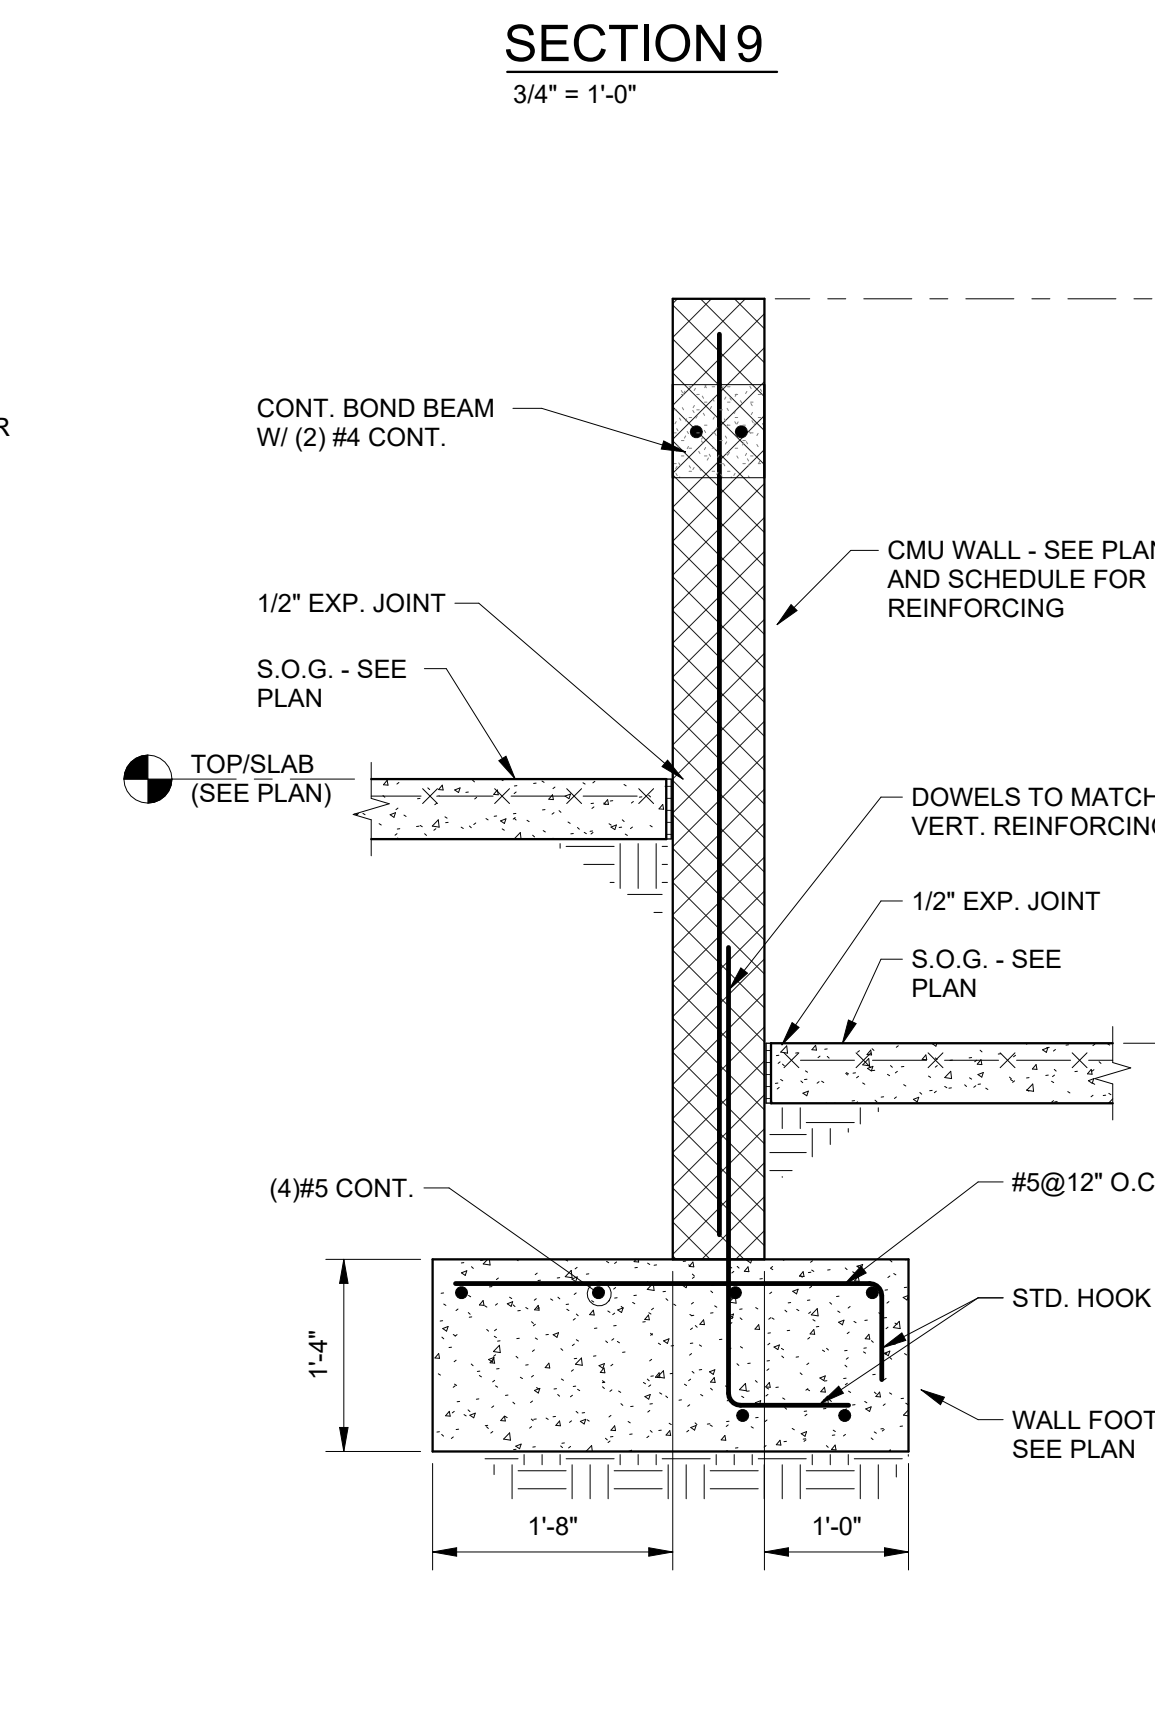


SECTION 16
3/4" = 1'-0"




SECTION 17
3/4" = 1'-0"

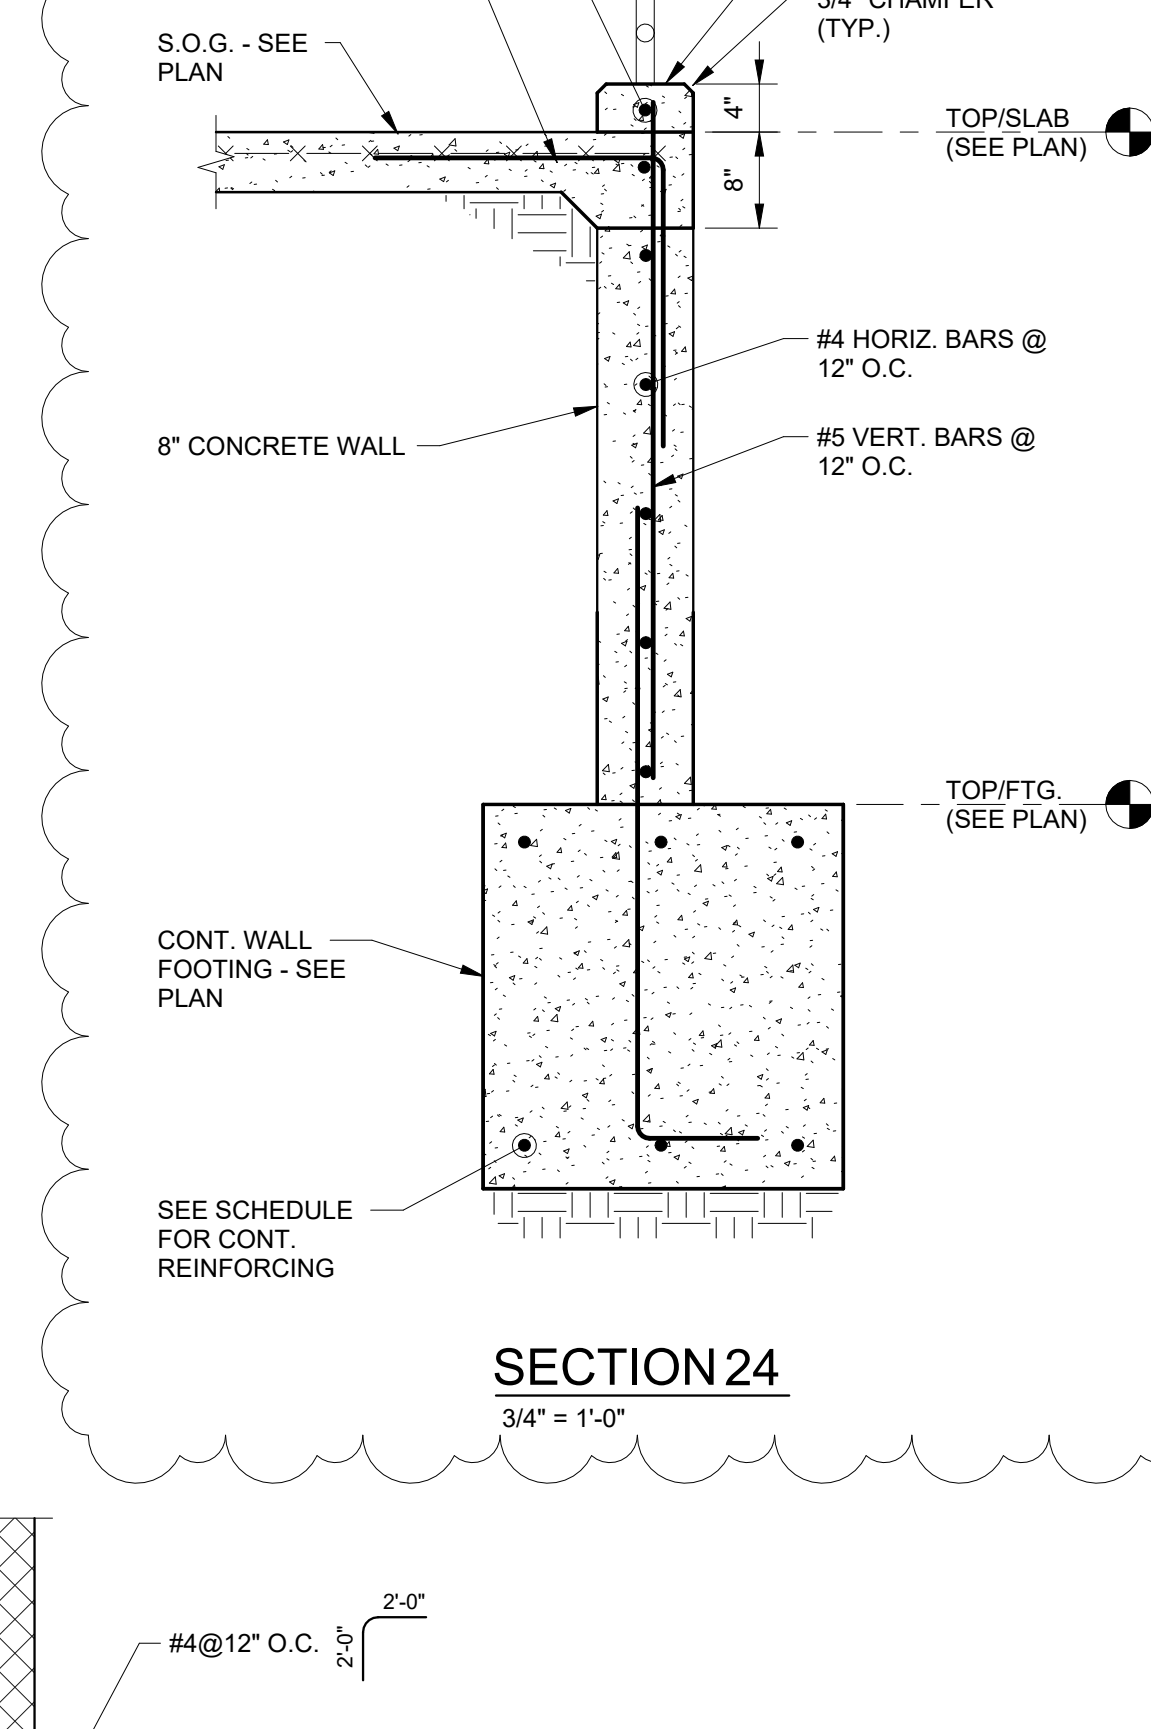


SECTION 18
3/4" = 1'-0"

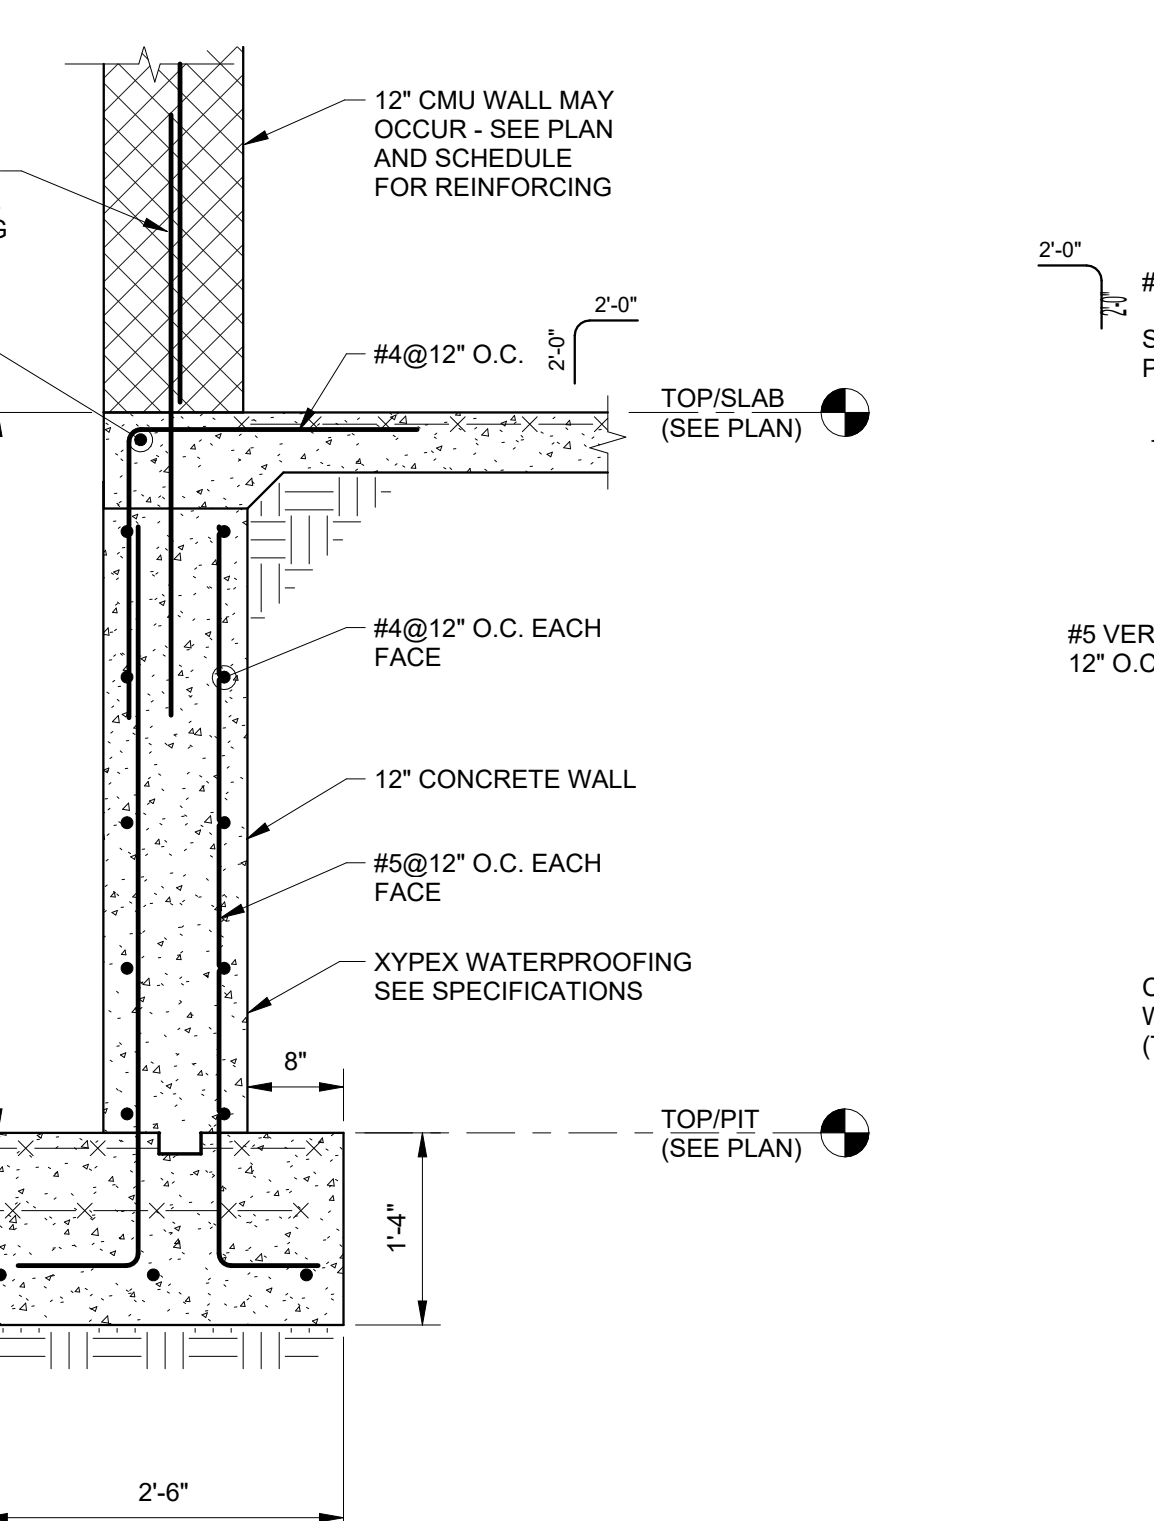


SECTION 20
3/4" = 1'-0"

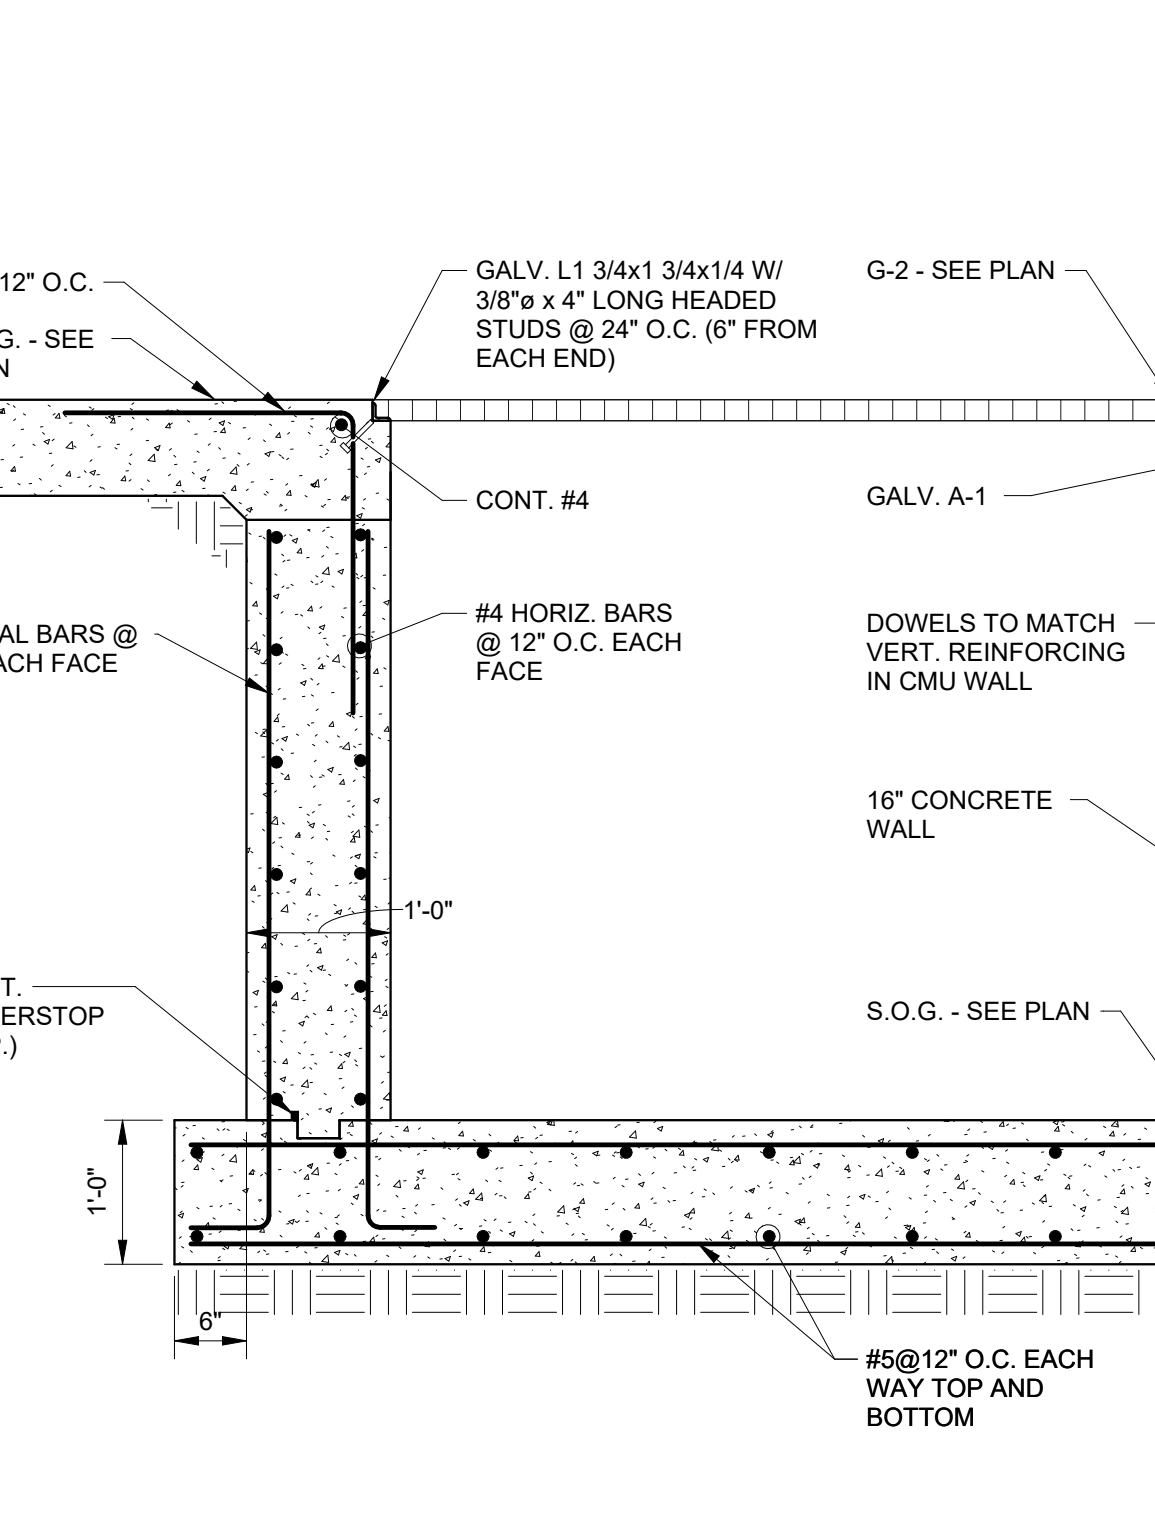

SECTION 21
3/4" = 1'-0"

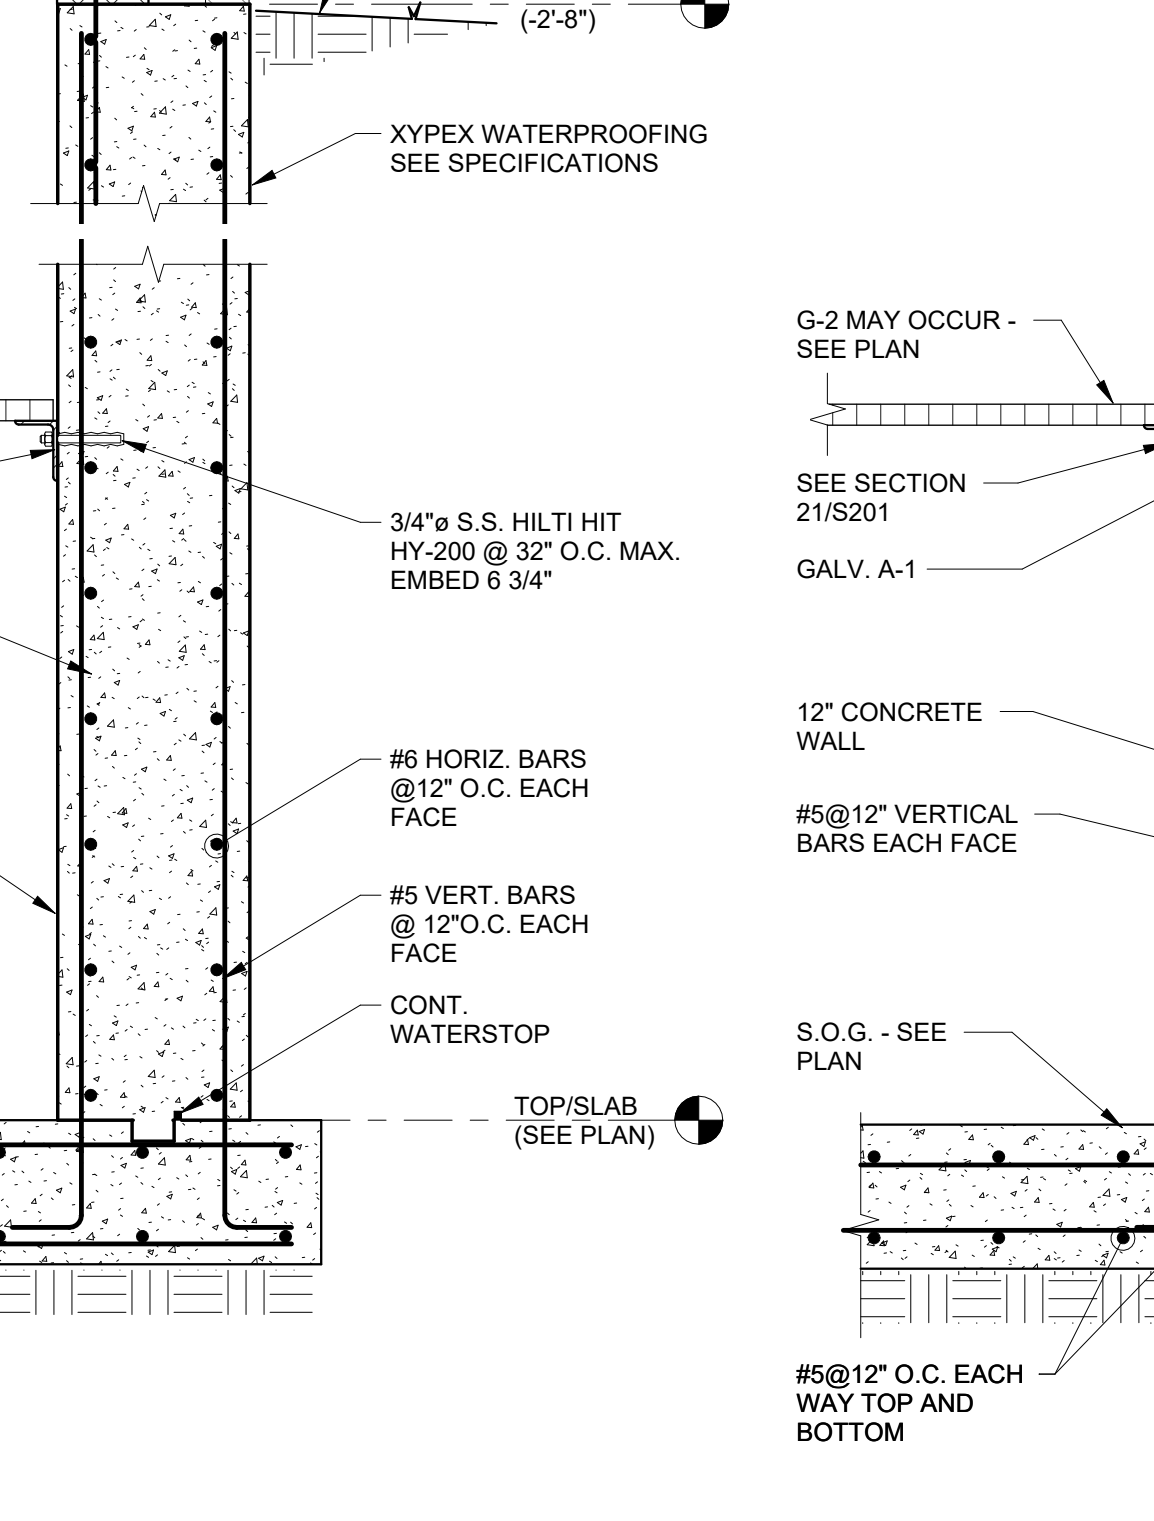

SECTION 22
3/4" = 1'-0"

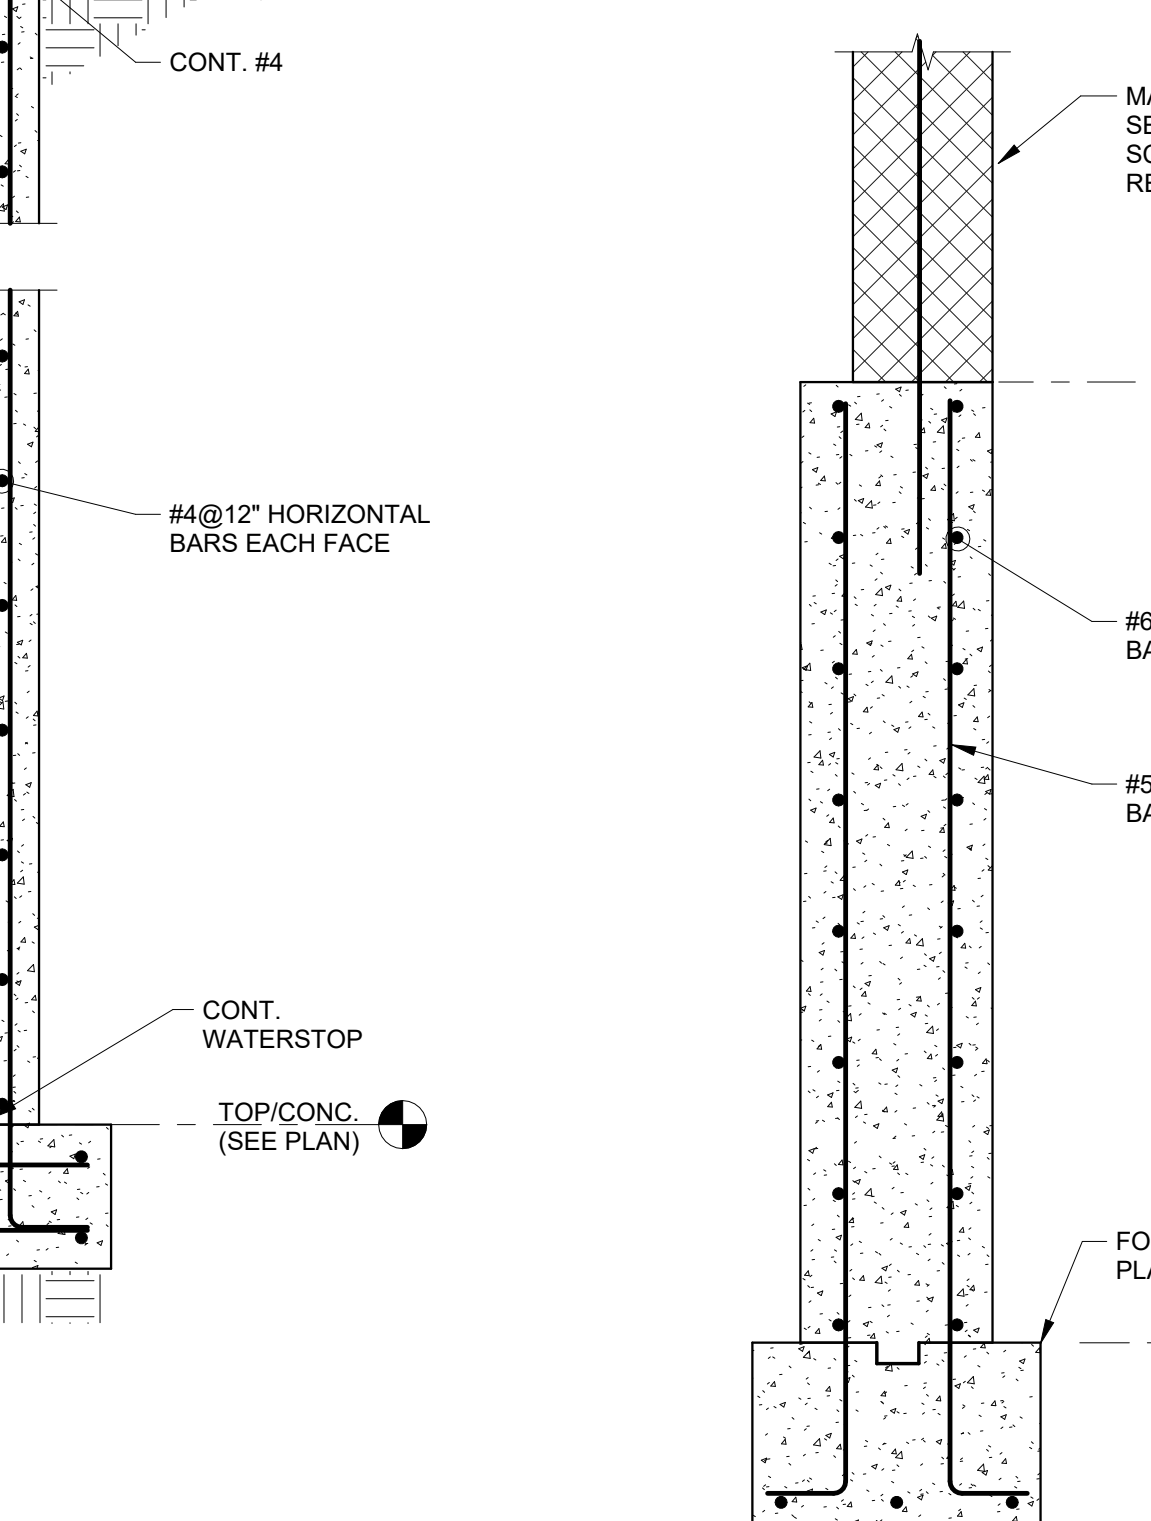

SECTION 23
3/4" = 1'-0"